


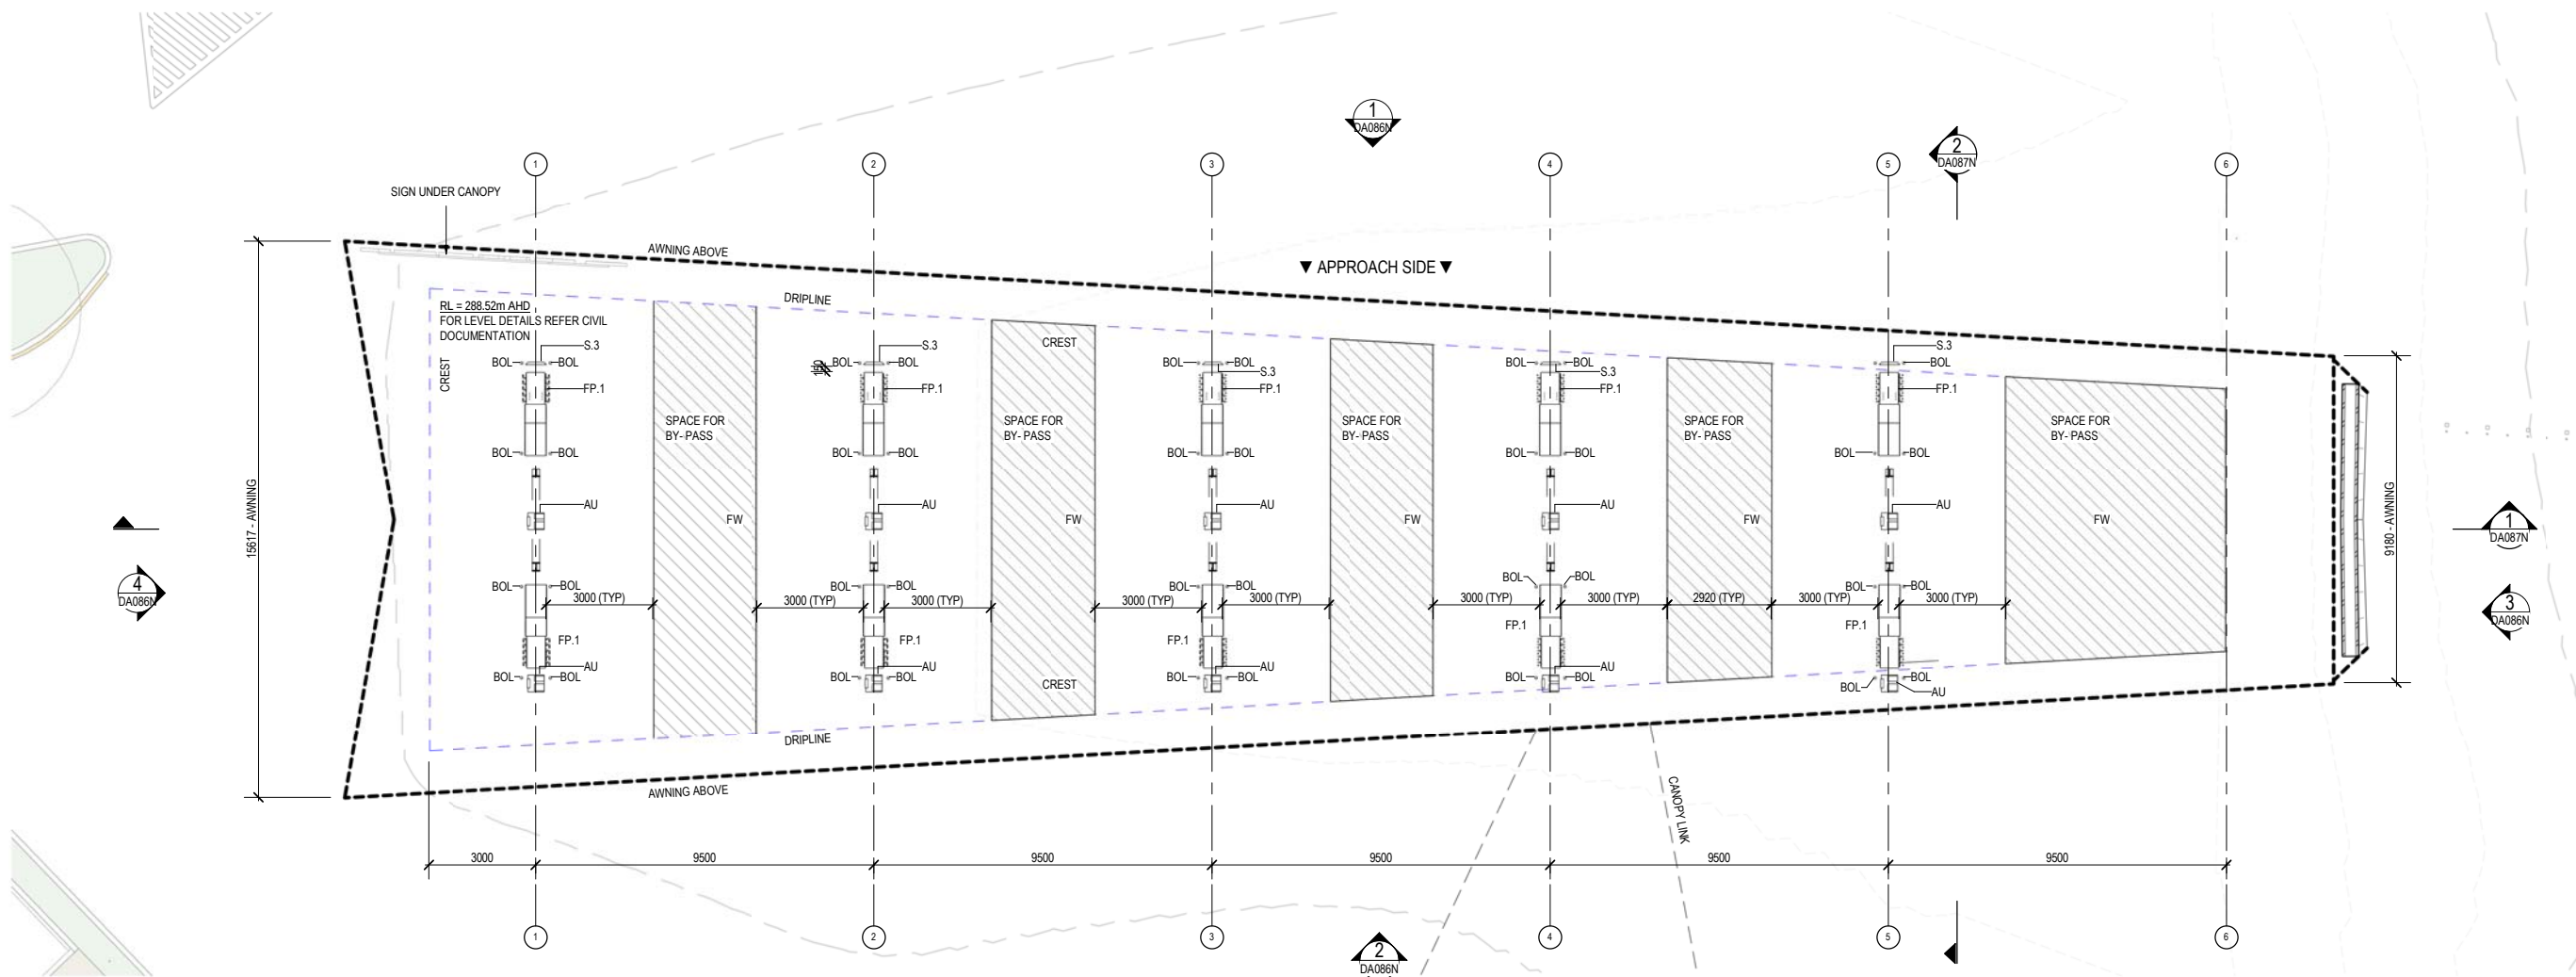


1 GENERAL ARRANGEMENT - CAR CANOPY
1 : 100 @ A1




2 PERSPECTIVE
@ A1

LEGEND:

BOL	MEIAL BOLLARD, ROUND: 165Ø x 1200 HIGH AFFL(TYP)
COL	ANGULAR CANOPY COLUMNS
AU	DRIVEWAY AMENITIES UNIT (TOWEL DISPENSER, WASTE BIN ETC)
FP.1	FUEL PUMP
FW	FLOOR WASTE POINT
	SPACE FOR BY-PASS

 Revisions					General Notes					Drawing Notes					FOR DA NOT TO BE USED DURING CONSTRUCTION					ABN 34 001 485 436					Client					Project					Scale					Project Number				
D2 INFORMATION ONLY 14.04.2021 DC DC D1 INFORMATION ONLY 08.04.2021 DC DC					Do not scale this drawing. The drawing shows design intent only. All dimensions to be checked on site prior to construction or production. Construction details to be confirmed by contractor/manufacturer. This is a computer generated drawing. Do not amend by hand. Figure dimensions are to be used. Contact architect for clarification if dimensions are not clear. All dimensions are in millimeters. All discrepancies and omissions on site must be reported to the architect for their comments or approval prior to commencing work.										Richmond+Ross CONSULTING ENGINEERS AND PROJECT LEADERS 38 Willoughby Road Crows Nest NSW 2065 TEL: (02) 9490 9600 FAX: (02) 94381224										REDEVELOPMENT OF HIGHWAY SERVICE CENTRE PHEASANTS NEST (M31) - CAR CANOPY					1 : 100 @ A1					200451									
																									M31 HUME HIGHWAY PHEASANTS NEST NSW 2574 - NORTHBOUND					Drawing CAR CANOPY- GENERAL ARRANGEMENT														
Issue					Description					Date					Chk					Int					Project Code					Discipline code					Drawing Number					Issue				
																									PNN					AR					DA081N					D2				

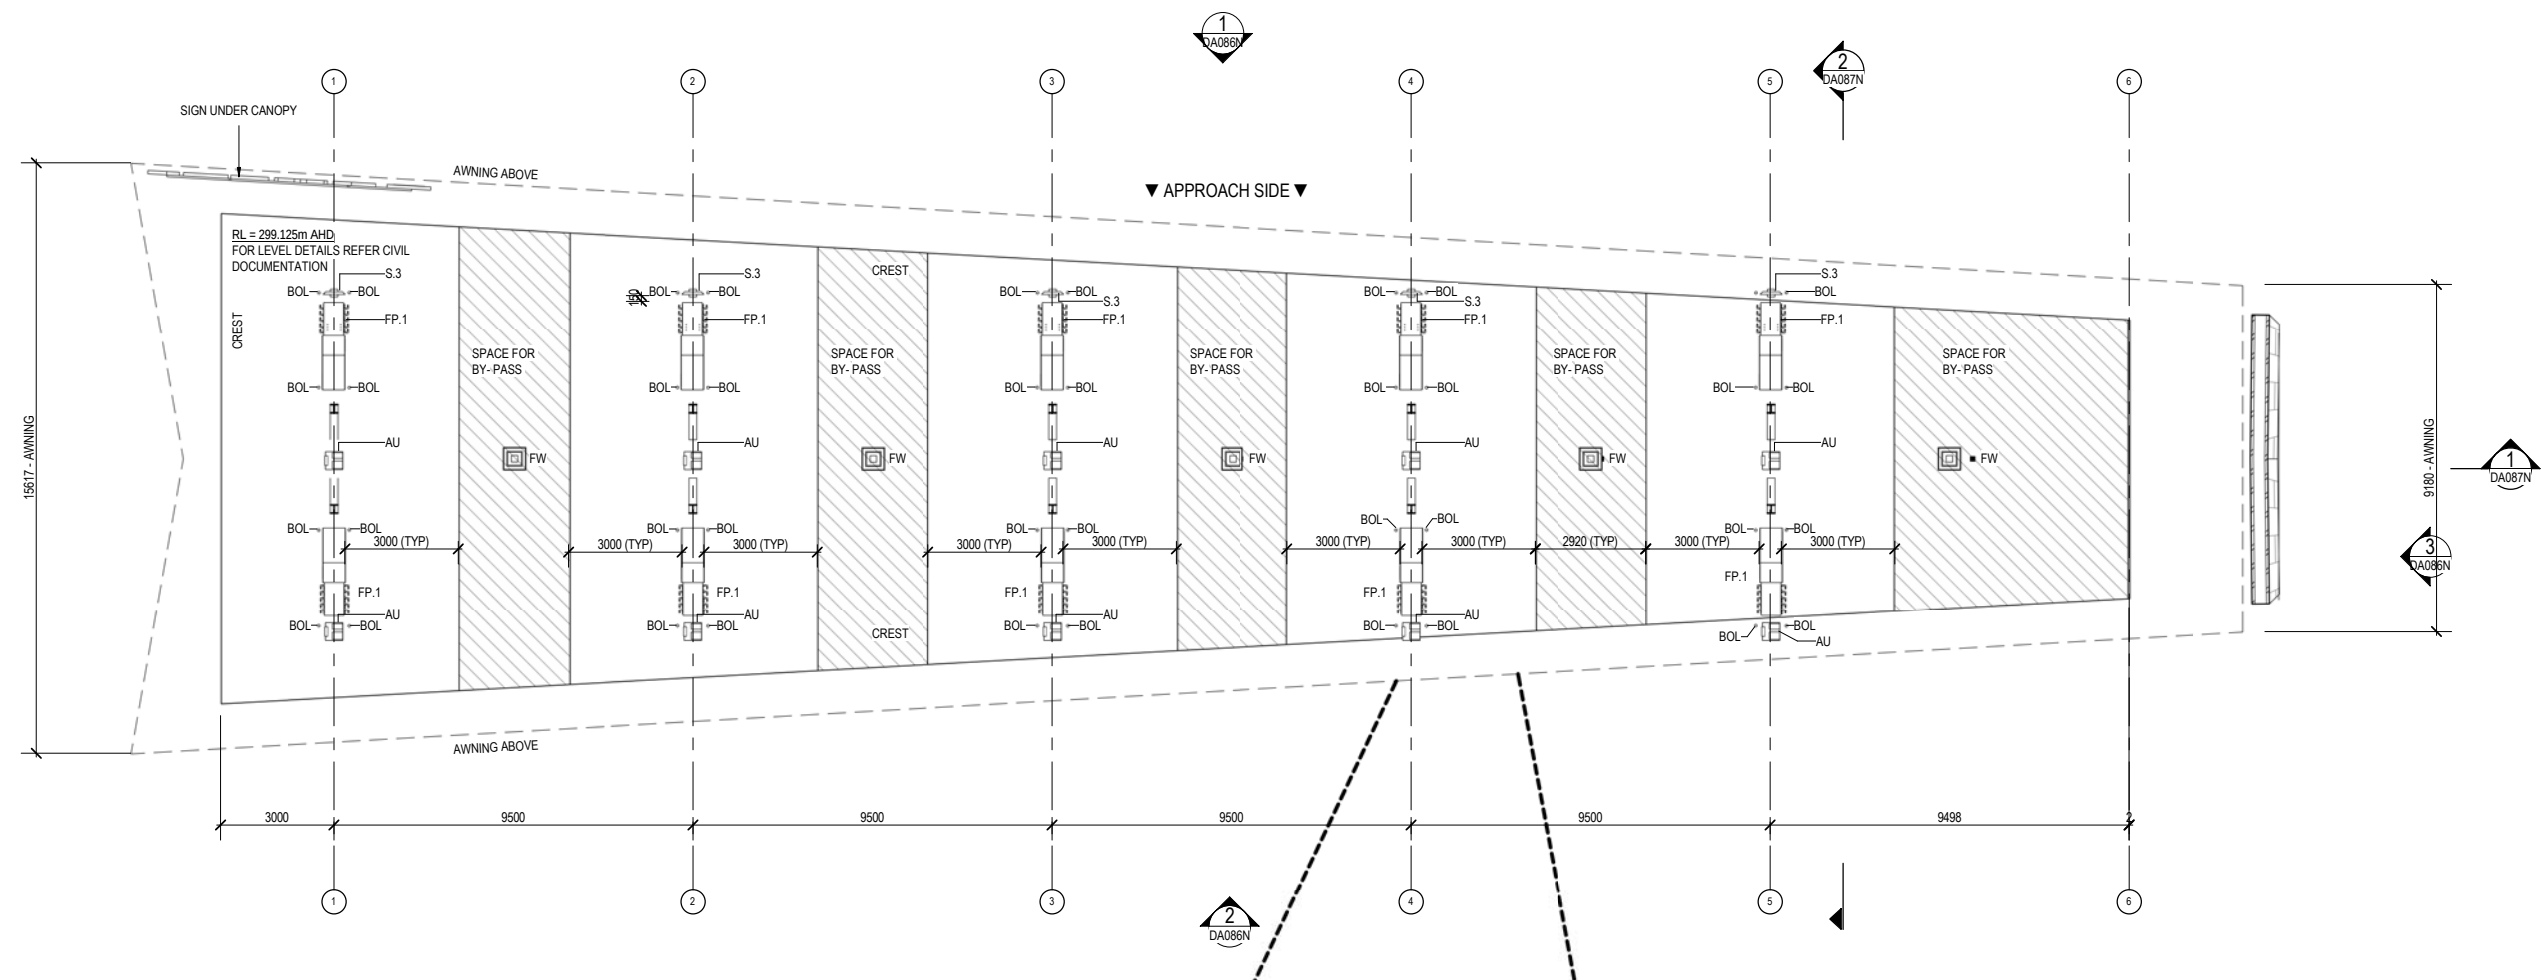




1 GENERAL ARRANGEMENT - CAR CANOPY
1 : 100 @ A1




- LEGEND:**
- BOL MEIAL BOLLARD, ROUND: 165Ø x 1200 HIGH AFFL(TYP)
 - COL ANGLUAR CANOPY COLUMNS
 - AU DRIVEWAY AMENITIES UNIT (TOWEL DISPENSER, WASTE BIN ETC)
 - FP.1 FUEL PUMP
 - FW FLOOR WASTE POINT
 - SPACE FOR BY-PASS


2 PERSPECTIVE
@ A1

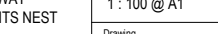Revisions					General Notes					Drawing Notes					FOR DA NOT TO BE USED DURING CONSTRUCTION										ABN 34 001 485 436 Richmond+Ross CONSULTING ENGINEERS AND PROJECT LEADERS 38 Willoughby Road Crows Nest NSW 2065 TEL: (02) 9490 9600 FAX: (02) 94381224					Client										Project REDEVELOPMENT OF HIGHWAY SERVICE CENTRE PHEASANTS NEST (M31) - CAR CANOPY Location M31 HUME HIGHWAY PHEASANTS NEST NSW 2574 - NORTHBOUND					Scale 1 : 100 @ A1 Drawing CAR CANOPY- GENERAL ARRANGEMENT Project Code Discipline code Drawing Number Issue PNS AR DA081S D2					Project Number 200451	
D2	INFORMATION ONLY				14.04.2021	DC	DC	Do not scale this drawing. The drawing shows design intent only. All dimensions to be checked on site prior to construction or production. Construction details to be confirmed by contractor/manufacturer. This is a computer generated drawing. Do not amend by hand. Figure dimensions are to be used. Contact architect for clarification if dimensions are not clear. All dimensions are in millimeters. All discrepancies and omissions on site must be reported to the architect for their comments or approval prior to commencing work.	</				

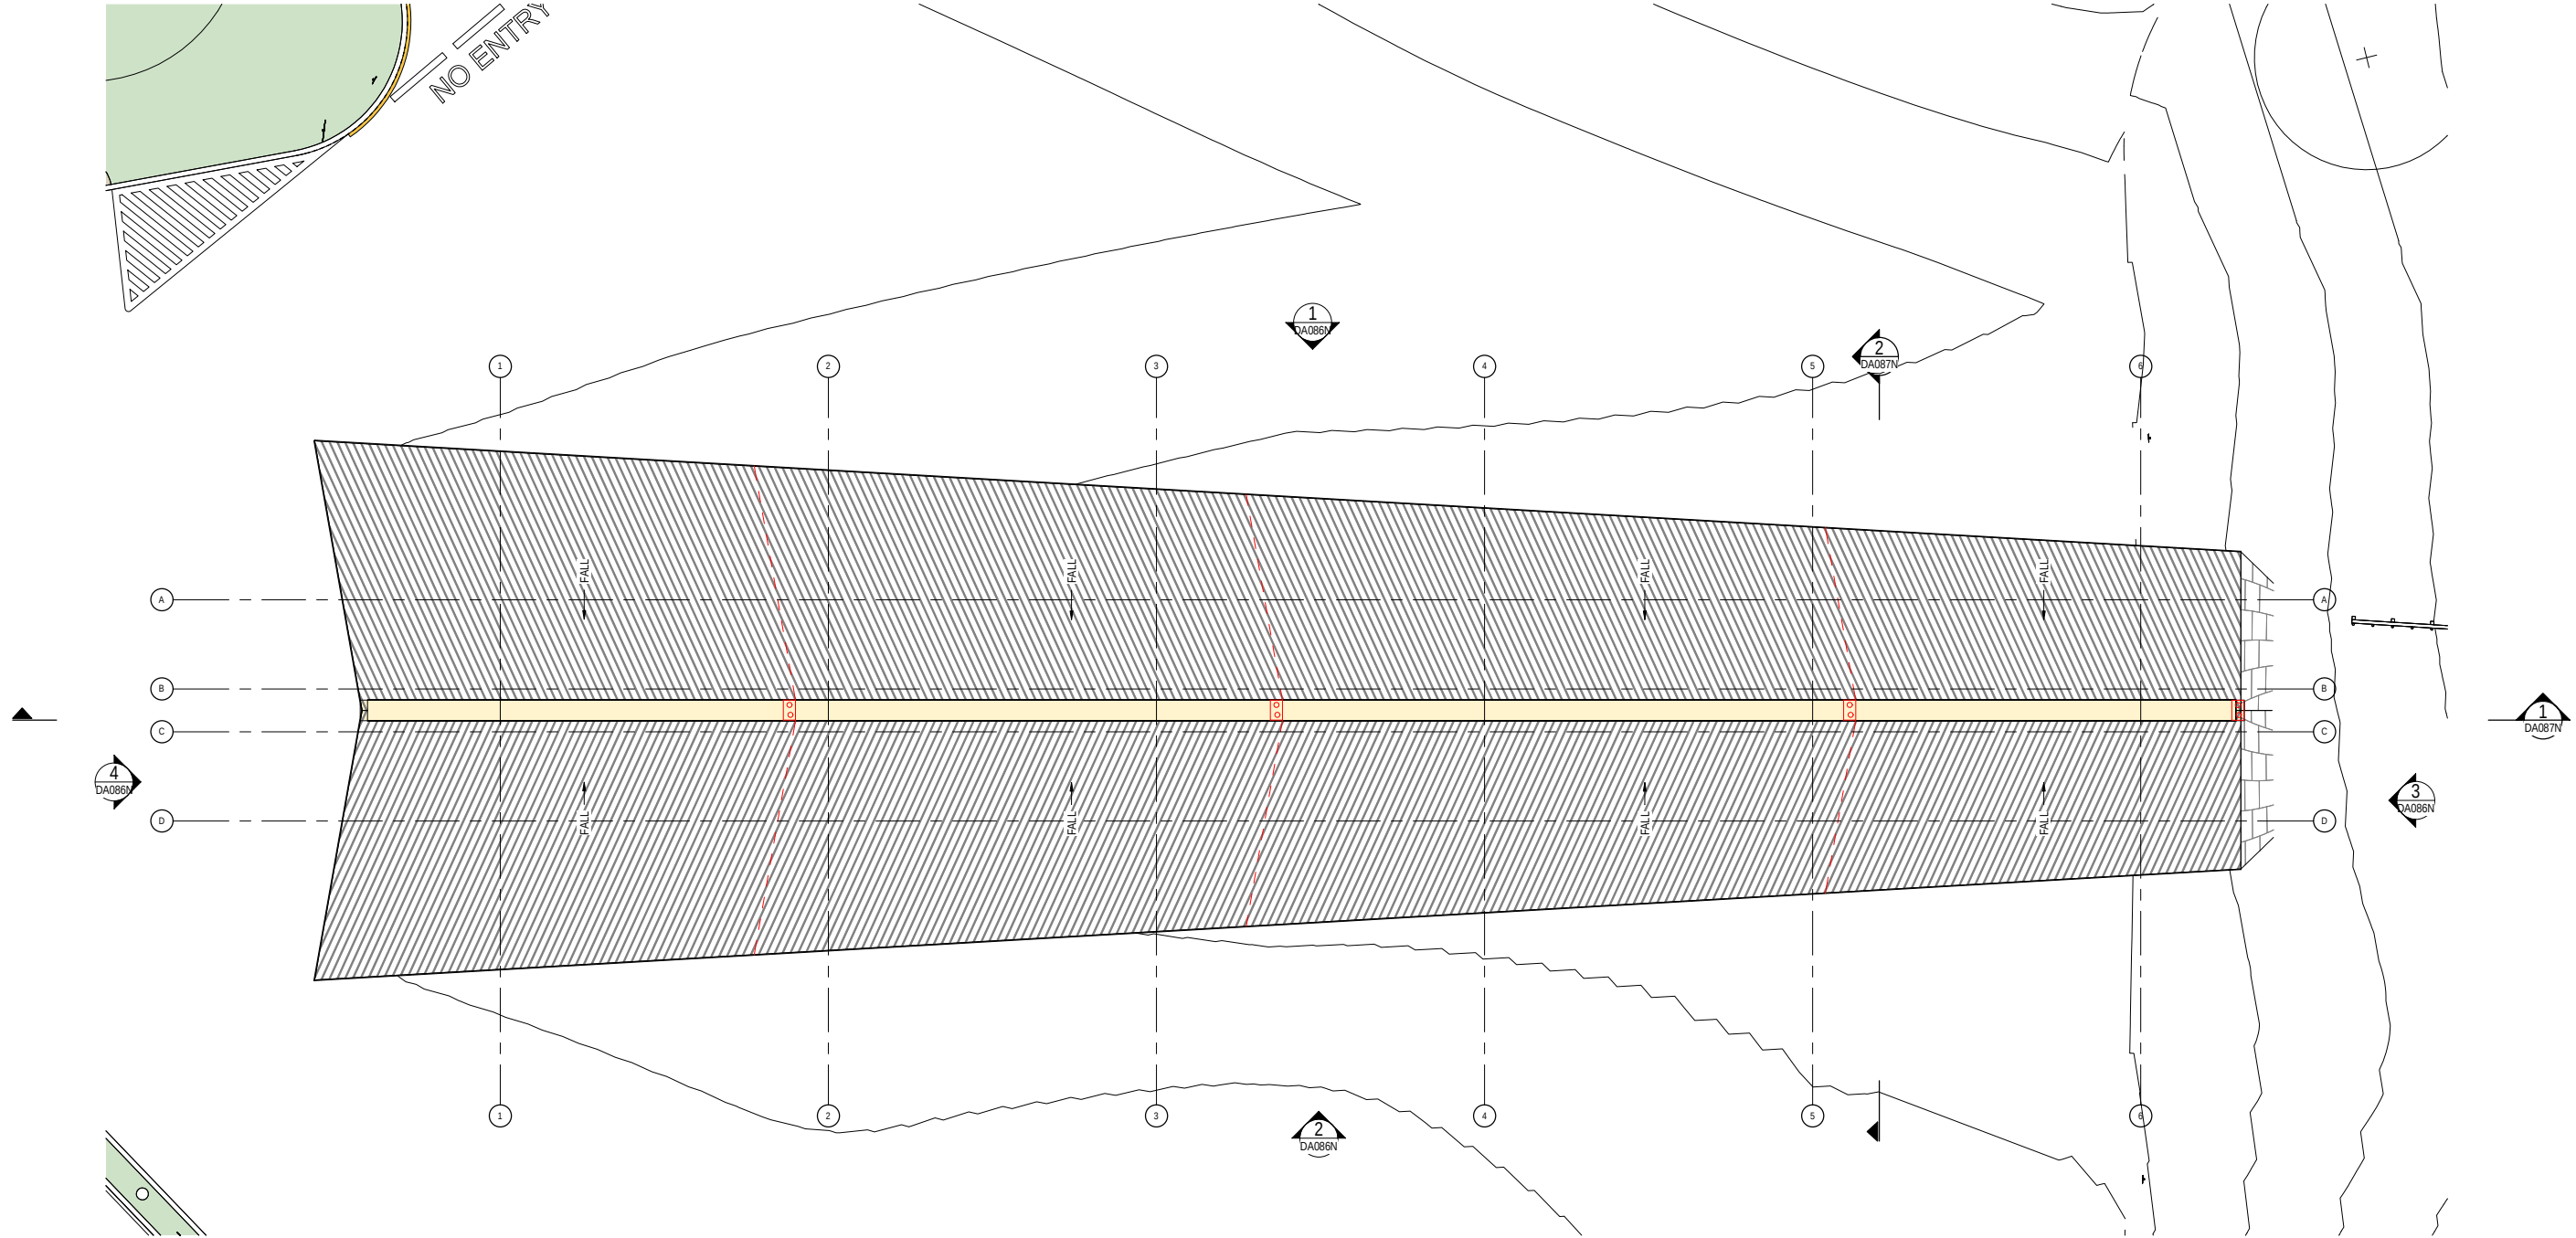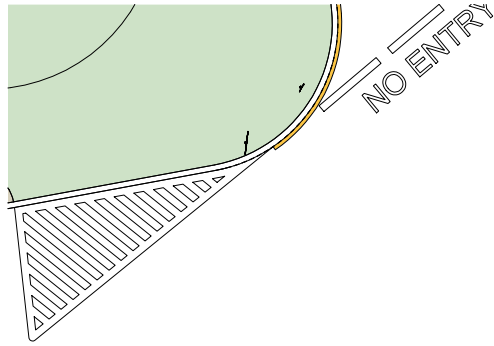


LEGEND:	
	SIPHONIC SYTEM
	BOX GUTTER

 Revisions					General Notes					Drawing Notes					FOR DA NOT TO BE USED DURING CONSTRUCTION										ABN 34 001 485 436 Richmond+Ross CONSULTING ENGINEERS AND PROJECT LEADERS 38 Willoughby Road Crows Nest NSW 2065 TEL: (02) 9450 9600 FAX: (02) 94381224										Client					Project REDEVELOPMENT OF HIGHWAY SERVICE CENTRE PHEASANTS NEST (M31) - CAR CANOPY					Scale 1 : 100 @ A1 Project Number 200451				
D2 D1 INFORMATION ONLY INFORMATION ONLY 14.04.2021 08.04.2021 DC DC DC DC					Do not scale this drawing. The drawing shows design intent only. All dimensions to be checked on site prior to construction or production. Construction details to be confirmed by contractor/manufacturer. This is a computer generated drawing. Do not amend by hand. Figure dimensions are to be used. Contact architect for clarification if dimensions are not clear. All dimensions are in millimeters. All discrepancies and omissions on site must be reported to the architect for their comments or approval prior to commencing work.																				Location M31 HUME HIGHWAY PHEASANTS NEST NSW 2574 - NORTHBOUND					Drawing CAR CANOPY - ROOF PLAN																			
Issue Description Date Chk Int																														Project Code PNN					Discipline code AR					Drawing Number DA082N					Issue D2				

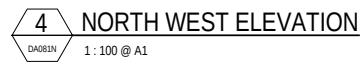


CODE	No.	AREA	DESCRIPTION	MANUFACTURER	COLOUR	IMAGE
MRS	01	BUILDING AND CANOPY ROOF	KLIP-LOK 700 HI-STRENGTH SURFMIST	LYSAGHT OR EQUAL	COLORBOND SURFMIST	
MWC	05	CANOPY - SOFFIT	STRAMIT MONOPANEL	STRAMIT OR EQUAL	WHITE	
PAF	10	CANOPY COLUMNS	PAINT FINISH - DULUX 'BLACK'	DULUX OR EQUAL	BLACK	


Revisions					General Notes					Drawing Notes					FOR DA NOT TO BE USED DURING CONSTRUCTION					ABN 34 001 485 436					Client					Project					Scale					Project Number																								
					Do not scale this drawing. The drawing shows design intent only. All dimensions to be checked on site prior to construction or production. Construction details to be confirmed by contractor/manufacturer. This is a computer generated drawing. Do not amend by hand. Figure dimensions are to be used. Contact architect for clarification if dimensions are not clear. All dimensions are in millimeters. All discrepancies and omissions on site must be reported to the architect for their comments or approval prior to commencing work.															Richmond+Ross CONSULTING ENGINEERS AND PROJECT LEADERS 38 Willoughby Road Crows Nest NSW 2085 TEL: (02) 9490 9600 FAX: (02) 94381224										REDEVELOPMENT OF HIGHWAY SERVICE CENTRE PHEASANTS NEST (M31) - CAR CANOPY					1 : 100 @ A1					200451																								
																																			Drawing					CAR CANOPY- ELEVATIONS																								
D2 D1					INFORMATION ONLY INFORMATION ONLY					14.04.2021 08.04.2021					DC DC					DC DC															Location					M31 HUME HIGHWAY PHEASANTS NEST NSW 2574 - NORTHBOUND					Project Code					Discipline code					Drawing Number					Issue				
Issue					Description					Date					Chk					Int																									PNN					AR					DA086N					D2				

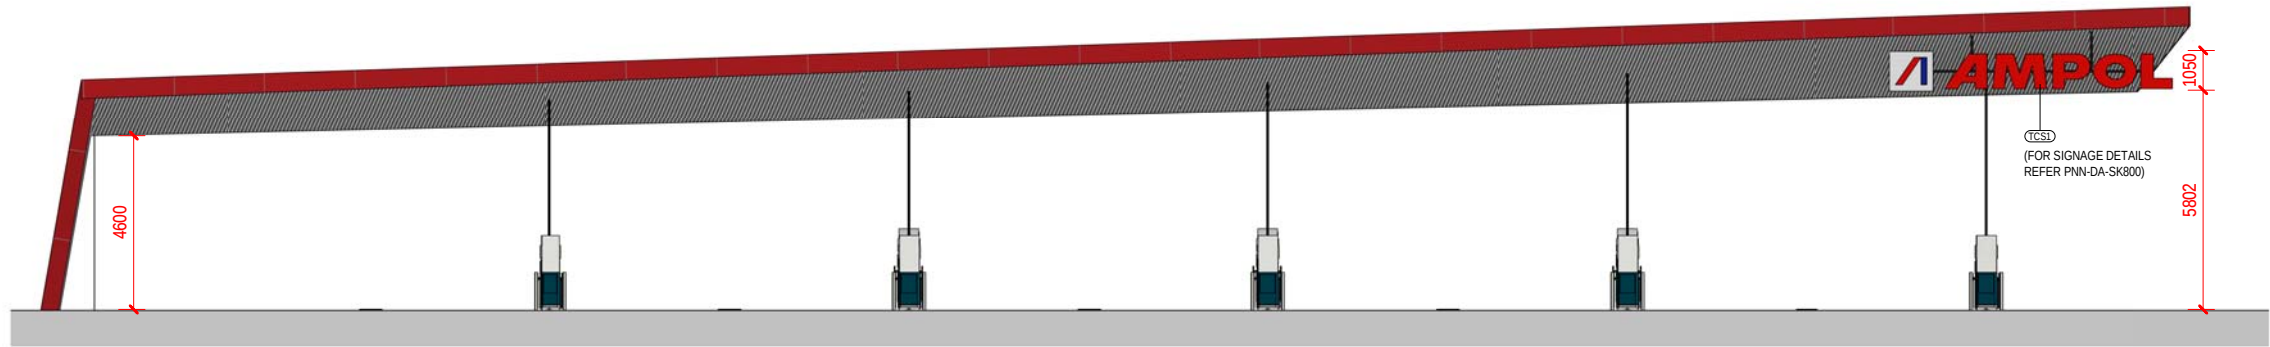


5 NORTH WEAST
DA082S 1 : 100 @ A1

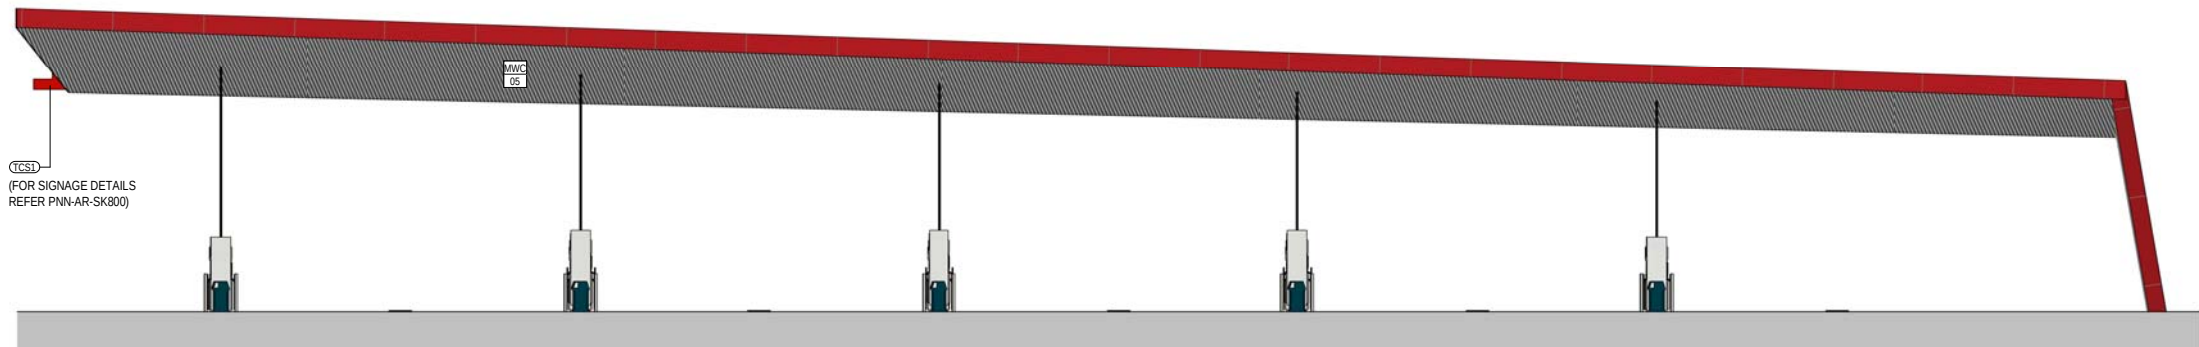

2 SOUTH EAST ELEVATION
DA082S 1 : 100 @ A1

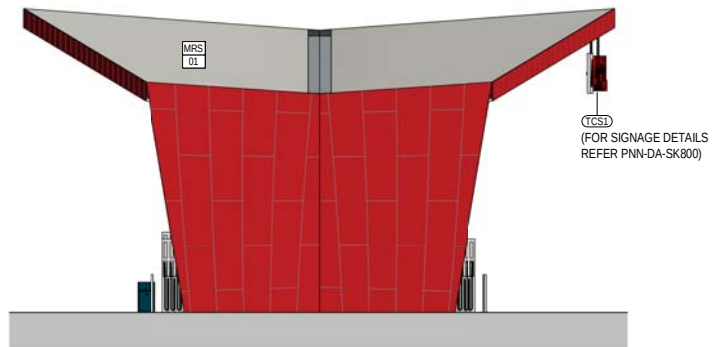

3 NORTH EAST ELEVATION
DA082S 1 : 100 @ A1

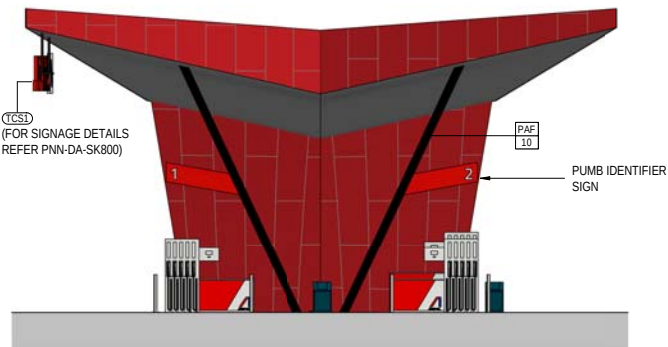


4 SOUTH WEST ELEVATION
DA082S 1 : 100 @ A1


EXTERNAL FINISHES SCHEDULE

CODE	No.	AREA	DESCRIPTION	MANUFACTURER	COLOUR	IMAGE
MRS	01	BUILDING AND CANOPY ROOF	KLIP-LOK 700 HI-STRENGTH SURFMIST	LYSAGHT OR EQUAL	COLORBOND SURFMIST	
MWC	05	CANOPY - SOFFIT	STRAMIT MONOPANEL	STRAMIT OR EQUAL	WHITE	
PAF	10	CANOPY COLUMNS	PAINT FINISH - DULUX 'BLACK'	DULUX OR EQUAL	BLACK	

Revisions					General Notes					Drawing Notes					FOR DA NOT TO BE USED DURING CONSTRUCTION					ABN 34 001 485 436					Client					Project					Scale					Project Number																			
D2 INFORMATION ONLY D1 INFORMATION ONLY					14.04.2021 08.04.2021					DC DC DC DC					Do not scale this drawing. The drawing shows design intent only. All dimensions to be checked on site prior to construction or production. Construction details to be confirmed by contractor/manufacturer. This is a computer generated drawing. Do not amend by hand. Figure dimensions are to be used. Contact architect for clarification if dimensions are not clear. All dimensions are in millimeters. All discrepancies and omissions on site must be reported to the architect for their comments or approval prior to commencing work.										Richmond+Ross CONSULTING ENGINEERS AND PROJECT LEADERS 38 Willoughby Road Crows Nest NSW 2065 TEL: (02) 9490 9600 FAX: (02) 94381224										REDEVELOPMENT OF HIGHWAY SERVICE CENTRE PHEASANTS NEST (M31) - CAR CANOPY					1 : 100 @ A1					200451														
																														Location					CAR CANOPY- ELEVATIONS																								
Issue Description					Date					Chk Int																									M31 HUME HIGHWAY PHEASANTS NEST NSW 2574 - NORTHBOUND					Project Code					Discipline code					Drawing Number					Issue				
	PNS					AR					DA086S					D2				

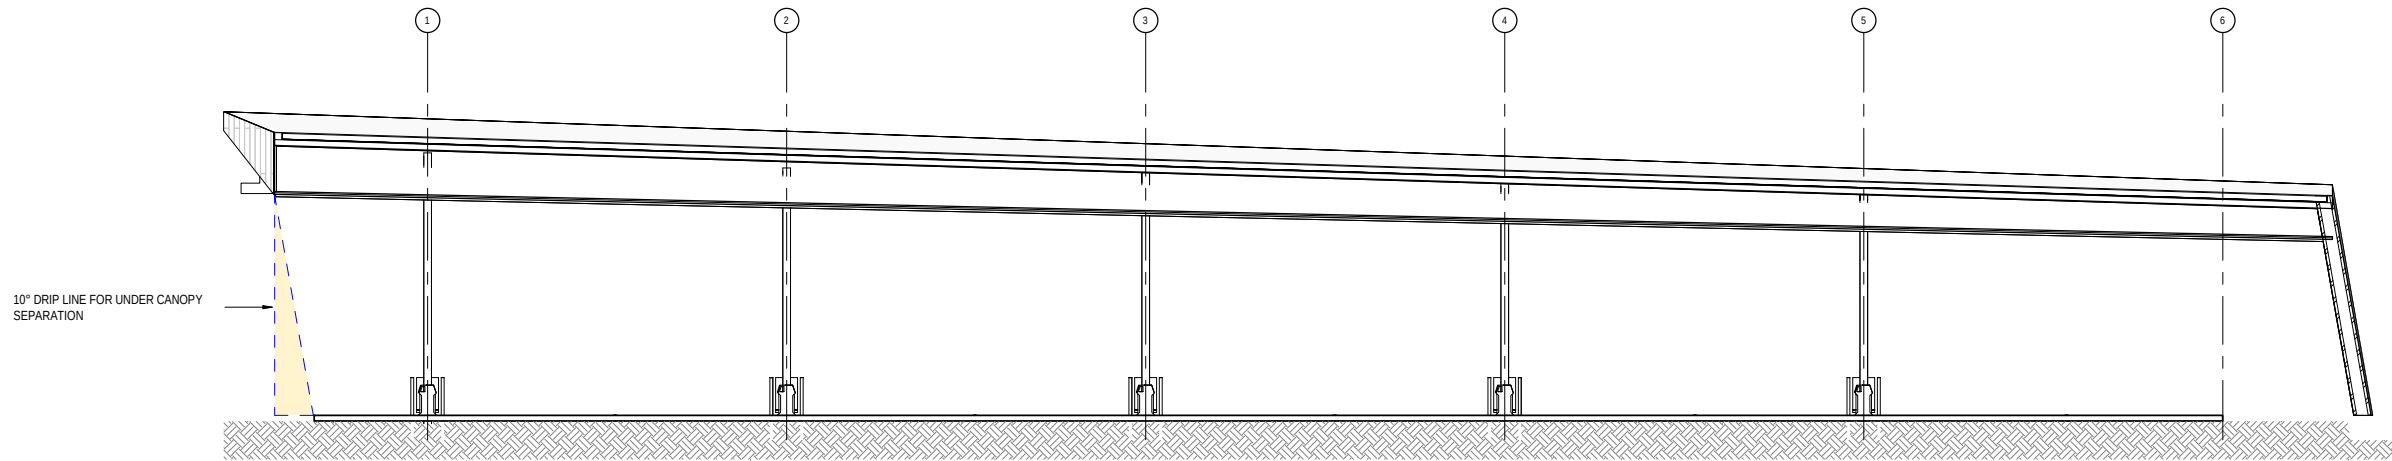


1 CAR CANOPY SECTION 01
1 : 100 @ A1

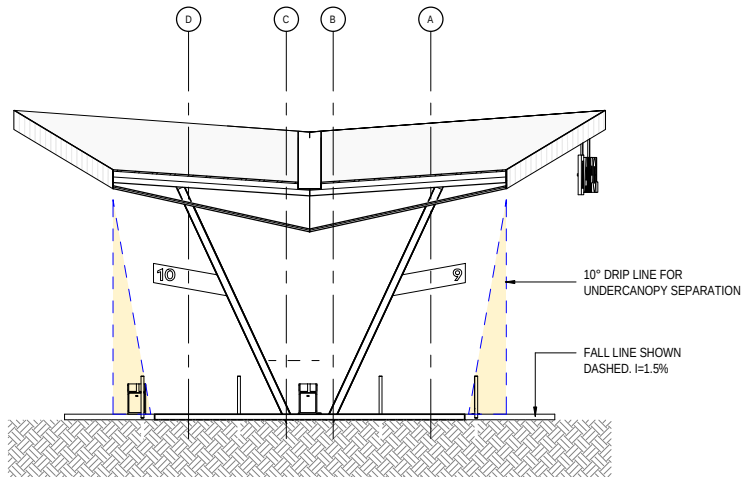


2 CAR CANOPY SECTION 02
1 : 100 @ A1

Revisions				General Notes				Drawing Notes				FOR DA NOT TO BE USED DURING CONSTRUCTION				Client				Project				Scale				Project Number			
D2				D1				14.04.2021				DC				DC				REDEVELOPMENT OF HIGHWAY				1 : 100 @ A1				200451			
D1				INFORMATION ONLY				08.04.2021				DC				DC				SERVICE CENTRE PHEASANTS NEST				CAR CANOPY - SECTIONS							
Issue				Description				Date				Chk				Int				Location				Project Code				Discipline code			
																				M31 HUME HIGHWAY PHEASANTS NEST				PNN				Drawing Number			
																				NSW 2574 - NORTHBOUND				AR				Issue			
																								DA087N				D2			

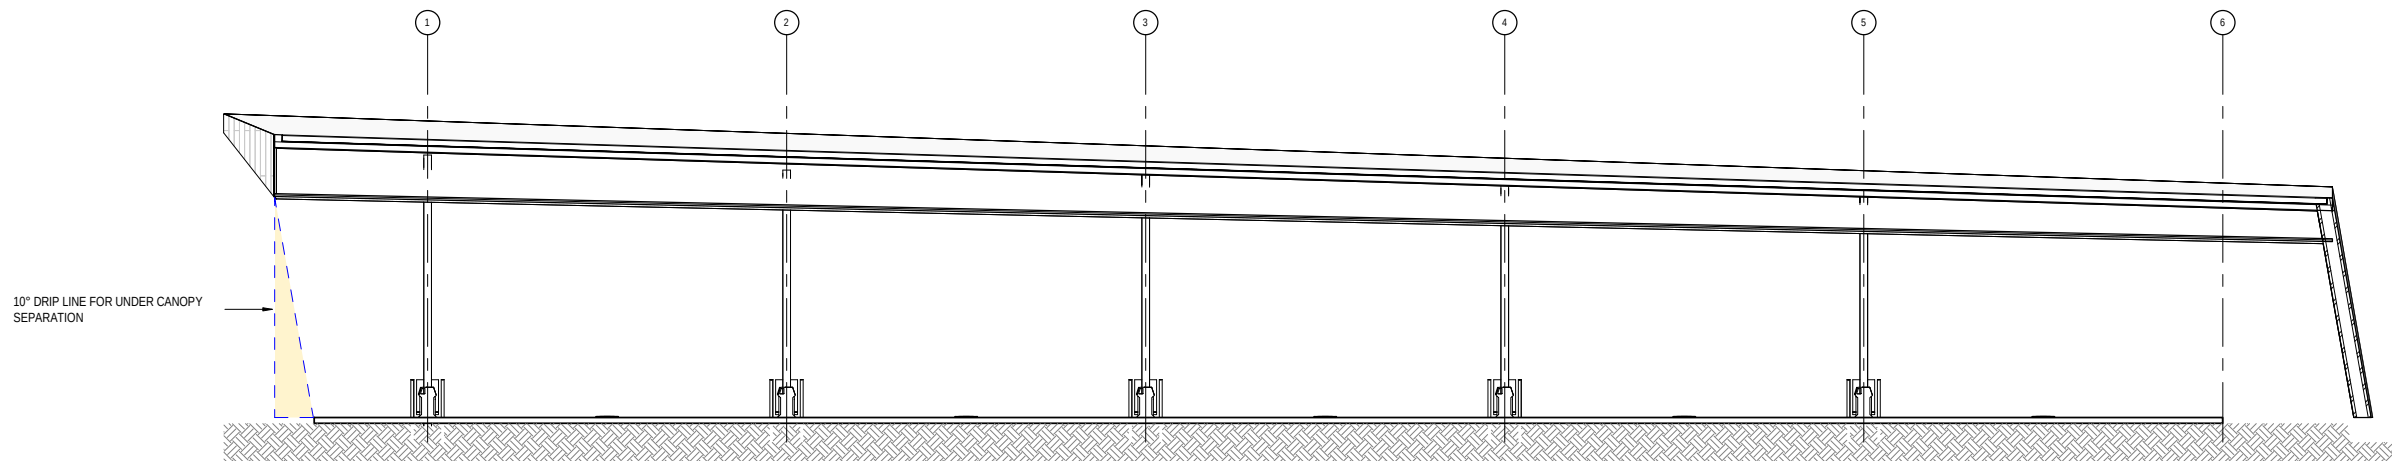

2 CAR CANOPY SECTION 01
1 : 100 @ A1

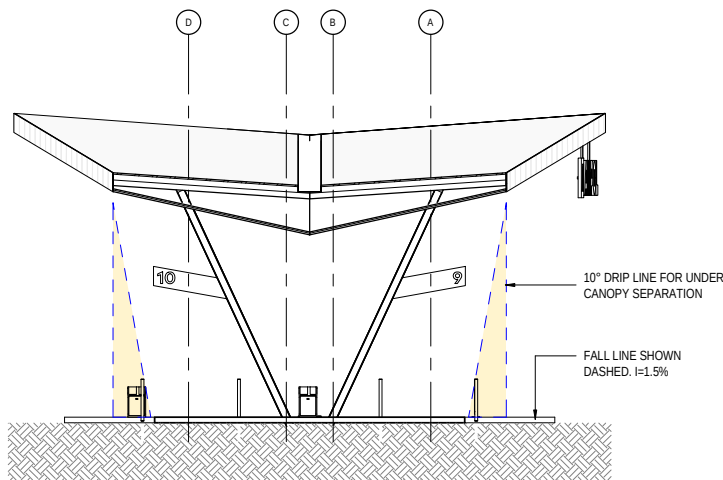



1 CAR CANOPY SECTION 02
1 : 100 @ A1

Revisions					General Notes					Drawing Notes					FOR DA NOT TO BE USED DURING CONSTRUCTION					ABN 34 001 485 436					Client					Project					Scale					Project Number														
					Do not scale this drawing. The drawing shows design intent only. All dimensions to be checked on site prior to construction or production. Construction details to be confirmed by contractor/manufacturer. This is a computer generated drawing. Do not amend by hand. Figure dimensions are to be used. Contact architect for clarification if dimensions are not clear. All dimensions are in millimeters. All discrepancies and omissions on site must be reported to the architect for their comments or approval prior to commencing work.																				REDEVELOPMENT OF HIGHWAY SERVICE CENTRE PHEASANTS NEST (M31) - CAR CANOPY					1 : 100 @ A1					200451																			
D2					14.04.2021					DC					DC										Location					M31 HUME HIGHWAY PHEASANTS NEST					Drawing					CAR CANOPY- SECTIONS														
D1					08.04.2021					DC					DC										38 Willoughby Road Crows Nest NSW 2065 TEL: (02) 9490 9600 FAX: (02) 94381224					M31 HUME HIGHWAY PHEASANTS NEST NSW 2574 - NORTHBOUND					Project Code					Discipline code					Drawing Number					Issue				
Issue					Description					Date					Chk					Int										PNS					AR					DA087S					D2									



BOL.1	CONCRETE BOLLARD, ROUND: 600ø x 1400 HIGH AFFL
COL	ANGULAR CANOPY COLUMNS
AU	DRIVEWAY AMENITIES UNIT (TOWEL DISPENSER, WASTE BIN ETC)
FP.1	FUEL PUMP TYPE A (REFER OTHERS)
FP.2	FUEL PUMP TYPE B (REFER OTHERS)
FP.3	FUEL PUMP TYPE C (REFER OTHERS)
FW	FLOOR WASTE POINT

 Revisions					General Notes					Drawing Notes					FOR DA NOT TO BE USED DURING CONSTRUCTION															Client										Project					Scale					Project Number																			
					Do not scale this drawing. The drawing shows design intent only. All dimensions to be checked on site prior to construction or production. Construction details to be confirmed by contractor/manufacturer. This is a computer generated drawing. Do not amend by hand. Figure dimensions are to be used. Contact architect for clarification if dimensions are not clear. All dimensions are in millimeters. All discrepancies and omissions on site must be reported to the architect for their comments or approval prior to commencing work.																				ABN 34 001 485 436										REDEVELOPMENT OF HIGHWAY SERVICE CENTRE PHEASANTS NEST (M31) - TRUCK CANOPY					1 : 100 @ A1					200451																								
D2 D1					ISSUE FOR DA ISSUE FOR DA					14.04.2021 08.04.2021					DC DC					DC DC																				Location					Drawing HEAVY VEHICLE CANOPY- GENERAL ARRANGEMENT																								
Issue					Description					Date					Chk					Int																				M31 HUME HIGHWAY PHEASANTS NEST NSW 2574 - NORTHBOUND					Project Code					Discipline code					Drawing Number					Issue									
	PNN					AR					DA091N					D2				

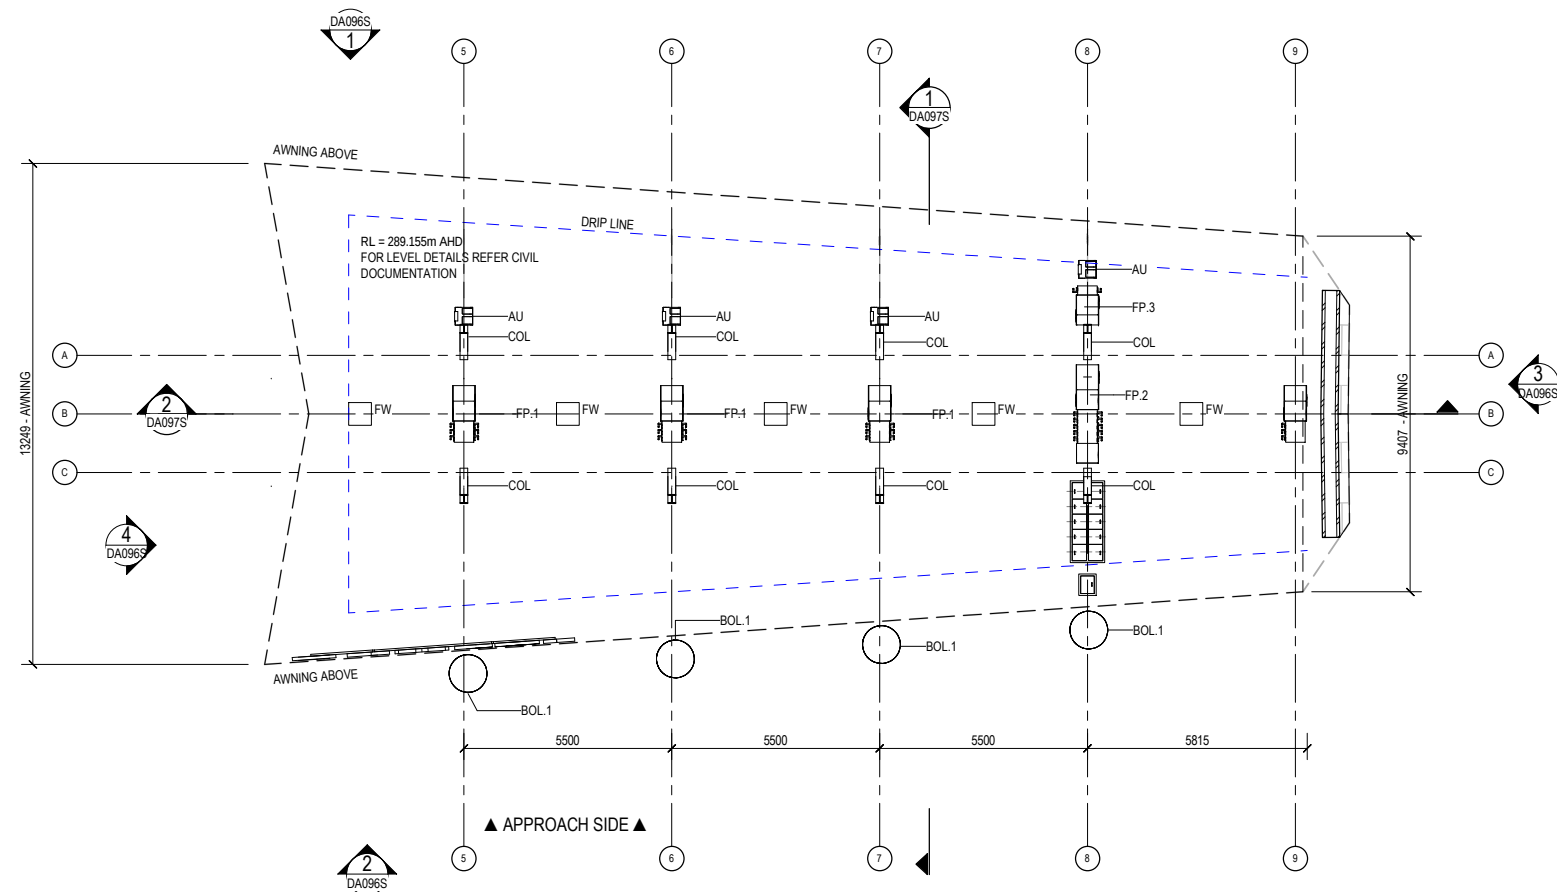



1 GENERAL ARRANGEMENT - TRUCK CANOPY
1:100 @ A1




2 PERSPECTIVE
@ A1


LEGEND:


BOL.1	CONCRETE BOLLARD, ROUND: 600Ø x 1400 HIGH AFFL
COL	ANGULAR CANOPY COLUMNS
AU	DRIVEWAY AMENITIES UNIT (TOWEL DISPENSER, WASTE BIN ETC)
FP.1	FUEL PUMP TYPE A (REFER OTHERS)
FP.2	FUEL PUMP TYPE B (REFER OTHERS)
FP.3	FUEL PUMP TYPE C (REFER OTHERS)
FW	FLOOR WASTE POINT

 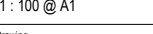Revisions					General Notes					Drawing Notes					FOR DA NOT TO BE USED DURING CONSTRUCTION										ABN 34 001 485 436 Richmond+Ross CONSULTING ENGINEERS AND PROJECT LEADERS 38 Willoughby Road Crows Nest NSW 2065 TEL: (02) 9490 9600 FAX: (02) 94381224					Client										Project					Scale					Project Number									
D2 D1					ISSUE FOR DA ISSUE FOR DA					14.04.2021 08.04.2021					DC DC					DC DC															REDEVELOPMENT OF HIGHWAY SERVICE CENTRE PHEASANTS NEST (M31) - TRUCK CANOPY					1 : 100 @ A1					200451														
																																			Drawing HEAVY VEHICLE CANOPY- GENERAL ARRANGEMENT																								
Issue					Description					Date					Chk					Int															M31 HUME HIGHWAY PHEASANTS NEST NSW 2574 - NORTHBOUND					Project Code					Discipline code					Drawing Number					Issue				
	PNS					AR					DA091S					D2				

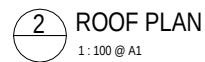

BOX GUTTER

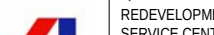
Revisions					General Notes					Drawing Notes					FOR DA NOT TO BE USED DURING CONSTRUCTION										ABN 34 001 485 436 Richmond+Ross CONSULTING ENGINEERS AND PROJECT LEADERS 38 Willoughby Road Crows Nest NSW 2065 TEL: (02) 9490 9600 FAX: (02) 94381224					Client 					Project REDEVELOPMENT OF HIGHWAY SERVICE CENTRE PHEASANTS NEST (M31) - TRUCK CANOPY Location M31 HUME HIGHWAY PHEASANTS NEST NSW 2574 - NORTHBOUND					Scale 1 : 100 @ A1					Project Number 200451	
D2 DC					ISSUE FOR DA					14/04/2021 DC					DC					DC					DC					DC					DC					DC					DC					DC	
Issue					Description					Date					Chk					Int					Do not scale this drawing. The drawing shows design intent only. All dimensions to be checked on site prior to construction or production. Construction details to be confirmed by contractor/manufacturer. This is a computer generated drawing. Do not amend by hand. Figure dimensions are to be used. Contact architect for clarification if dimensions are not clear. All dimensions are in millimeters. All discrepancies and omissions on site must be reported to the architect for their comments or approval prior to commencing work.					Drawing					HEAVY VEHICLE CANOPY-ROOF PLAN					Project Code					Discipline code					Drawing Number					Issue	

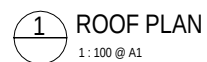


BOX GUTTER


Revisions D2 D1 ISSUE FOR DA ISSUE FOR DA 14.04.2021 08.04.2021 DC DC DC DC Issue Description Date Chk Int					General Notes Do not scale this drawing. The drawing shows design intent only. All dimensions to be checked on site prior to construction or production. Construction details to be confirmed by contractor/manufacturer. This is a computer generated drawing. Do not amend by hand. Figure dimensions are to be used. Contact architect for clarification if dimensions are not clear. All dimensions are in millimeters. All discrepancies and omissions on site must be reported to the architect for their comments or approval prior to commencing work.					Drawing Notes					FOR DA NOT TO BE USED DURING CONSTRUCTION 					ABN 34 001 485 436 Richmond+Ross CONSULTING ENGINEERS AND PROJECT LEADERS 38 Willoughby Road Crows Nest NSW 2065 TEL: (02) 9490 9600 FAX: (02) 94381224					Client 					Project REDEVELOPMENT OF HIGHWAY SERVICE CENTRE PHEASANTS NEST (M31) - TRUCK CANOPY Location M31 HUME HIGHWAY PHEASANTS NEST NSW 2574 - NORTHBOUND					Scale 1 : 100 @ A1 Project Number 200451 Drawing HEAVY VEHICLE CANOPY- ROOF PLAN Project Code Discipline code Drawing Number Issue PNS AR DA092S D2				
---	--	--	--	--	---	--	--	--	--	---------------	--	--	--	--	---	--	--	--	--	---	--	--	--	--	---	--	--	--	--	--	--	--	--	--	--	--	--	--	--

EXTERNAL FINISHES SCHEDULE

 CODE	No.	AREA	DESCRIPTION	MANUFACTURER	COLOUR	IMAGE
MRS	01	BUILDING AND CANOPY ROOF	KLIP-LOK 700 HI-STRENGTH SURFMIST	LYSAGHT OR EQUAL	COLORBOND SURFMIST	
MWC	04	CANOPY - FASCIA & REAR WAL	AODELI 'ORIENT RED' METALLIC	AODELI OR EQUAL	ORIENT RED	
MWC	05	CANOPY - SOFFIT	STRAMIT MONOPANEL	STRAMIT OR EQUAL	WHITE	
PAF	10	CANOPY COLUMNS	PAINT FINISH - DULUX 'BLACK'	DULUX OR EQUAL	BLACK	

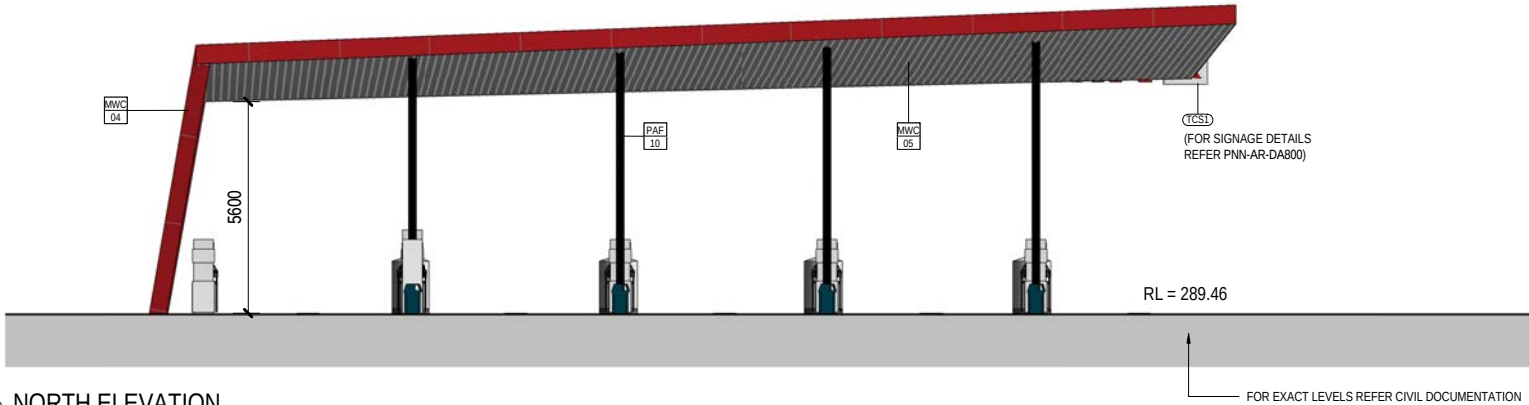


4 NORTH ELEVATION
A101 1 : 100 @ A1

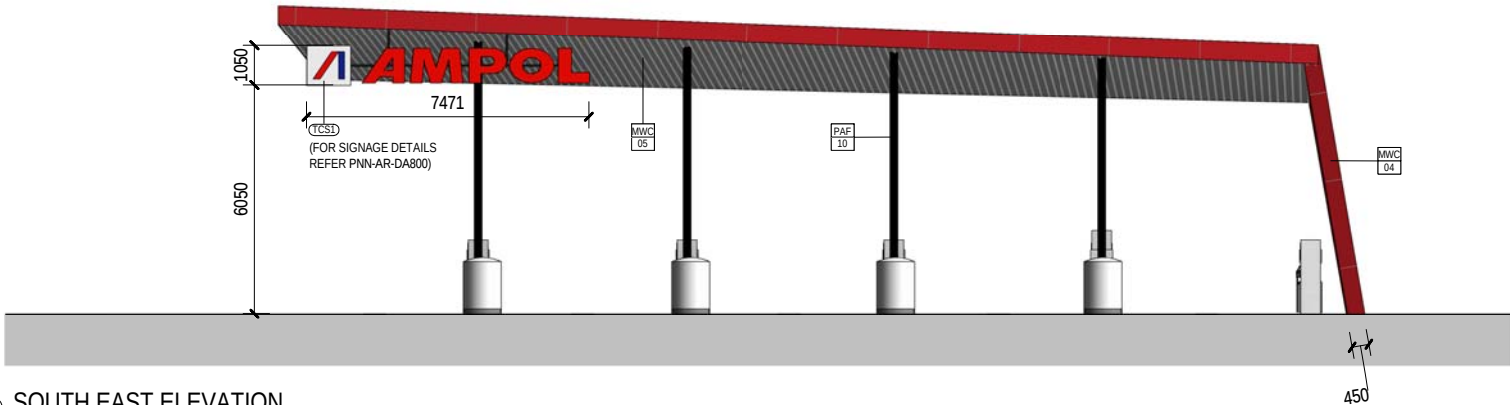

1 SOUTH EAST ELEVATION
A101 1 : 100 @ A1






2 NORTH EAST ELEVATION
A101 1 : 100 @ A1

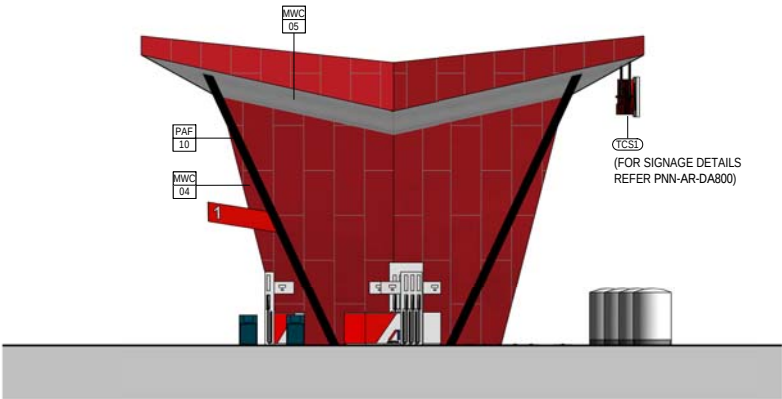


3 SOUTH WEST ELEVATION
A101 1 : 100 @ A1

Revisions					General Notes					Drawing Notes					FOR DA NOT TO BE USED DURING CONSTRUCTION					ABN 34 001 485 436					Client					Project					Scale					Project Number																			
					Do not scale this drawing. The drawing shows design intent only. All dimensions to be checked on site prior to construction or production. Construction details to be confirmed by contractor/manufacturer. This is a computer generated drawing. Do not amend by hand. Figure dimensions are to be used. Contact architect for clarification if dimensions are not clear. All dimensions are in millimeters. All discrepancies and omissions on site must be reported to the architect for their comments or approval prior to commencing work.															REDEVELOPMENT OF HIGHWAY SERVICE CENTRE PHEASANTS NEST (M31) - TRUCK CANOPY					M31 HUME HIGHWAY PHEASANTS NEST NSW 2574 - NORTHBOUND					1 : 100 @ A1					200451																								
																														Drawing					HEAVY VEHICLE CANOPY ELEVATIONS																								
																														Project Code					Discipline code					Drawing Number					Issue														
D2 D1					ISSUE FOR DA ISSUE FOR DA					14.04.2021 08.04.2021					DC DC					DC DC																																							
Issue					Description					Date					Chk					Int																																							

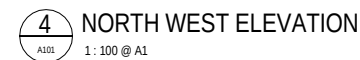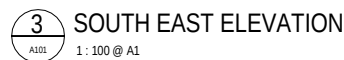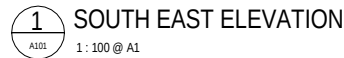


CODE	No.	AREA	DESCRIPTION	MANUFACTURER	COLOR	IMAGE
MRS	01	BUILDING AND CANOPY ROOF	KLIP-LOK 700 HI-STRENGTH SURFMIST	LYSAGHT OR EQUAL	COLORBOND SURFMIST	
MWC	04	CANOPY - FASCIA & REAR WAL	AODELI 'ORIENT RED' METALLIC	AODELI OR EQUAL	ORIENT RED	
MWC	05	CANOPY - SOFFIT	STRAMIT MONOPANEL	STRAMIT OR EQUAL	WHITE	
PAF	10	CANOPY COLUMNS	PAINT FINISH - DULUX 'BLACK'	DULUX OR EQUAL	BLACK	

Revisions						General Notes		Drawing Notes		FOR DA NOT TO BE USED DURING CONSTRUCTION				Project REDEVELOPMENT OF HIGHWAY SERVICE CENTRE PHEASANTS NEST (M31) - TRUCK CANOPY		Scale 1 : 100 @ A1		Project Number 200451						
Do not scale this drawing. The drawing shows design intent only. All dimensions to be checked on site prior to construction or production. Construction details to be confirmed by contractor/manufacturer. This is a computer generated drawing. Do not amend by hand. Figure dimensions are to be used. Contact architect for clarification if dimensions are not clear. All dimensions are in millimeters. All discrepancies and omissions on site must be reported to the architect for their comments or approval prior to commencing work.																Drawing HEAVY VEHICLE CANOPY ELEVATIONS								
D2 D1						ISSUE FOR DA ISSUE FOR DA		14.04.2021 08.04.2021		DC DC		DC DC												
Issue		Description			Date		Chk		Int						Location M31 HUME HIGHWAY PHEASANTS NEST NSW 2574 - NORTHBOUND		Project Code PNS		Discipline code AR		Drawing Number DA096S		Issue D2	


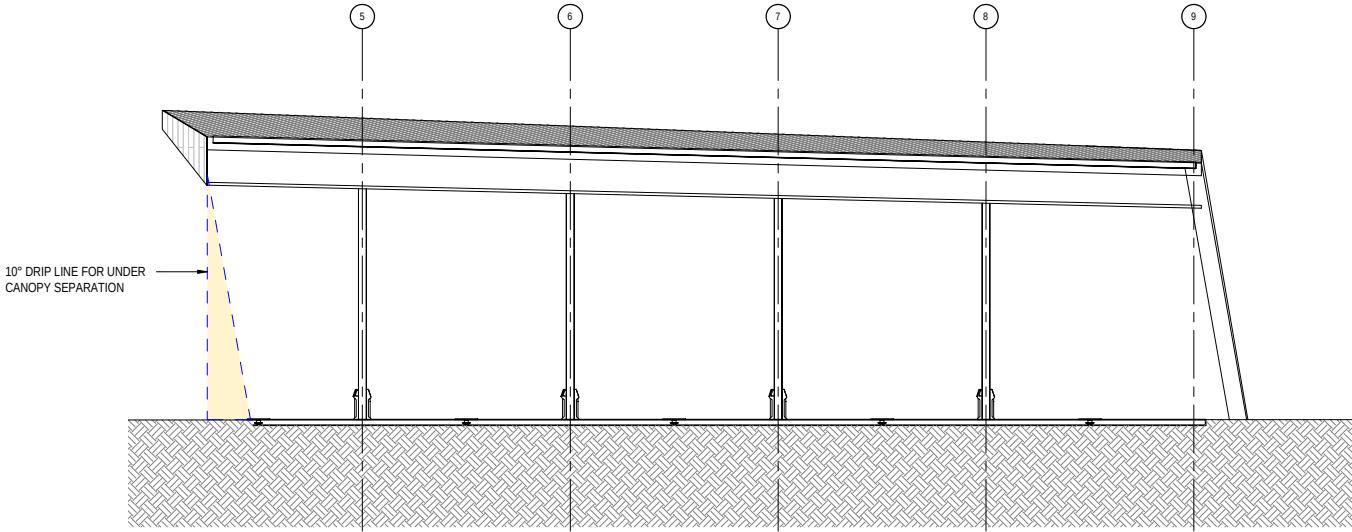



1 TRUCKS CANOPY SECTION 01
1 : 100 @ A1

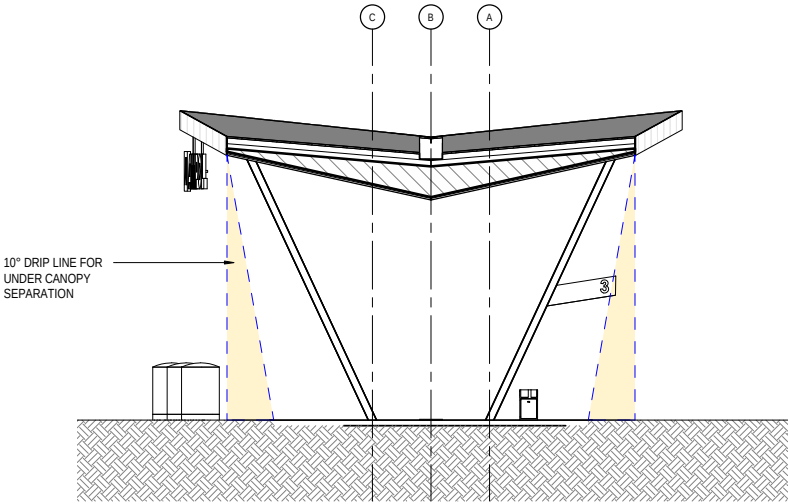

2 PNN-TRUCKS CANOPY SECTION -
1 : 100 @ A1

Revisions				General Notes				Drawing Notes				FOR DA NOT TO BE USED DURING CONSTRUCTION				Client				Project				Scale				Project Number			
D2				ISSUE FOR DA				14.04.2021				DC				DC				REDEVELOPMENT OF HIGHWAY				1 : 100 @ A1				200451			
D1				ISSUE FOR DA				08.04.2021				DC				DC				SERVICE CENTRE PHEASANTS NEST				Drawing							
Issue				Description				Date				Chk				Int				M31 HUME HIGHWAY PHEASANTS NEST				HEAVY VEHICLE CANOPY- SECTIONS							
																				NSW 2574 - NORTHBOUND				Project Code				Issue			
																								PNN				DA097N			
																								AR				D2			

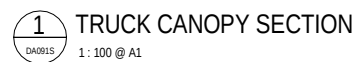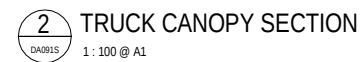

 Revisions					General Notes					Drawing Notes					FOR DA NOT TO BE USED DURING CONSTRUCTION					ABN 34 001 485 436					Client					Project					Scale					Project Number				
D2 ISSUE FOR DA 14.04.2021 DC DC					D1 ISSUE FOR DA 08.04.2021 DC DC					Do not scale this drawing. The drawing shows design intent only. All dimensions to be checked on site prior to construction or production. Construction details to be confirmed by contractor/manufacturer. This is a computer generated drawing. Do not amend by hand. Figure dimensions are to be used. Contact architect for clarification if dimensions are not clear. All dimensions are in millimeters. All discrepancies and omissions on site must be reported to the architect for their comments or approval prior to commencing work.					Richmond+Ross CONSULTING ENGINEERS AND PROJECT LEADERS 38 Willoughby Road Crows Nest NSW 2085 TEL: (02) 9490 9600 FAX: (02) 94381224										REDEVELOPMENT OF HIGHWAY SERVICE CENTRE PHEASANTS NEST (M31) - TRUCK CANOPY Location M31 HUME HIGHWAY PHEASANTS NEST NSW 2574 - NORTHBOUND					1 : 100 @ A1					200451									
																														Drawing					HEAVY VEHICLE CANOPY- SECTIONS									
Issue		Description			Date		Chk		Int		Project Code		Discipline code		Drawing Number		Issue																											
					PNS		AR		DA097S		D2																																	