

1

2

3

4

5

6

7

8

9

10

11

12

GENERAL NOTES:

1. DO NOT SCALE DRAWINGS - WRITTEN DIMENSIONS TAKE PRECEDENT.

2. ALL DIMENSIONS ARE IN MILLIMETRES UNLESS OTHERWISE NOTED.

3. THIS DRAWING MUST BE READ IN CONJUNCTION WITH ALL RELEVANT CONTRACTS, SPECIFICATIONS, SCHEDULES, REPORTS AND DRAWINGS.

4. ALL DIMENSIONS, LEVELS AND EXISTING SERVICES SHALL BE VERIFIED BY CONTRACTOR AND SUB-CONTRACTORS ON SITE PRIOR TO COMMENCEMENT ON SITE, DURING THE PREPARATION OF SHOP DRAWINGS AND FABRICATION OF CONSTRUCTION COMPONENTS. NOTIFY SUPERINTENDENT OF ANY DISCREPANCIES.

5. SETOUT TO BE UNDERTAKEN BY A LICENSED SURVEYOR. CAD FILES WILL BE AVAILABLE ON REQUEST TO THE SUPERINTENDENT.

6. FOR ALL ROAD CONSTRUCTION INFORMATION, PAVEMENTS, JOINTS, KERBING AND ASSOCIATED REINFORCING, SUBGRADE PREPARATION AND ROAD FINISHED LEVELS REFER TO CIVIL DOCUMENTATION.

7. FOR ALL STREET AND FEATURE LIGHTING REFER TO ELECTRICAL ENGINEER'S DOCUMENTATION.

8. FOR ALL IRRIGATION DEMOLITION AND CONSTRUCTION INFORMATION REFER TO IRRIGATION DOCUMENTATION AND SPECIFICATION.

9. FOR ALL CONCRETE COMPRESSIVE STRENGTH DETAILS REFER SPECIFICATION.

DEMOLITION:

10. ALL EXISTING TREES, THAT ARE DESIGNATED TO BE RETAINED, MUST BE FULLY PROTECTED WITH TREE PROTECTION FENCING ERECTED BEYOND THE DRIP LINE. FENCING MUST REMAIN IN PLACE FOR THE FULL DURATION OF ALL CONSTRUCTION ACTIVITIES IN ACCORDANCE WITH AS 4970--2009 PROTECTION OF TREES ON DEVELOPMENT SITES.

11. REMOVE ALL DEMOLISHED MATERIALS FROM SITE. DISPOSAL BY BURNING AND/OR BURYING PROHIBITED.

12. THE LOCATION OF EXISTING SERVICES MAY VARY FROM THE DRAWINGS. CONFIRM ALL EXISTING SERVICE LOCATIONS PRIOR TO COMMENCING DEMOLITION.

GRADING:

13. REFER TO CIVIL ENGINEER DOCUMENTATION FOR GRADING AND EARTHWORKS

14. REFER TO DETAILS FOR IMPORTED SUB-BASE SOIL PROFILE REQUIREMENTS

15. GRADE AREAS THROUGHOUT TO TRUE AND EVEN GRADES AND FALLS TO THE CONTOURS INDICATED ON THE DRAWINGS. FINISH GRADES FLUSH WITH ADJOINING PAVEMENTS AND KERBS EXCEPT WHERE OTHERWISE INDICATED ON THE DRAWINGS.

16. GRADE TO PROVIDE EVEN FALLS SO THAT THE SURFACE IS CONSTANTLY SELF-DRAINING. NO IRREGULARITIES, DEPRESSIONS OR ABRUPT CHANGES IN GRADES OR FALLS WILL BE ACCEPTED.

PIT LIDS:

17. THE FINAL LOCATION AND ORIENTATION OF PIT LIDS TO BE CONFIRMED BY SUPER INTENDANT PRIOR TO INSTALLATION.

18. ALL PIT LIDS TO BE SET SQUARE TO LANDSCAPE GEOMETRY AND ELEMENTS.

19. REFER TO LANDSCAPE FINISHES PLANS & LANDSCAPE MATERIAL SCHEDULE FOR SURFACE TYPES TO INFILL TO PIT LIDS.

20. PIT LID DETAILS ARE PROVIDED TO SHOW LID INFILL AND EDGE SURROUND REQUIREMENTS ONLY. REFER TO SERVICES ENGINEERS AND CIVIL ENGINEER'S DOCUMENTATION FOR PIT DIMENSIONS AND FURTHER REQUIREMENTS.

21. ALL PITS LOCATED IN PAVEMENTS TO HAVE INFILL COVER. INFILL TO MATCH ADJOINING PAVEMENT.

22. ALL PIT LIDS IN GARDEN BEDS SHALL HAVE DUCTILE IRON LIDS. ALL CONCRETE SURROUNDS SHALL BE SUBSURFACE AND CONCEALED BELOW GARDEN MULCH LEVEL.

23. ALL PIT LIDS SHALL BE INSTALLED TO MEET FINISHED LEVELS AND CROSS-FALLS, REFER TO CIVIL ENGINEER'S DESIGN.

24. REFER TO CIVIL, ELECTRICAL AND MECHANICAL ENGINEER'S DOCUMENTATION FOR PIT LID REQUIREMENTS IN ROAD WAYS.

25. SEWER PIT LIDS TO COMPLY WITH WATER CORPORATION REQUIREMENTS. REFER TO CIVIL DESIGN

26. PIT LID CONCRETE INFILL SUBSTRATE TO BE LIGHTWEIGHT CONCRETE.

27. IT IS THE RESPONSIBILITY OF THE HEAD CONTRACTOR TO ENSURE THAT PIT LID INFILL REQUIREMENTS ARE ACHIEVED WITH A CONSISTENCY OF FINISH ACROSS THE ENTIRE PROJECT.

WALLS:

28. ALL FORMWORK TO BE DESIGNED TO CARRY LOADS TO AVOID BOWING, BUILDING, SAG OR OTHER DISTORTIONS.

29. TOPS OF WALLS TO SLOPE DOWN TOWARDS SOFT SURFACES TO AVOID WATER POOLING.

30. TIE ROD HOLES TO BE SET OUT TO ACHIEVE A UNIFORM PATTERN APPEARANCE.

31. WHERE CONTROL JOINTS HAVE NOT BEEN NOMINATED JOINTS TO BE EVENLY SPACED AT SPECIFIED INTERVALS.

32. ENSURE CONSISTENT ORIENTATION AND SPACING OF FORMWORK TO ACHIEVE UNIFORM FINISH.

33. WALLS TO BE PROTECTED FOR THE DURATION OF THE WORKS.

34. DAMAGED WALL SURFACES TO BE MADE GOOD. METHOD TO BE AGREED WITH THE SUPER INTENDANT PRIOR TO APPLICATION.

SURFACE FINISHES:

35. CONTRACTOR TO SET OUT ALL HARD LANDSCAPE ELEMENTS AND VERIFY WITH SUPERINTENDENT PRIOR TO CONSTRUCTION. ANY DISCREPANCIES OR CONFLICTS WITH EXISTING CONDITIONS TO BE REPORTED IMMEDIATELY.

36. CONTRACTOR TO INSTALL EXPANSION JOINTS AS DOCUMENTED WHERE PAVEMENT MEETS VERTICAL STRUCTURES SUCH AS WALLS, KERBS, STEPS, FURNITURE, LIGHTING AND BUILDING ELEMENTS WHERE NOT DOCUMENTED.

37. ALL UNRESTRAINED PAVING EDGES TO HAVE CONCEALED CONCRETE HAUNCH AS DOCUMENTED

38. CLOSURE RULE: WHEREVER THE END OF A PAVING RUN WOULD RESULT IN A PAVERS LESS THAN 1/3 FULL SIZE, CUT 2 PAVERS IN EQUAL LENGTHS TO CLOSE OUT THE RUN.

39. ALL PEDESTRIAN TRAFFICABLE SURFACES ARE TO COMPLY WITH AS1428.1 FOR VERTICAL TOLERANCES.

40. ALL PAVEMENT TO COMPLY WITH AS/NZS 4586 & 4663 FOR SLIP RESISTANCE AND MEET "W" AND "R10" CLASSIFICATIONS FOR PEDESTRIAN SURFACES.

41. WHERE SERVICE RUNS ARE REQUIRED THROUGH EXISTING HARD AND SOFT LANDSCAPE, FINISHES ARE TO BE MADE GOOD AT COMPLETION OF WORKS TO MATCH EXISTING.

42. SUB BASE - REFER TO CIVIL ENGINEER FOR SUB BASE DETAILS.

43. KERBING - REFER TO CIVIL DRAWINGS AND SPECS FOR ALL KERBING DETAILS

44. ASPHALT- REFER TO CIVIL DRAWINGS AND SPECS FOR TYPICAL DETAILS AND SUB-BASE PROFILE

FURNITURE:

45. ENSURE THAT ALL FURNITURE IS STABLE, SAFE, CLEAN AND FIT FOR USE.

46. ALL FURNITURE SHALL BE INSTALLED PLUMB AND LEVEL UNLESS SPECIFIED OTHERWISE.

47. ALL FIXINGS, CONDUITS AND FOUNDATIONS TO BE CONCEALED AND VANDAL RESISTANT.

48. FURNITURE TO BE MANUFACTURED IN ACCORDANCE WITH CURRENT AUSTRALIAN STANDARDS TO WHICH STREET FURNITURE MANUFACTURING MUST COMPLY.

49. THE CONTRACTOR MUST ENSURE THAT ALL ITEMS OF FURNITURE ARE PROTECTED FROM DAMAGE DURING HANDLING, TRANSPORTATION, INSTALLATION AND FOR THE DURATION OF THE WORKS.

51. 5MM SPACING BETWEEN TIMBER BOARDS IN ALL DIRECTIONS UNLESS NOTED OTHERWISE.

52. FULL SHOP DRAWINGS ARE TO BE PROVIDED FOR CUSTOM FURNITURE FOR APPROVAL BY SUPERINTENDENT AND STRUCTURAL CIVIL ENGINEER BEFORE MANUFACTURE AND INSTALLATION OF ELEMENTS.

53. SHOP DRAWINGS TO INCLUDE A 3D DIGITAL MODEL SHOWING ALL MATERIAL INTERFACES, JOINTS, JUNCTIONS AND TIMBER SIZES.

54. SHOP DRAWINGS TO INDICATE LOCATION OF WELDED JOINS. WELDED JOINTS TO BE FABRICATED WITH LASER CUT SEAMS, FULLY WELDED AND GROUND BACK TO SMOOTH.

55. WHERE FIXINGS TYPES OR STRUCTURAL SPACINGS HAVE NOT BEEN NOMINATED CONTRACTOR TO ENSURE THAT AN ENGINEER HAS APPROVED ANY SIZINGS AND SPACINGS INSTALLED.

56. CONTRACTOR TO SUPPLY AND INSTALL ALL SCREWS, BOLTS, NUTS, WASHERS, HINGES, LOCKS AND FIXINGS REQUIRED.

52. ALL DIMENSIONS, EXISTING LEVELS AND EXISTING SERVICES SHALL BE VERIFIED BY CONTRACTOR AND SUB-CONTRACTORS ON SITE PRIOR TO THE PREPARATION OF SHOP DRAWINGS AND FABRICATION OF FURNITURE TO ENSURE FURNITURE ELEMENTS ARE COORDINATED WITH AS CONSTRUCTED FINISHES.

53. ALL HARDWOOD TIMBER TO BE SUPPLIED AND INSTALLED AS DURABLE CLASS 1 UNLESS OTHERWISE STATED IN THE SPECIFICATION.

54. ALL TIMBER CONNECTIONS TO BE MITRE JOINTS UNLESS OTHERWISE SPECIFIED.

PLANTING:

55. REFER TO PLANTING SCHEDULE FOR SPECIES

56. EXACT LOCATIONS OF PLANT MATERIALS SHALL BE REVIEWED BY THE SUPERINTENDENT PRIOR TO INSTALLATION. THE SUPERINTENDENT RESERVES THE RIGHT TO ADJUST PLANTS TO EXACT LOCATIONS IN THE FIELD.

57. CONTRACTOR TO ENSURE ALL TREES TO BE PLANTED 1M FROM KERB OR FOOTPATH AND 1.5M FROM CROSS OVER.

58. LANDSCAPE CONTRACTOR IS TO PEG ALL TREE LOCATIONS TO THE SUPERINTENDENT'S APPROVAL PRIOR TO INSTALLATION.

59. PROVIDE MATCHING FORMS AND SIZES FOR PLANT MATERIAL WITHIN EACH SPECIES AND SIZE NOMINATED.

60. FINISHED SURFACE LEVEL OF PLANTING AREAS TO BE SET 50MM BELOW PAVING OR TOP OF WALL LEVELS UNLESS NOTED OTHERWISE.

61. SUPERINTENDENT TO REVIEW ALL PLANT MATERIALS AT SOURCE OR BY PHOTOGRAPH PRIOR TO DIGGING AND DELIVERY TO SITE.

62. PRIOR TO INSTALLATION OF PLANTING AND IRRIGATION CONTRACTOR TO PREPARE SOIL AS SPECIFIED.

63. TOPSOIL SHALL BE UNIFORMLY GRADED TO EVEN-RUNNING CONTOURS, SO THAT NO PONDING OR WATERLOGGING OCCURS ACROSS THE SURFACE OF THE GRASSED AREA AND RAKED BEFORE TURF IS LAID.

64. TURF SHALL BE LAID IN STRAIGHT LINES WITH STAGGERED CROSS JOINTS ON THE GENERAL LINE OF THE CONTOUR OF THE SLOPE. THE GAPS BETWEEN ADJACENT SECTIONS OF TURF SHOULD NOT EXCEED 5MM.

65. ACCEPTANCE SHALL BE THE ACHIEVEMENT OF AN EVEN GREEN COLOUR WITH A DENSE CONTINUOUS SWARD OVER THE WHOLE AREA. TURF SHALL EXHIBIT SIGNS OF HEALTHY GROWTH AND SHALL BE FREE OF WEEDS, STONES, STICKS AND OTHER DELETERIOUS MATERIAL. MAXIMUM DEVIATION FROM FINISHED GROUND LEVELS 50MM IN ANY 2 METRES.

EXISTING TREES:

66. NO CONSTRUCTION EQUIPMENT OR MOTORISED VEHICLES ARE PERMITTED WITHIN THE TREE PROTECTION ZONE AND ALL TREE PROTECTION ZONES MUST REMAIN UNDISTURBED AT ALL TIMES AS PER AUSTRALIAN STANDARD AS4970.

67. ANY BACKFILLING OR TOPSOIL STORAGE OF MATERIALS MUST REMAIN OUTSIDE THE LIMITS OF THE TREE PROTECTION ZONE.

68. ANY ROOTS OR BRANCHES THAT EXTEND BEYOND THE TREE PROTECTION ZONE, WHICH REQUIRE PRUNING, MUST BE PRUNED BY A QUALIFIED ARBORIST IN ACCORDANCE WITH GOOD ARBORICULTURE PRACTICES.

69. ALL EXISTING TREES, THAT ARE DESIGNATED TO BE RETAINED, MUST BE FULLY PROTECTED WITH TREE PROTECTION FENCING ERECTED BEYOND THE DRIP LINE. FENCING MUST REMAIN IN PLACE FOR THE FULL DURATION OF ALL CONSTRUCTION ACTIVITIES IN ACCORDANCE WITH AS 4970--2009 PROTECTION OF TREES ON DEVELOPMENT SITES

70. THE CONTRACTOR TO ALLOW FOR ALL WATERING SYSTEMS DURING CONSTRUCTION WORK TEMPORARY AND FIXED SYSTEMS OF ALL MATURE TREES AND HAND WATERING FOR THE DURATION OF ANY FAILURE TO THE WATERING SYSTEM.

71. CONTRACTOR TO ALLOW FOR COORDINATION OF THE WORK WITH ARBOR CENTRE AND TRAFFIC MANAGEMENT IF REQUIRED

72. CONTRACTOR SHALL ENSURE THAT IRRIGATION WATERING TO THE TRANSPLANT TREES IS AVAILABLE ON INSTALLATION OF TREES.

73. CONTRACTOR SHALL LIAISE WITH ARBORCULTURIST TO ENSURE THAT PLANTING HOLES AND IN-GROUND GUYING DON'T CONFLICT WITH PROPOSED SERVICES.

74. GUYING SPECIFIED ARE TO COMPLY WITH THE AUSTRALIAN LOADING CODE FOR WINDS APPLICABLE TO PERTH AS 1170.2:2014 SUPPLY BY ARBOR CENTRE

75. CONTRACTOR SHALL ENSURE CARE IS TAKEN WHEN INSTALLING FINISHES AROUND TREES TO AVOID COMPACTION CONTAMINATION OF TREE PIT.

williamdangar +

PLACE LABORATORY

Level 1, 289 Murray Street, Perth
Western Australia, Australia, 6000
T +61 8 9227 9313
M +61 402 706 162
E: ourplace@placelaboratory.com
W: www.placelaboratory.com

CLIENT

MINDEROO FOUNDATION

PO BOX 3155 BROADWAY,
NEDLANDS, WA 6009

DRN BY

D.CLANCY

START DATE

AUGUST 2017

DESIGNED

W.DANGAR

CHECKED

PERSON

GENERAL NOTES

REFER DRAWING L-001 FOR GENERAL NOTES

PLACE LAB

PROJ No

1659

SCALE:

AS SHOWN

DWG STATUS

FOR INFORMATION

DWG No


1659-L-001

DWG SIZE

A1

ISSUE

A

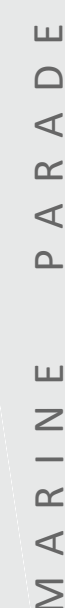

P:\1659 cottlesloe beach house\04 drawings & reports\A-Site\CAD\ Sheets\1659-L-400 Lower Ground Floor.dwg - Fri Sep 08 2017 - 12:45pm m

CLIENT

MINDEROO FOUNDATION

PO BOX 3155 BROADWAY,
NEDLANDS, WA 6009




REV	DATE	REVISION	DRN	CHK
-----	------	----------	-----	-----

DRN BY	D.CLANCY
START DATE	AUGUST 2017
DESIGNED	W.DANGAR
CHECKED	PERSON

COTTESLOE BEACH HOUSE
1 ROSENDO ST, COTTESLOE WA 6011
LOWER GROUND FLOOR

PLACE LAB PROJ No 1659	SCALE: AS SHOWN UNIT: mm
DWG STATUS FOR INFORMATION	SHEET SIZE A1
DWG No 1659-L-400	ISSUE A



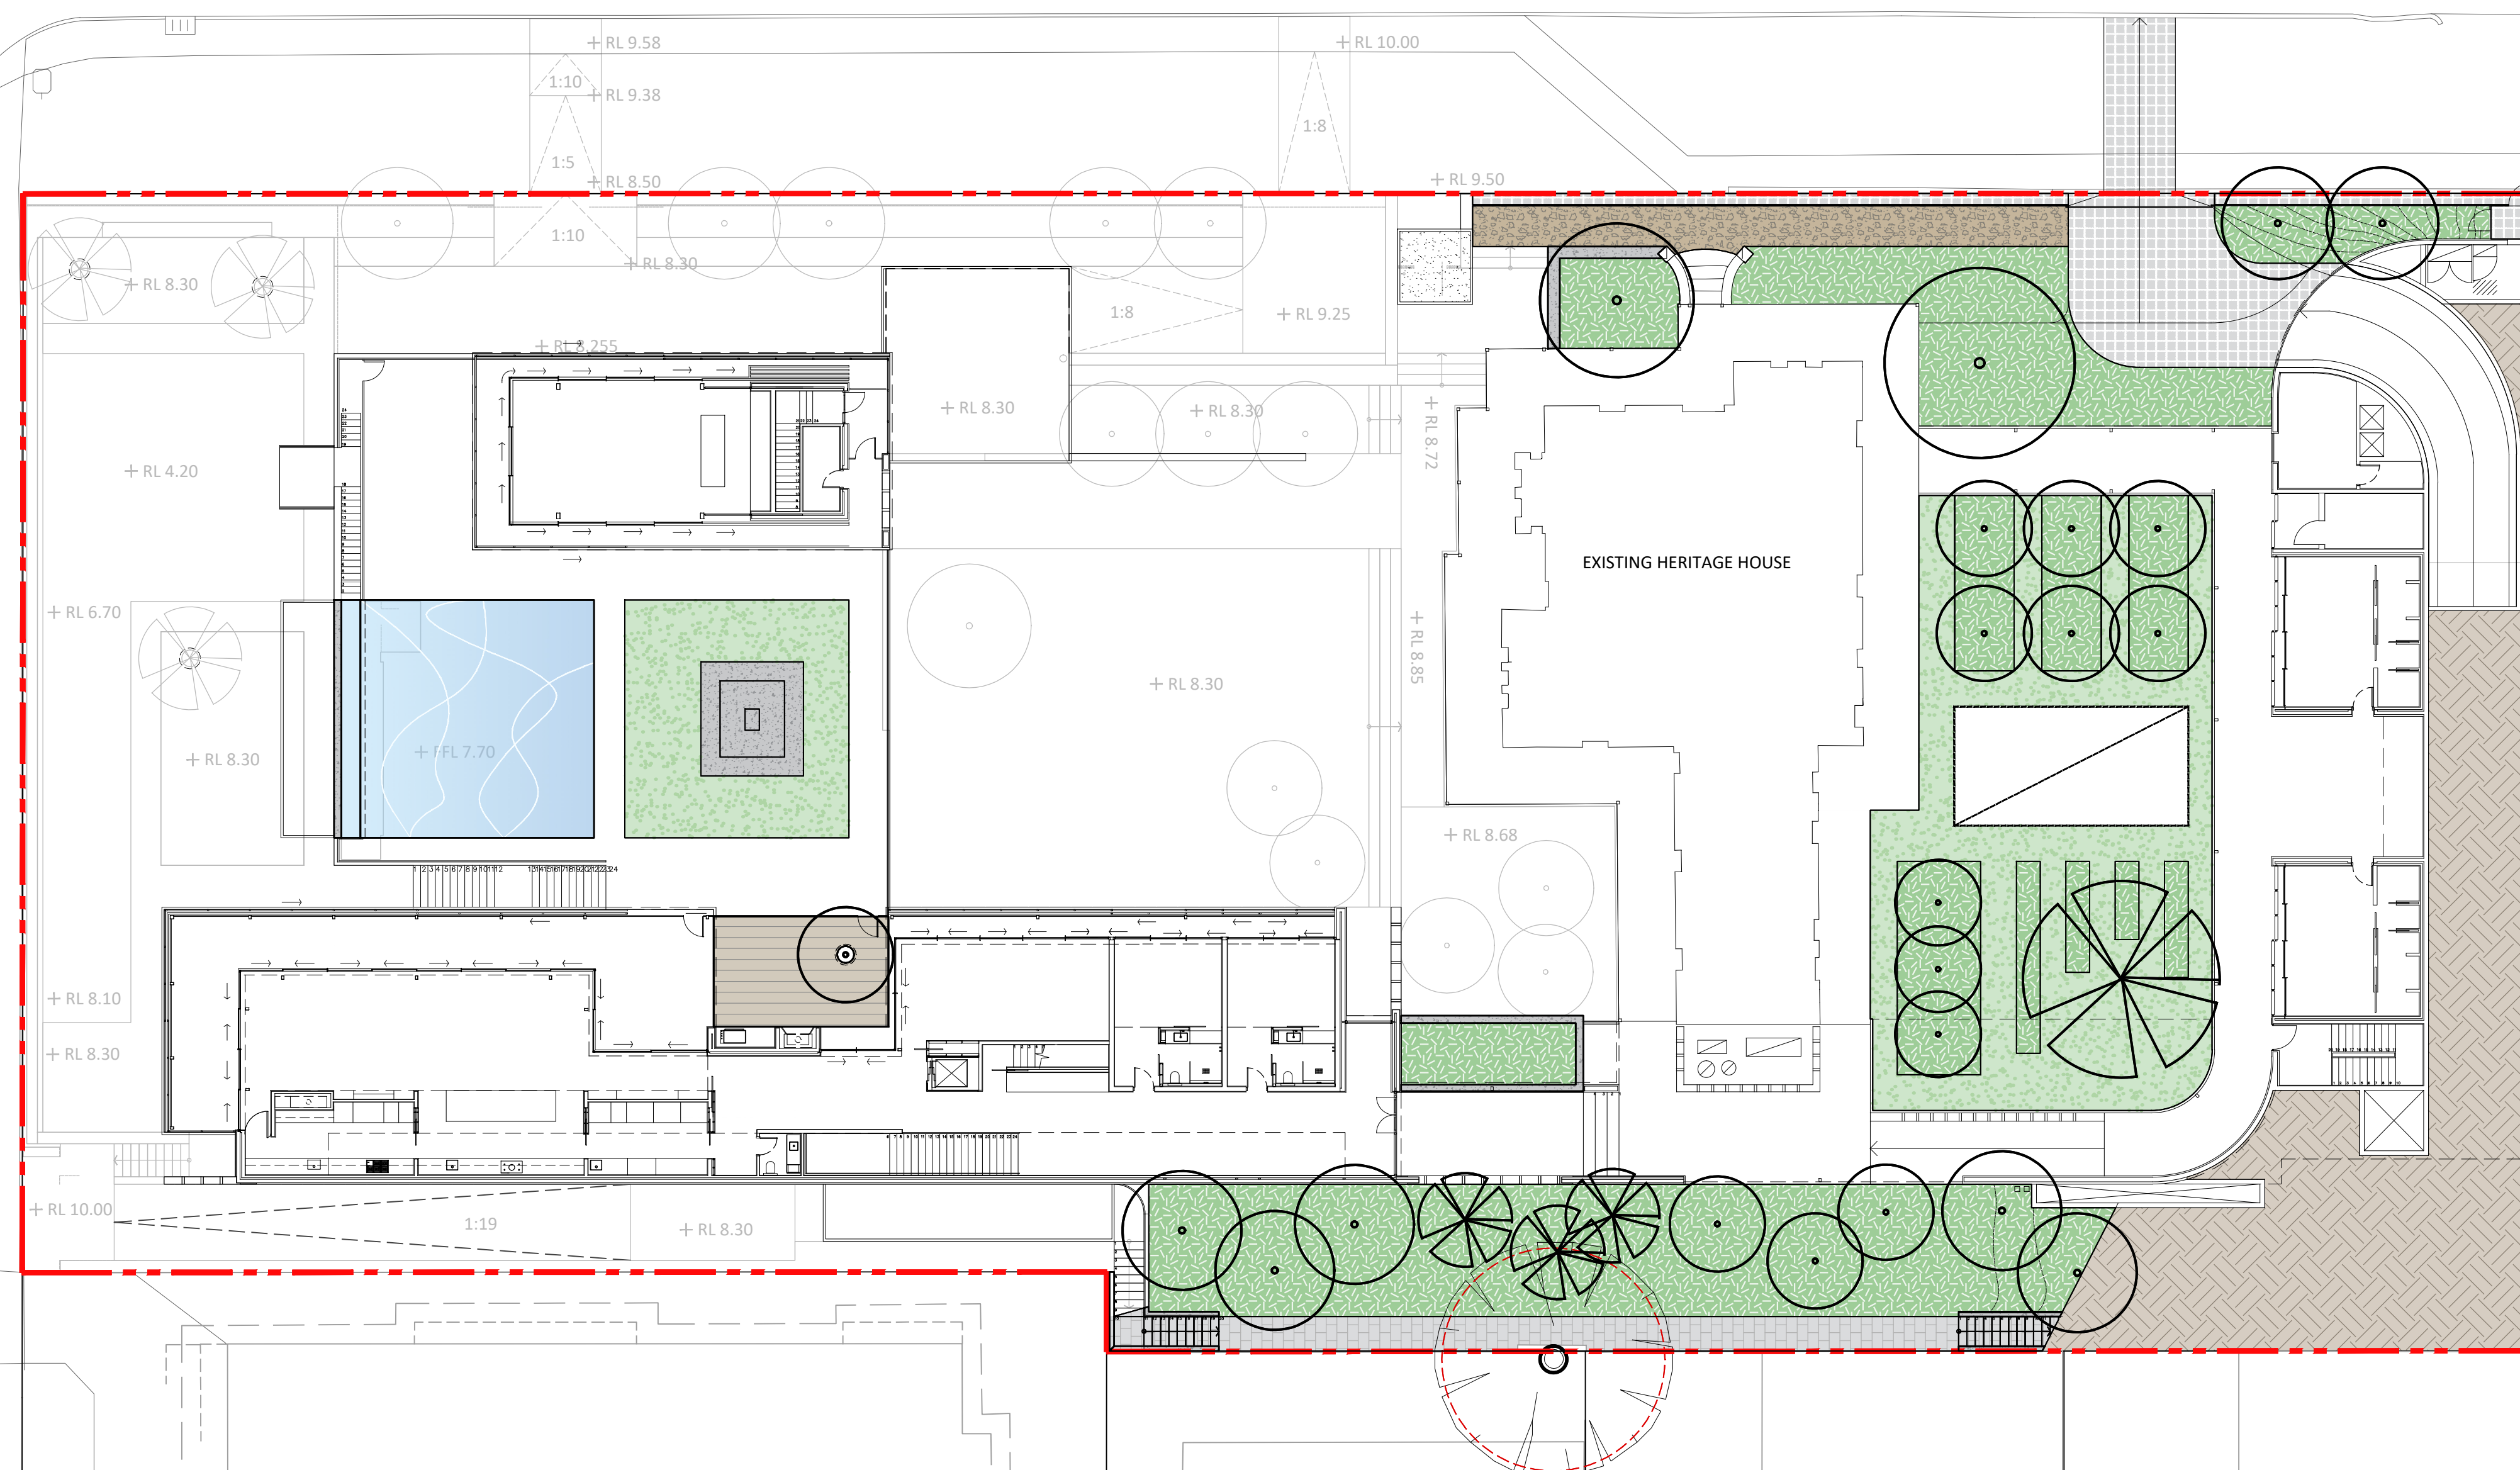


COTTESLOE BEACH HOUSE

1 ROSENDO ST, COTTESLOE WA 6011

GROUND FLOOR



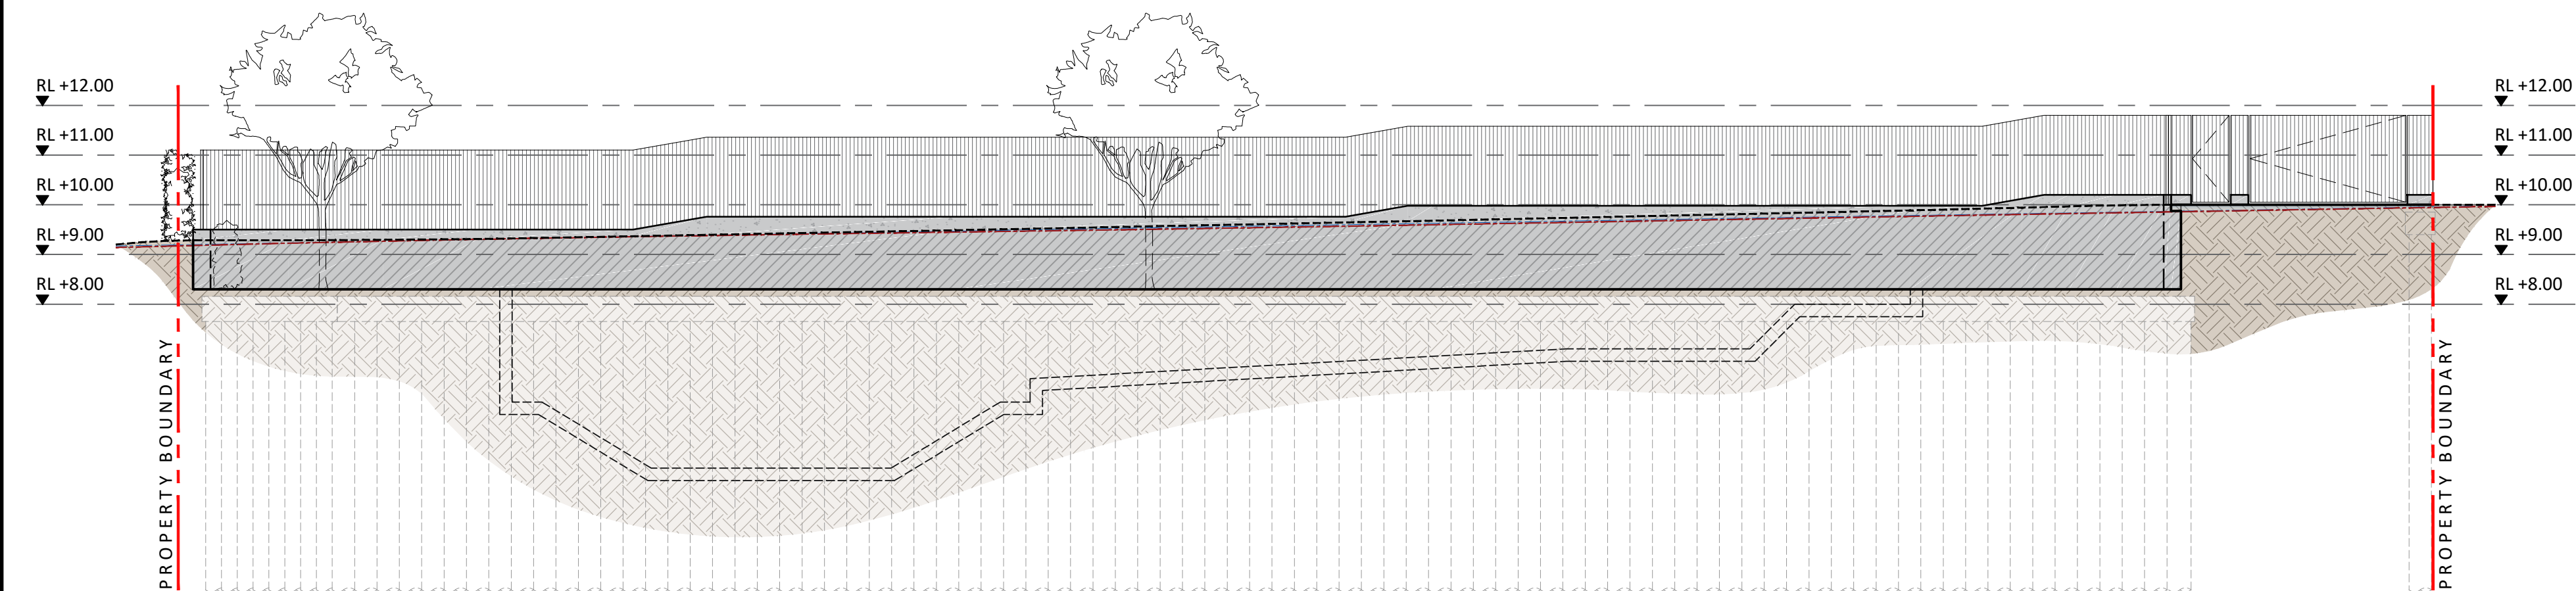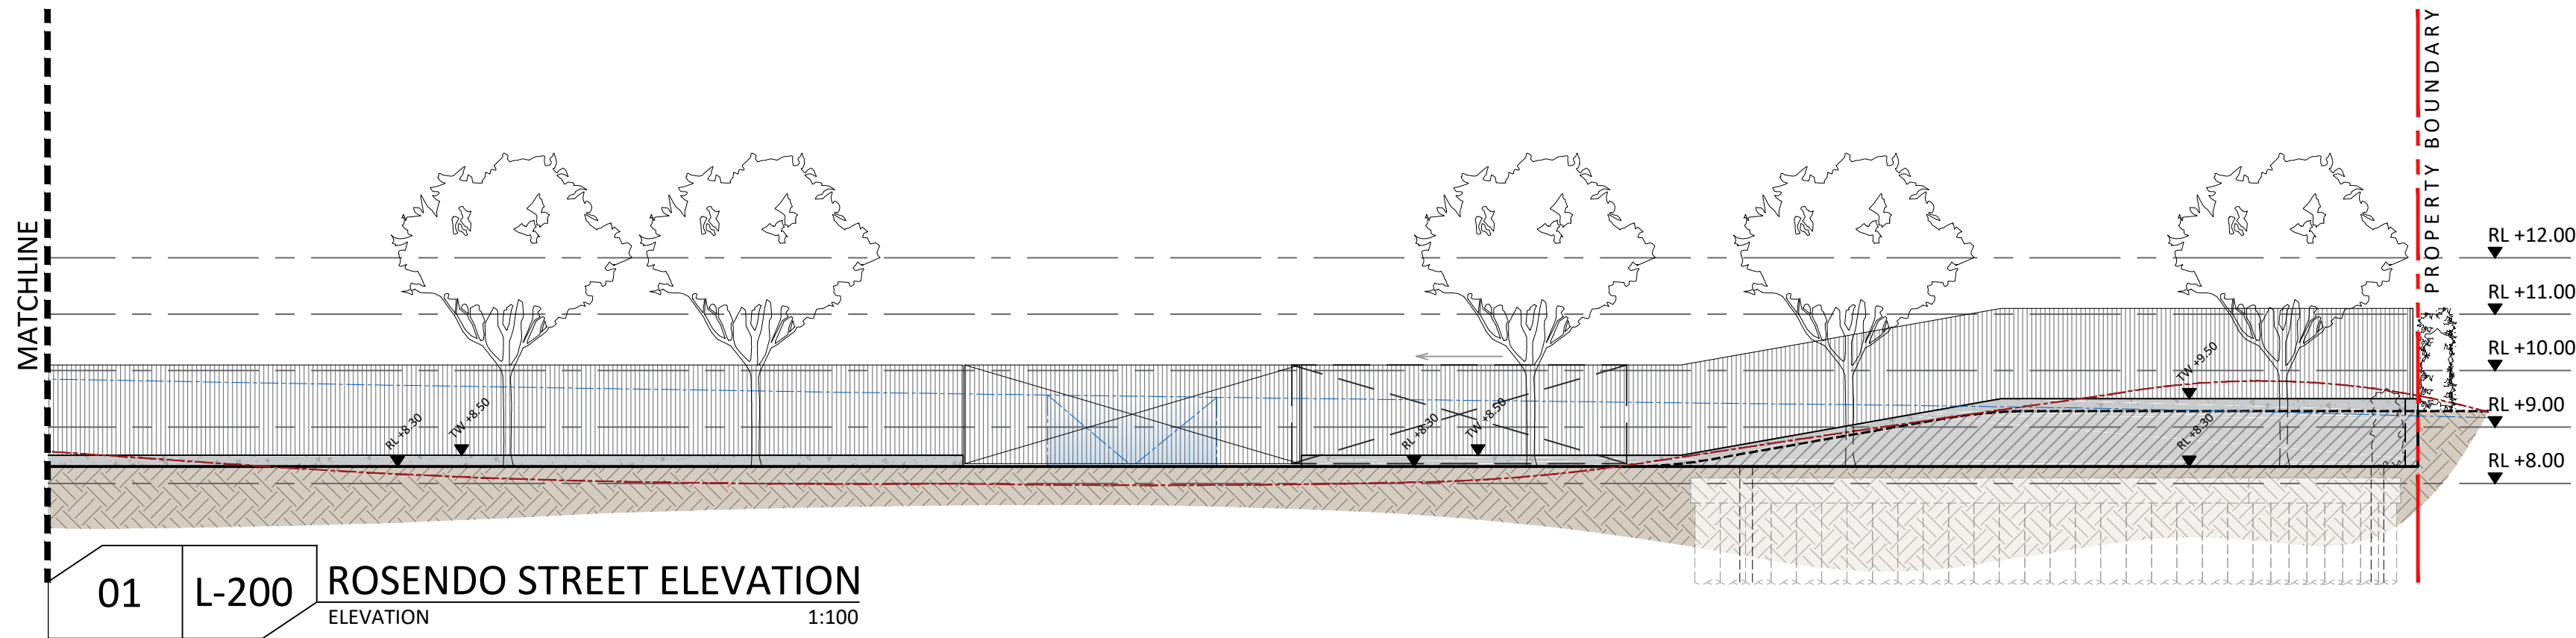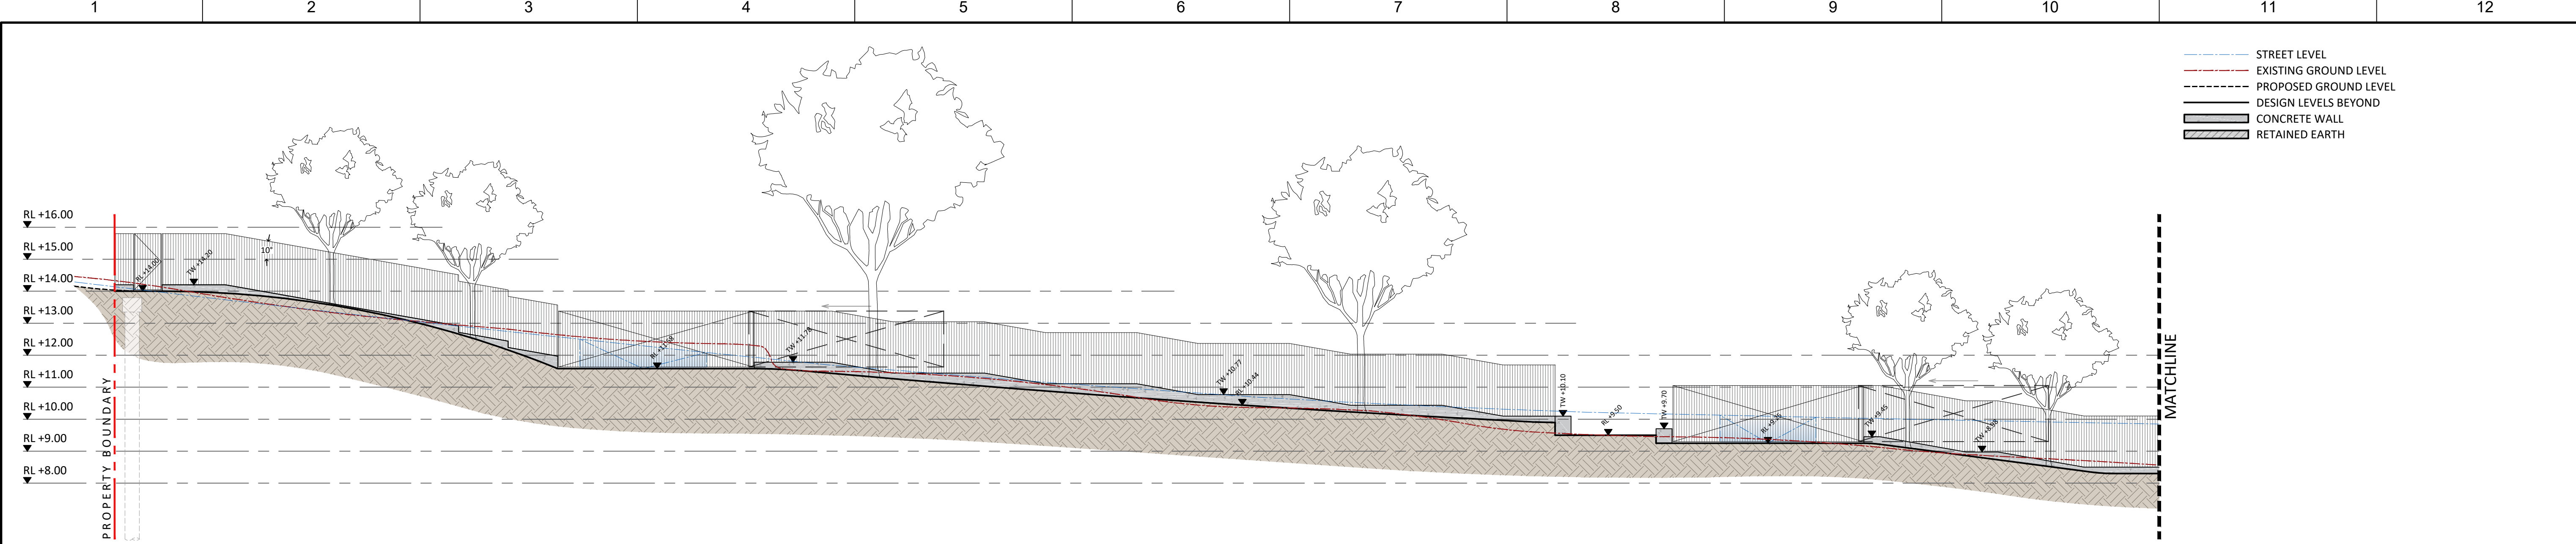

01 L-200 ROSENDO STREET ELEVATION
ELEVATION 1:100

02 L-200 MARINE PARADE ELEVATION
ELEVATION 1:100

williamdangar +

PLACE
LABORATORY

Level 1, 289 Murray Street, Perth
Western Australia, Australia, 6000
T +61 8 9227 9313
M +61 402 706 162
E: ourplace@placelaboratory.com
W: www.placelaboratory.com

CLIENT

MINDEROO FOUNDATION
PO BOX 3155 BROADWAY,
NEDLANDS, WA 6009

NORTH

REV	DATE	REVISION	DRN	CHK

DRN BY
START DATE
DESIGNED
CHECKED

D.CLANCY
AUGUST 2017
W.DANGAR
PERSON

GENERAL NOTES
REFER DRAWING L-001 FOR
GENERAL NOTES

PLACE LAB
PROJ No
DWG
STATUS

1659

1659-L-800




SCALE: AS SHOWN
UNIT: mm
SHEET
SIZE

A1

ISSUE

COTTESLOE BEACH HOUSE
1 ROSENDO ST, COTTESLOE WA 6011
SECTIONS & ELEVATIONS

P:\1659 Cottesloe Beach House\04 Drawings & Reports\A-Site\CAD\ Sheets\1659-L-800 Sections & Elevations.dwg - Thu Sep 07 2017 - 4:42pm daniel

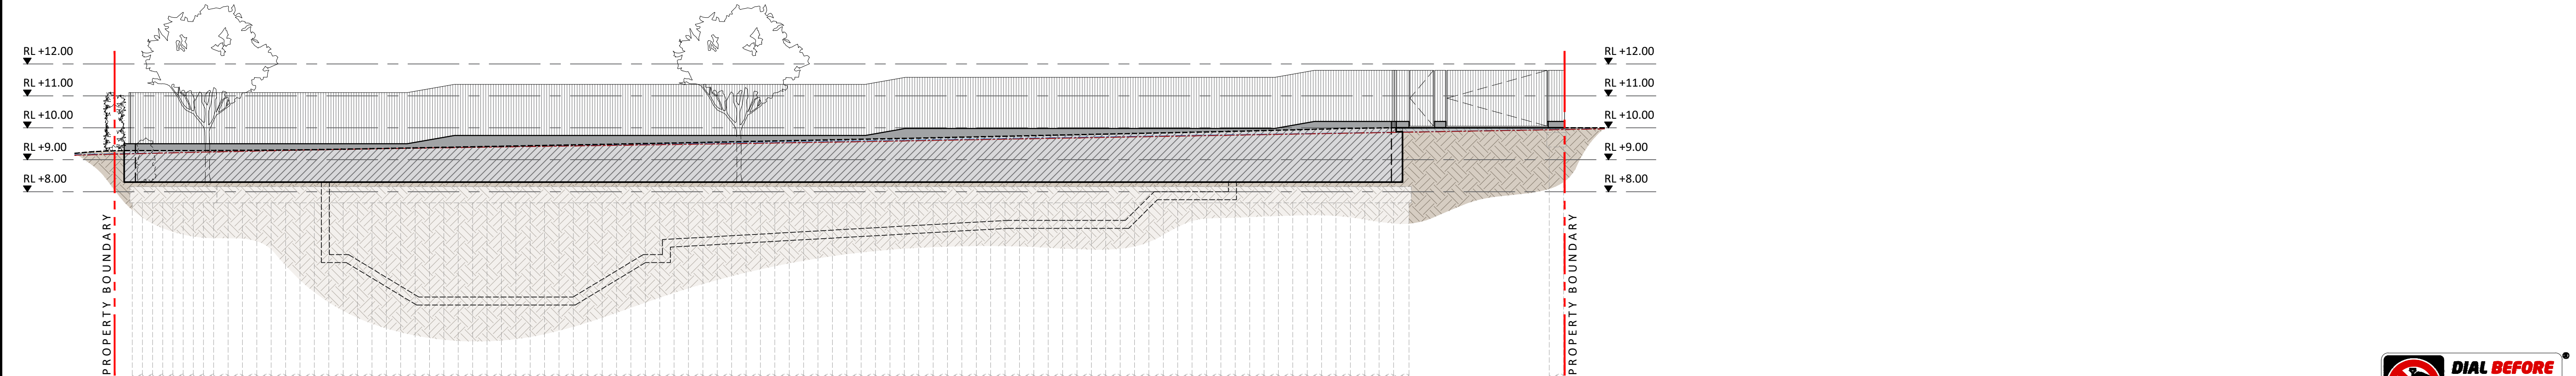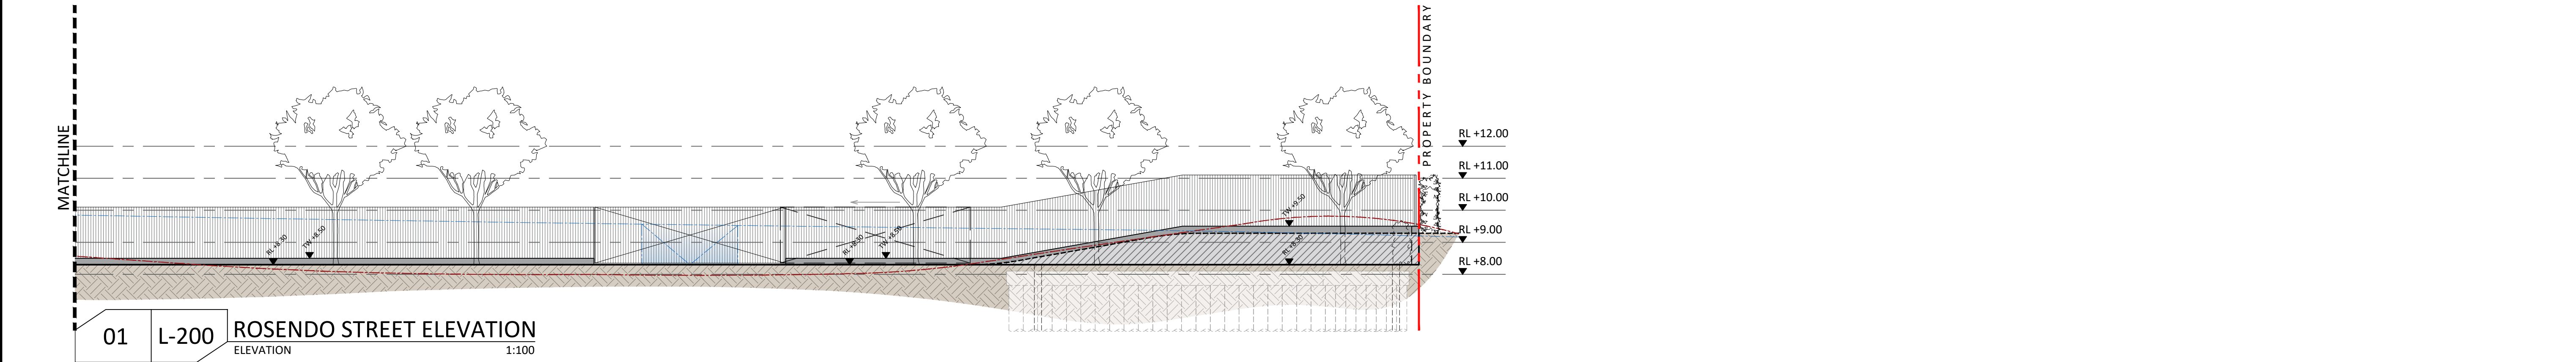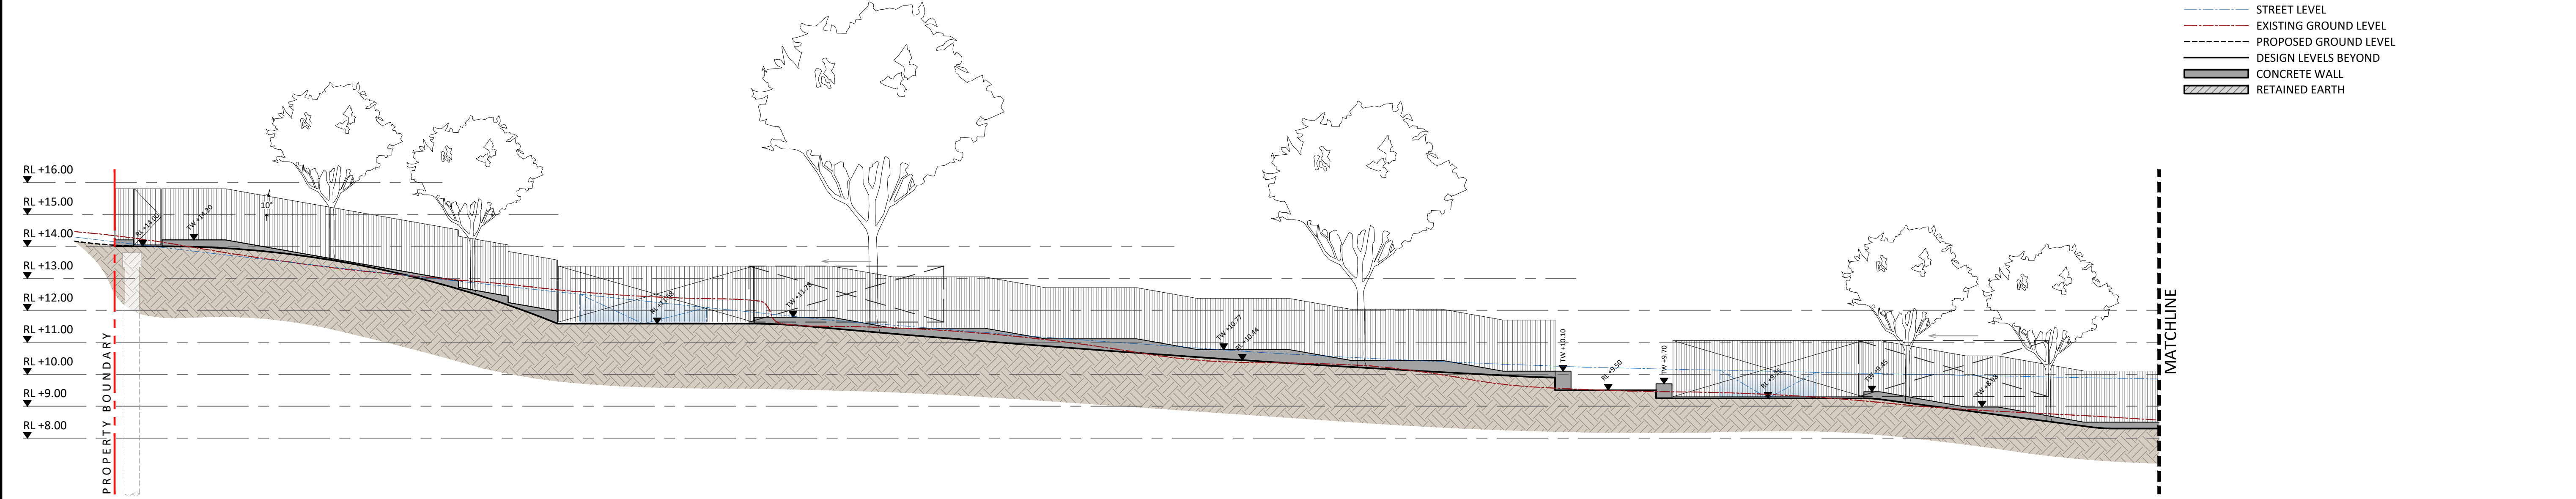

williamdangar +

PLACE LABORATORY

Level 1, 289 Murray Street, Perth
Western Australia, Australia, 6000
T +61 8 9227 9313
M +61 402 706 162
E: ourplace@placelaboratory.com
W: www.placelaboratory.com

CLIENT

MINDEROO FOUNDATION

PO BOX 3155 BROADWAY,
NEDLANDS, WA 6009

NORTH

REV	DATE	REVISION	DRN	CHK

DRN BY

D.CLANCY

START DATE

AUGUST 2017

DESIGNED

W.DANGAR

CHECKED

PERSON

GENERAL NOTES

REFER DRAWING L-001 FOR
GENERAL NOTES

COTTESLOE BEACH HOUSE

1 ROSENDO ST, COTTESLOE WA 6011

SECTIONS & ELEVATIONS

PLACE LAB

PROJ No

1659

SCALE:

AS SHOWN

UNIT:

mm

DWG

STATUS

SHEET

SIZE


A1

ISSUE


DWG No

1659-L-800


P:\1659 Cottesloe Beach House\04 Drawings & Reports\A-Site\CAD\ Sheets\1659-L-800 Sections & Elevations.dwg - Thu Sep 07 2017 - 4:48pm daniel

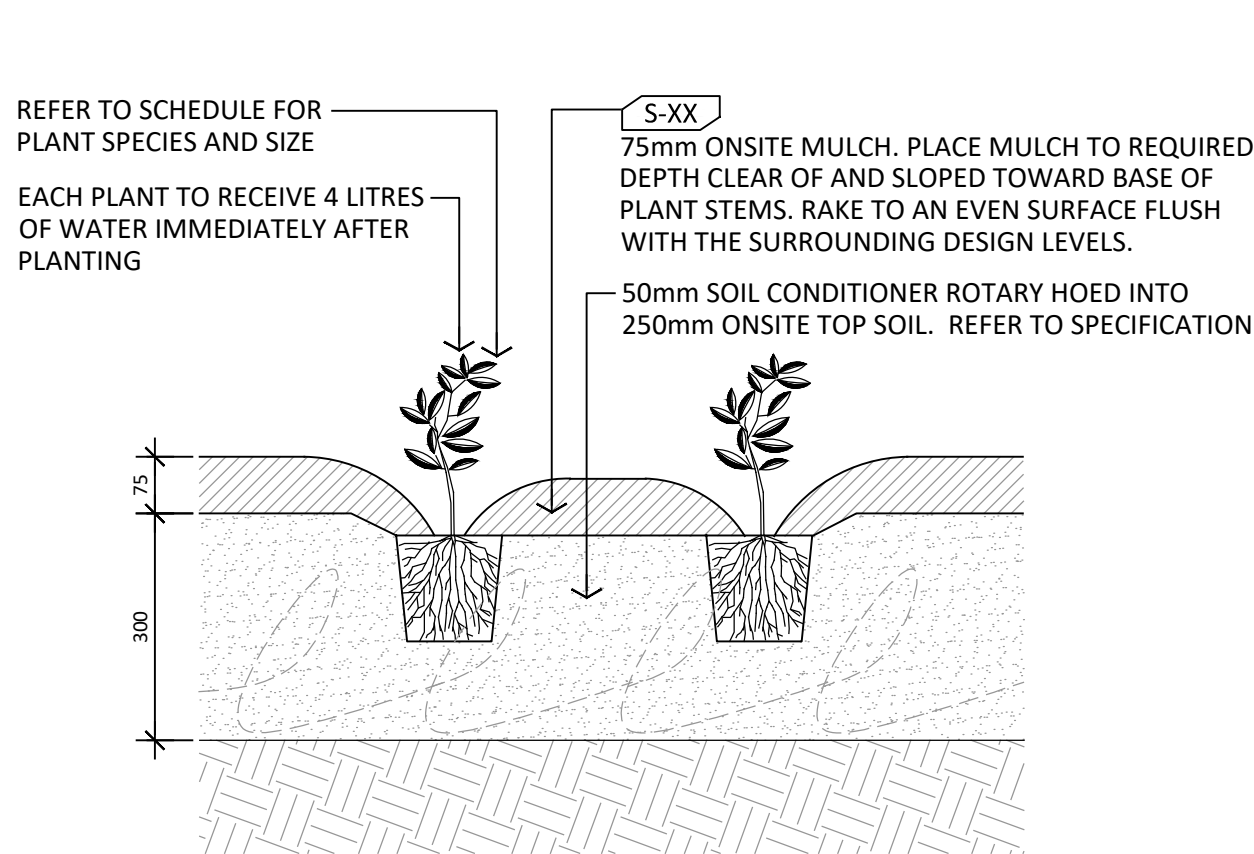


GARDEN BED - GROUND TYP.
SECTION DETAIL 1:10

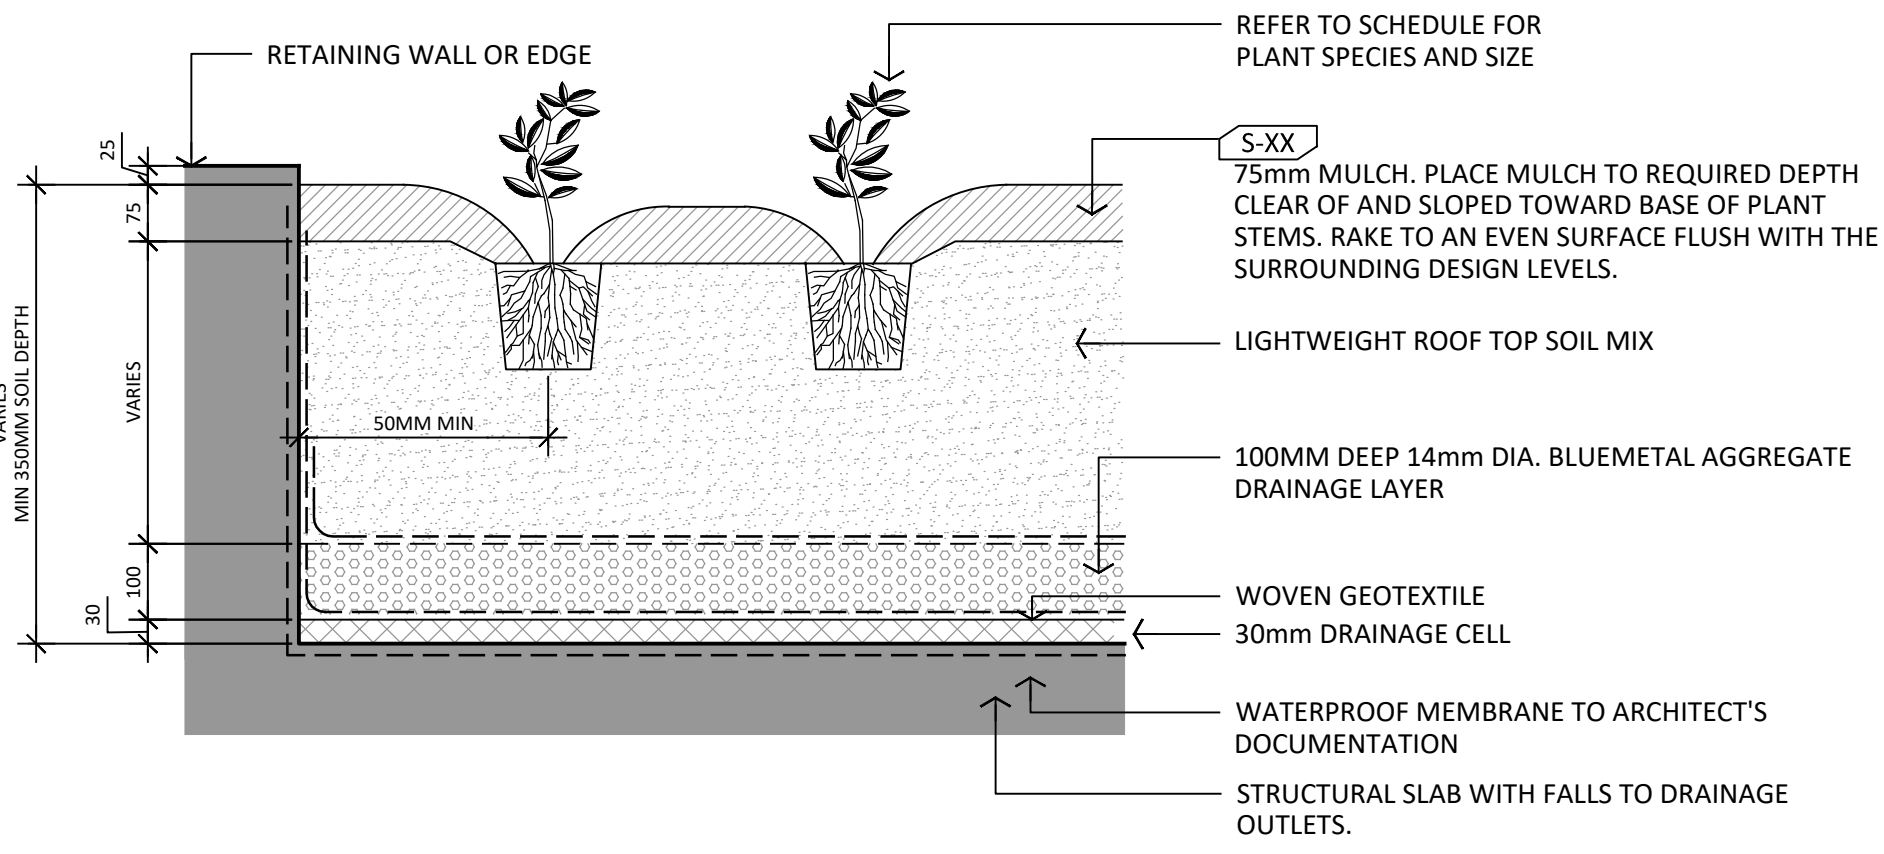

GARDEN BED - SLAB (INTENSIVE) TYP.
SECTION DETAIL 1:10

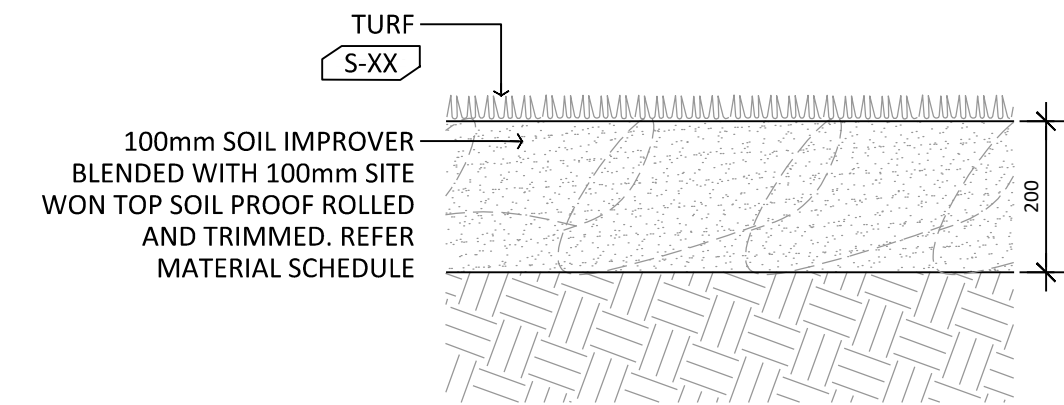


TURF - GROUND TYP. (SECTION)
SECTION DETAIL 1:10

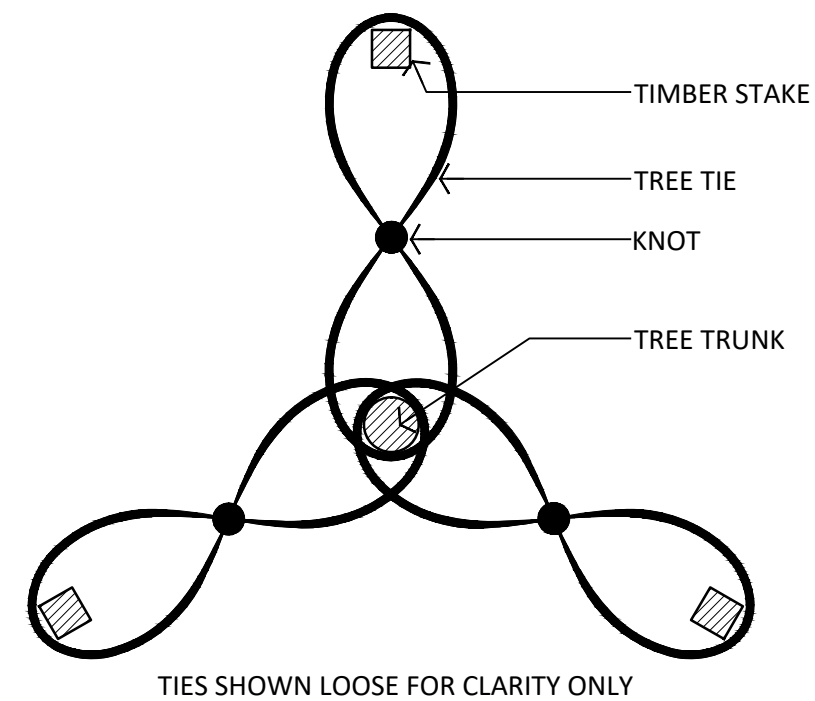


TREE STAKE & TIE TYP.
SECTION DETAIL 1:10


TREE - NURSERY STOCK SIZES (INDICATIVE ONLY)				
POT SIZE	ROOT BALL DIA.	ROOT BALL HEIGHT	TREE HEIGHT	TREE SPREAD
45L	380MM	400MM	1.2-2.0M	0.5M
100L	510MM	500MM	1.5-2.5M	0.75M
200L	650MM	600MM	1.8-3.0M	1.2M
400L	950MM	600MM	2.5-4.0M	2.0M
1000L	1200MM	900MM	5.0-6.5M	3.0M
2000L	1740MM	1050MM	5.5-7.5M	4.0M

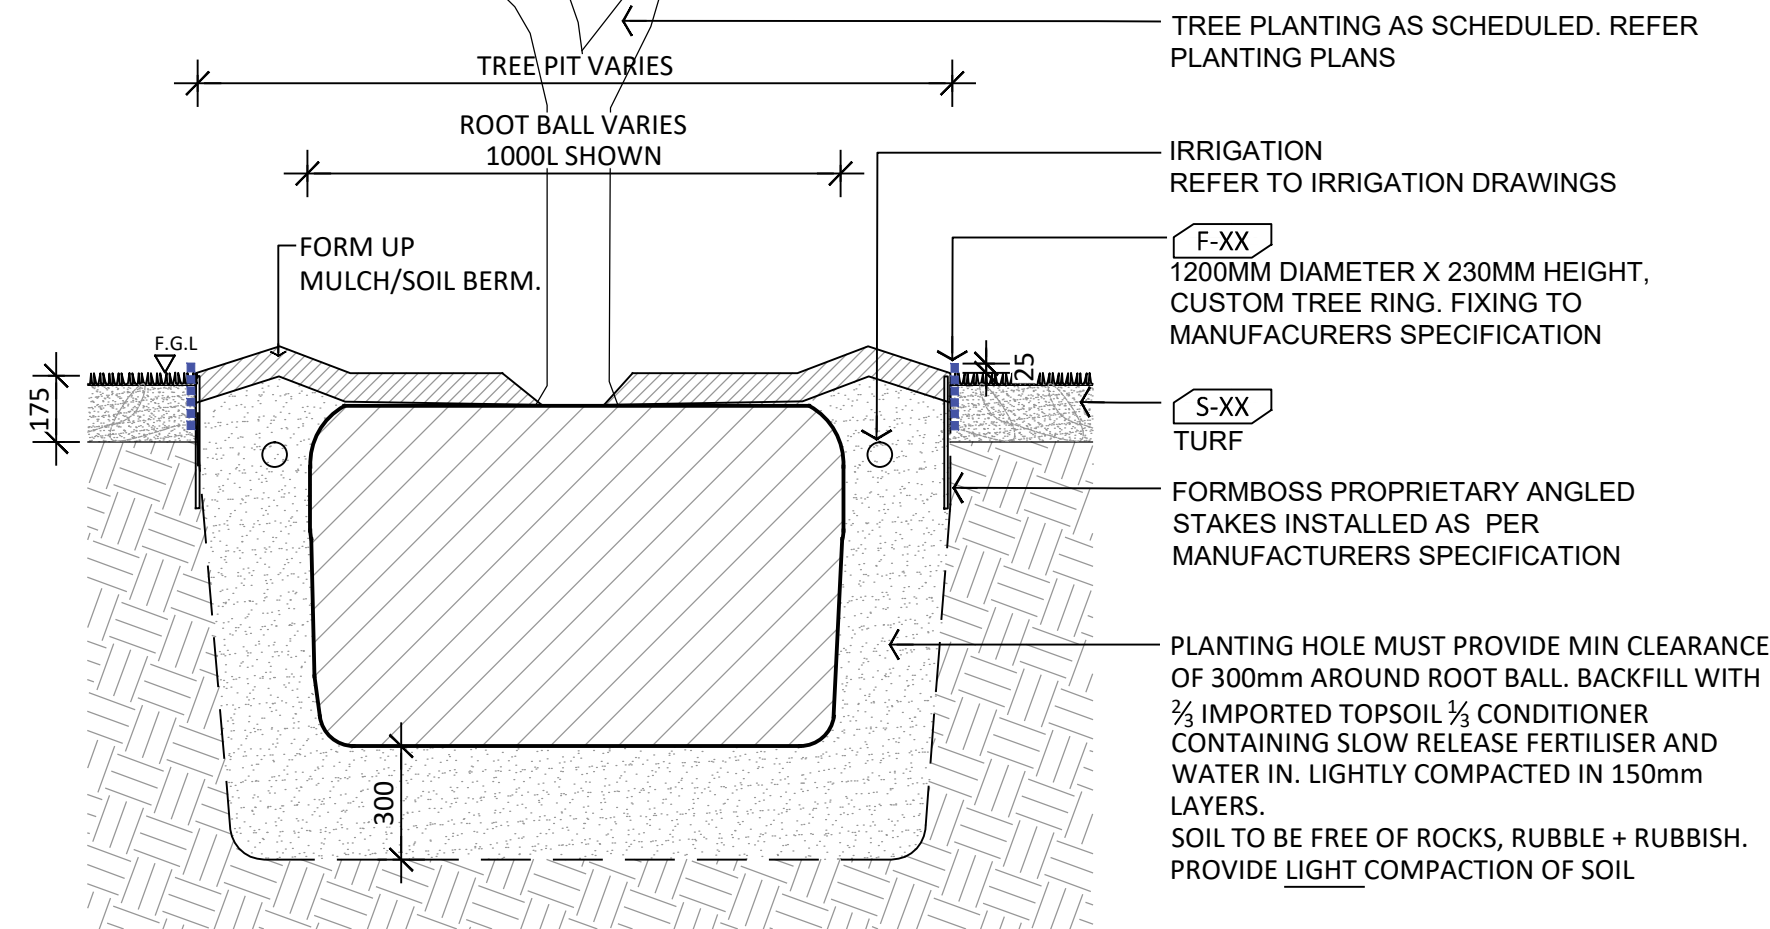

TREE - TURF TYP.
SECTION DETAIL 1:20

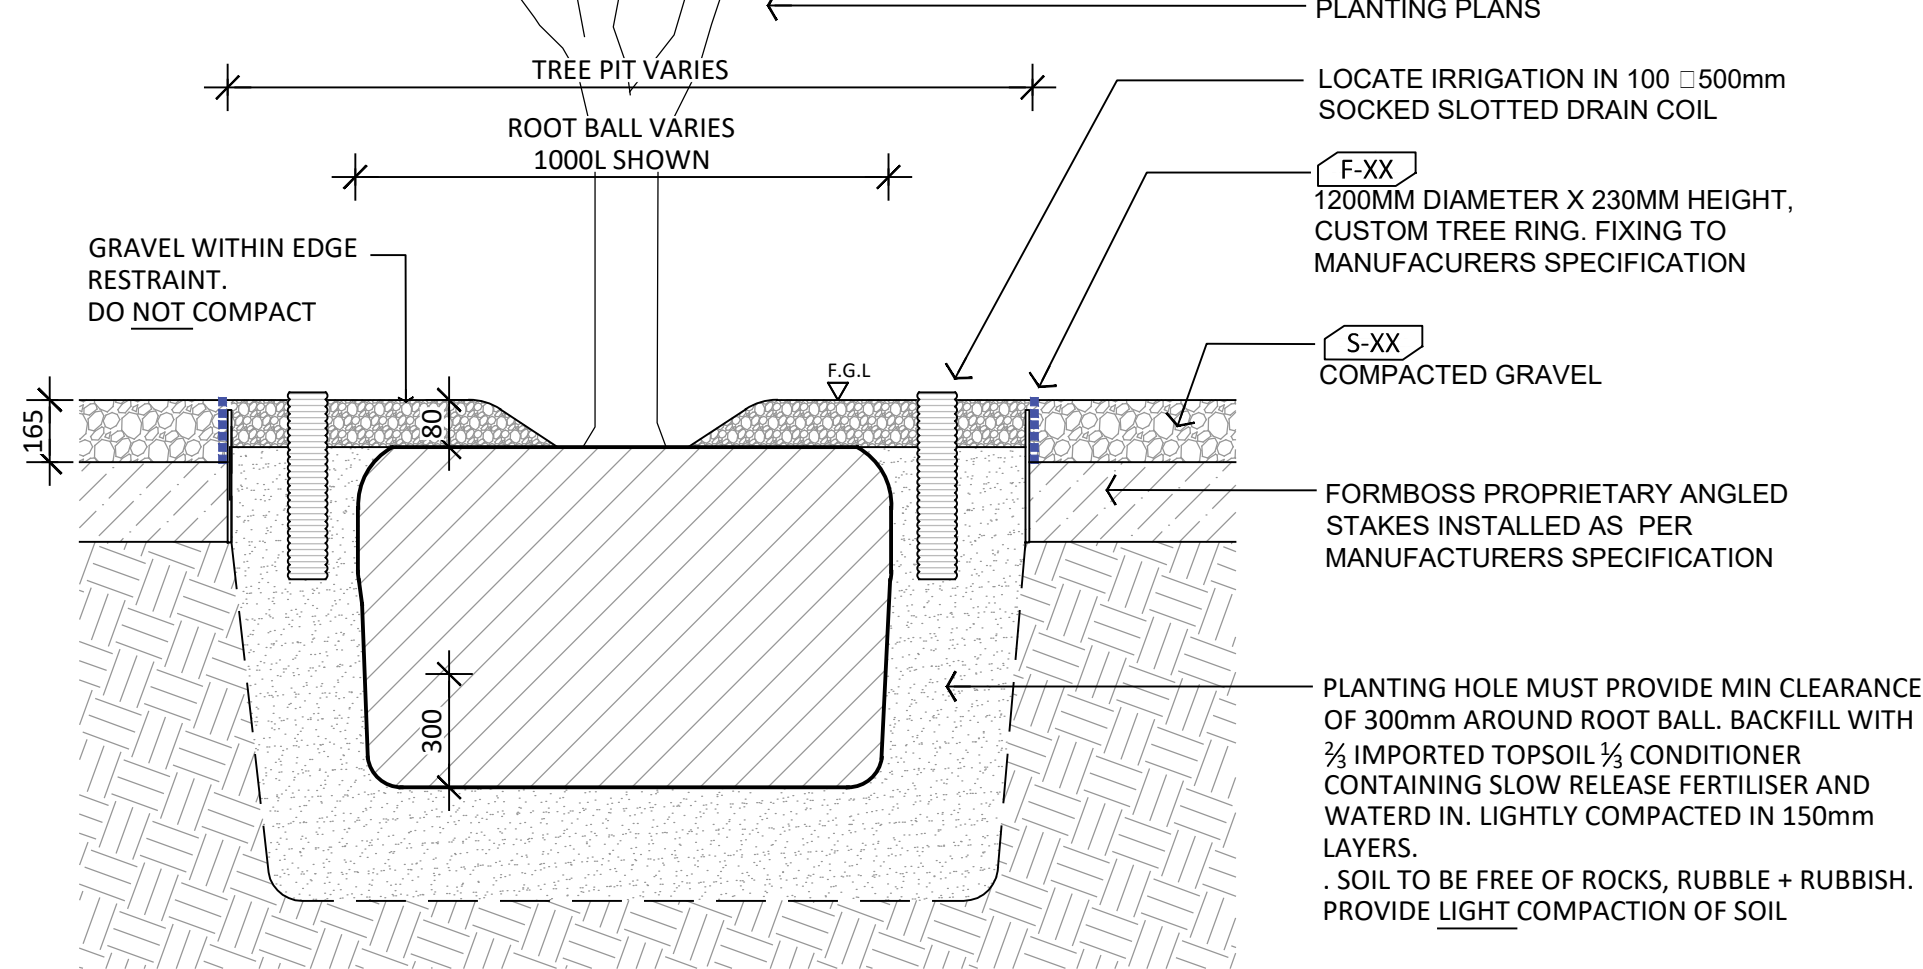

TREE - GRAVEL (TRAFFICABLE) TYP.
SECTION DETAIL 1:20

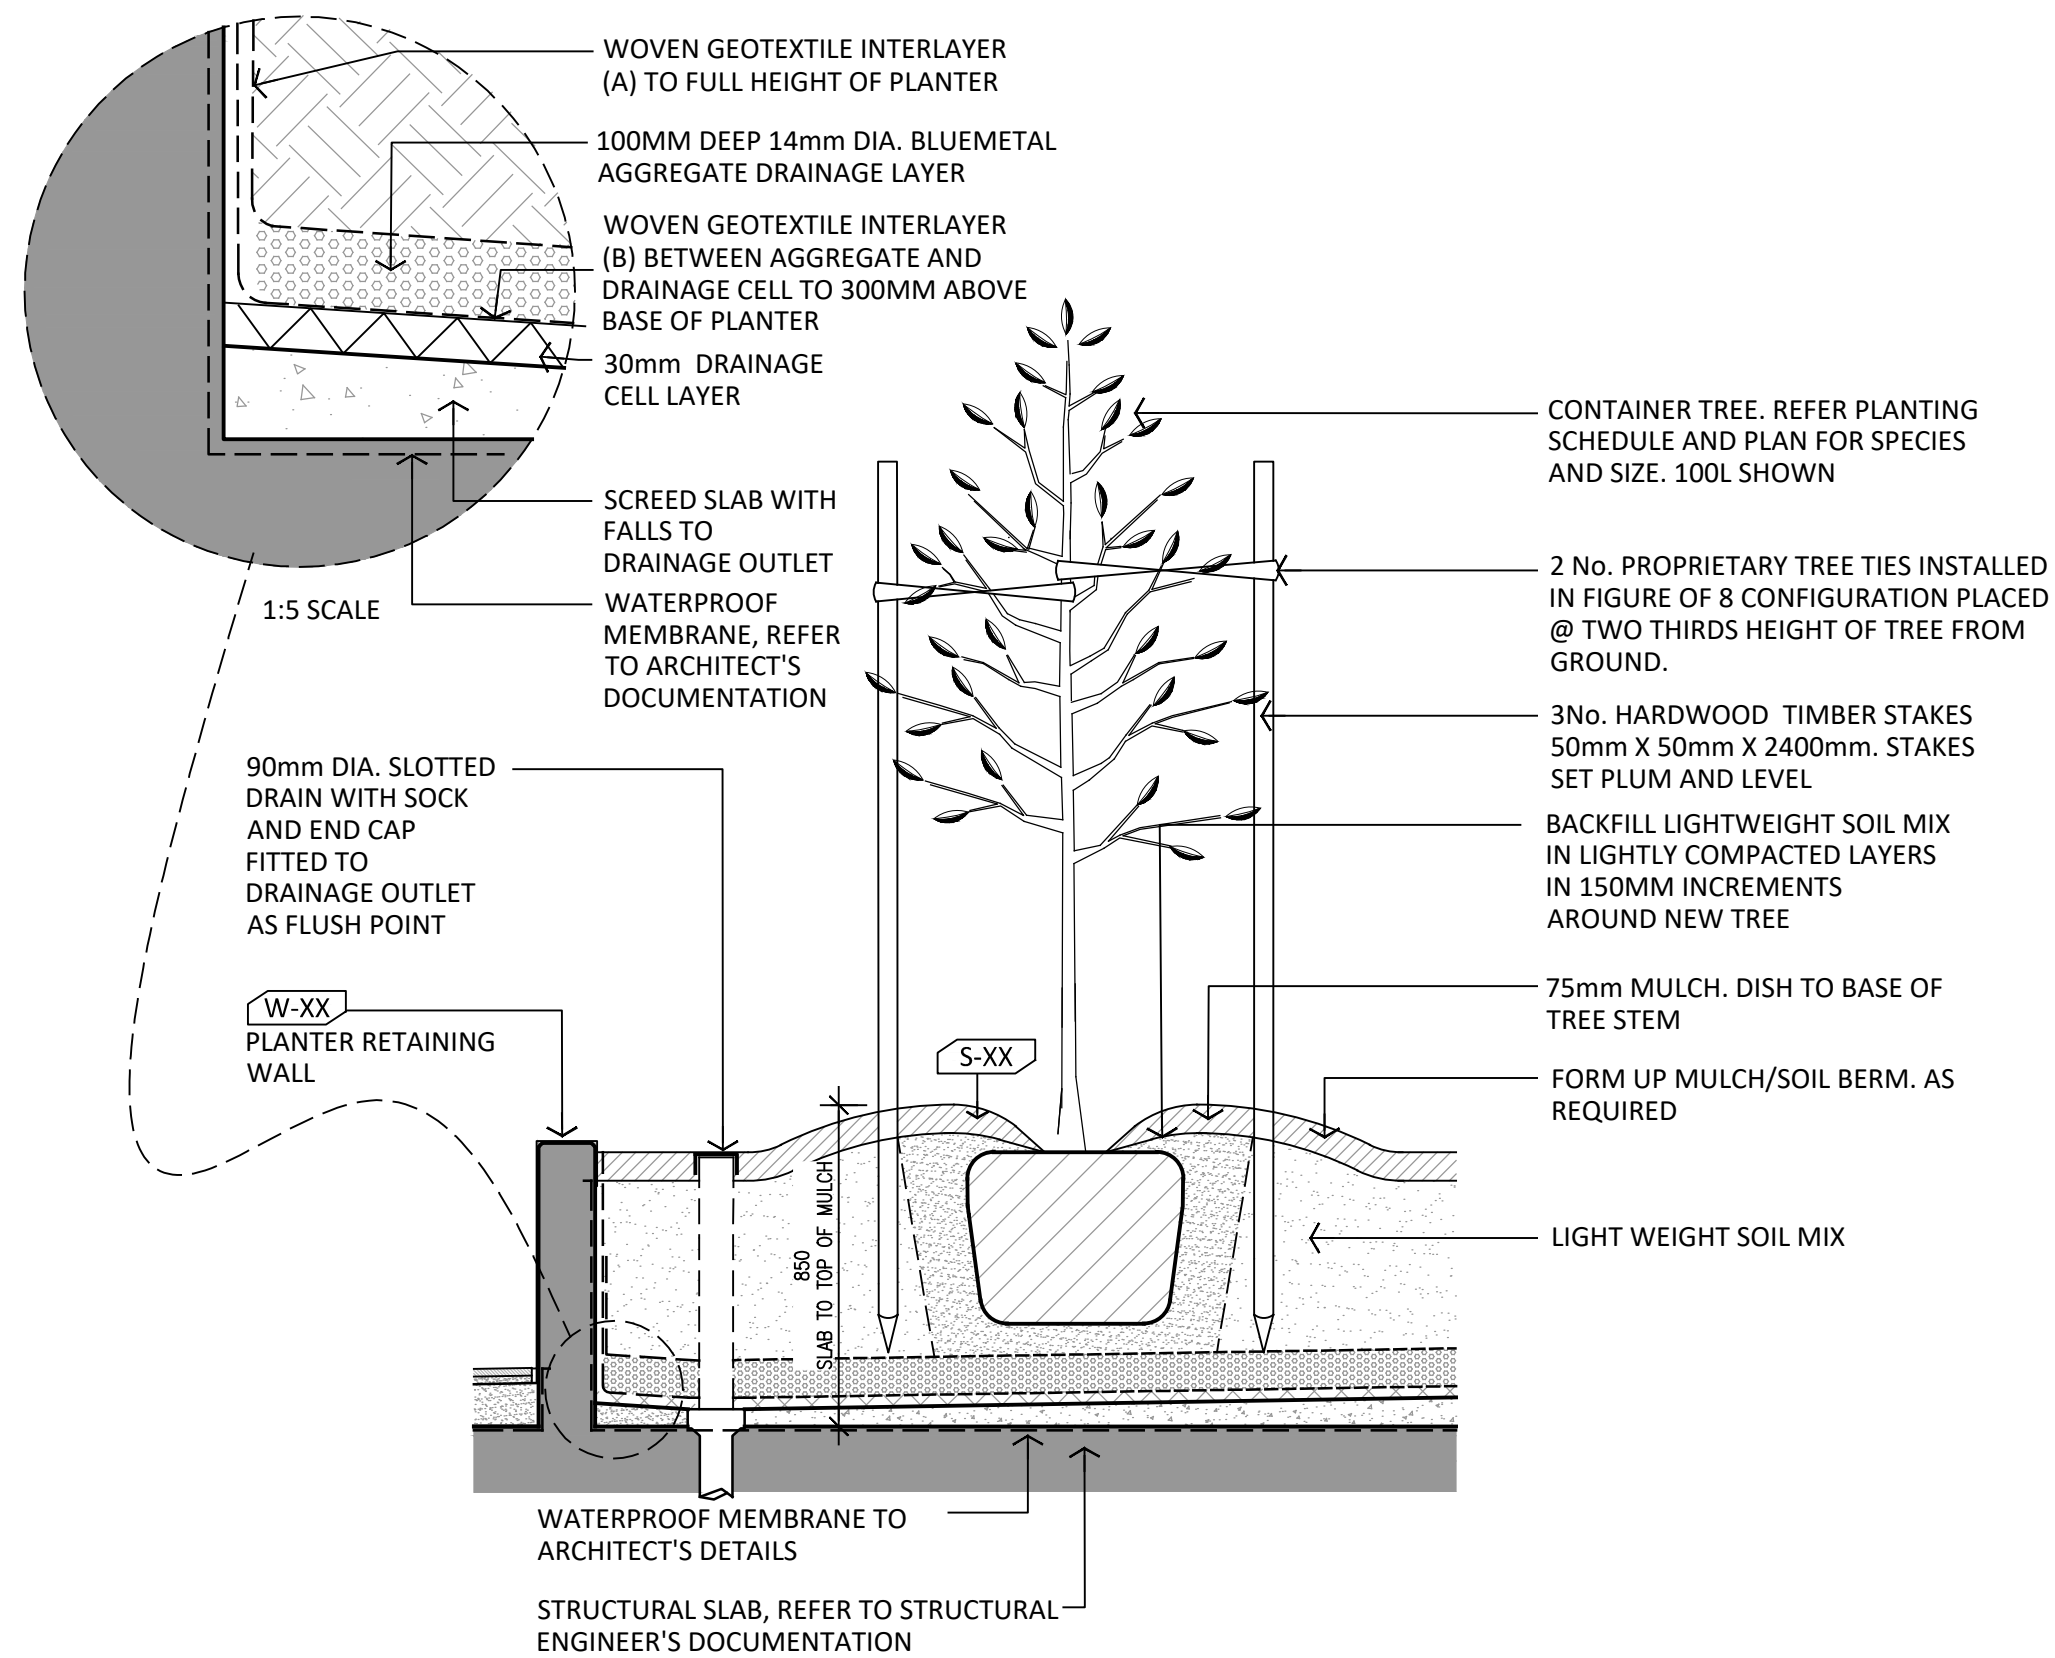

TREE - SLAB TYP.
SECTION DETAIL 1:20

williamdangar

+

PLACE

LABORATORY

Level 1, 289 Murray Street, Perth
Western Australia, Australia, 6000

T +61 8 9227 9313
M +61 402 700 162
E: ourplace@placelaboratory.com
W: www.placelaboratory.com

CLIENT

MINDEROO FOUNDATION

PO BOX 3155 BROADWAY,
NEDLANDS, WA 6009




COTTESLOE BEACH HOUSE

LANDSCAPE DESIGN

SOFTSCAPE DETAILS


PLACE LAB PROJ No	1659	SCALE:	AS SHOWN
DWG STATUS	----	UNIT:	mm
DWG No	1659-L-900	SHEET SIZE:	A1
		ISSUE	----

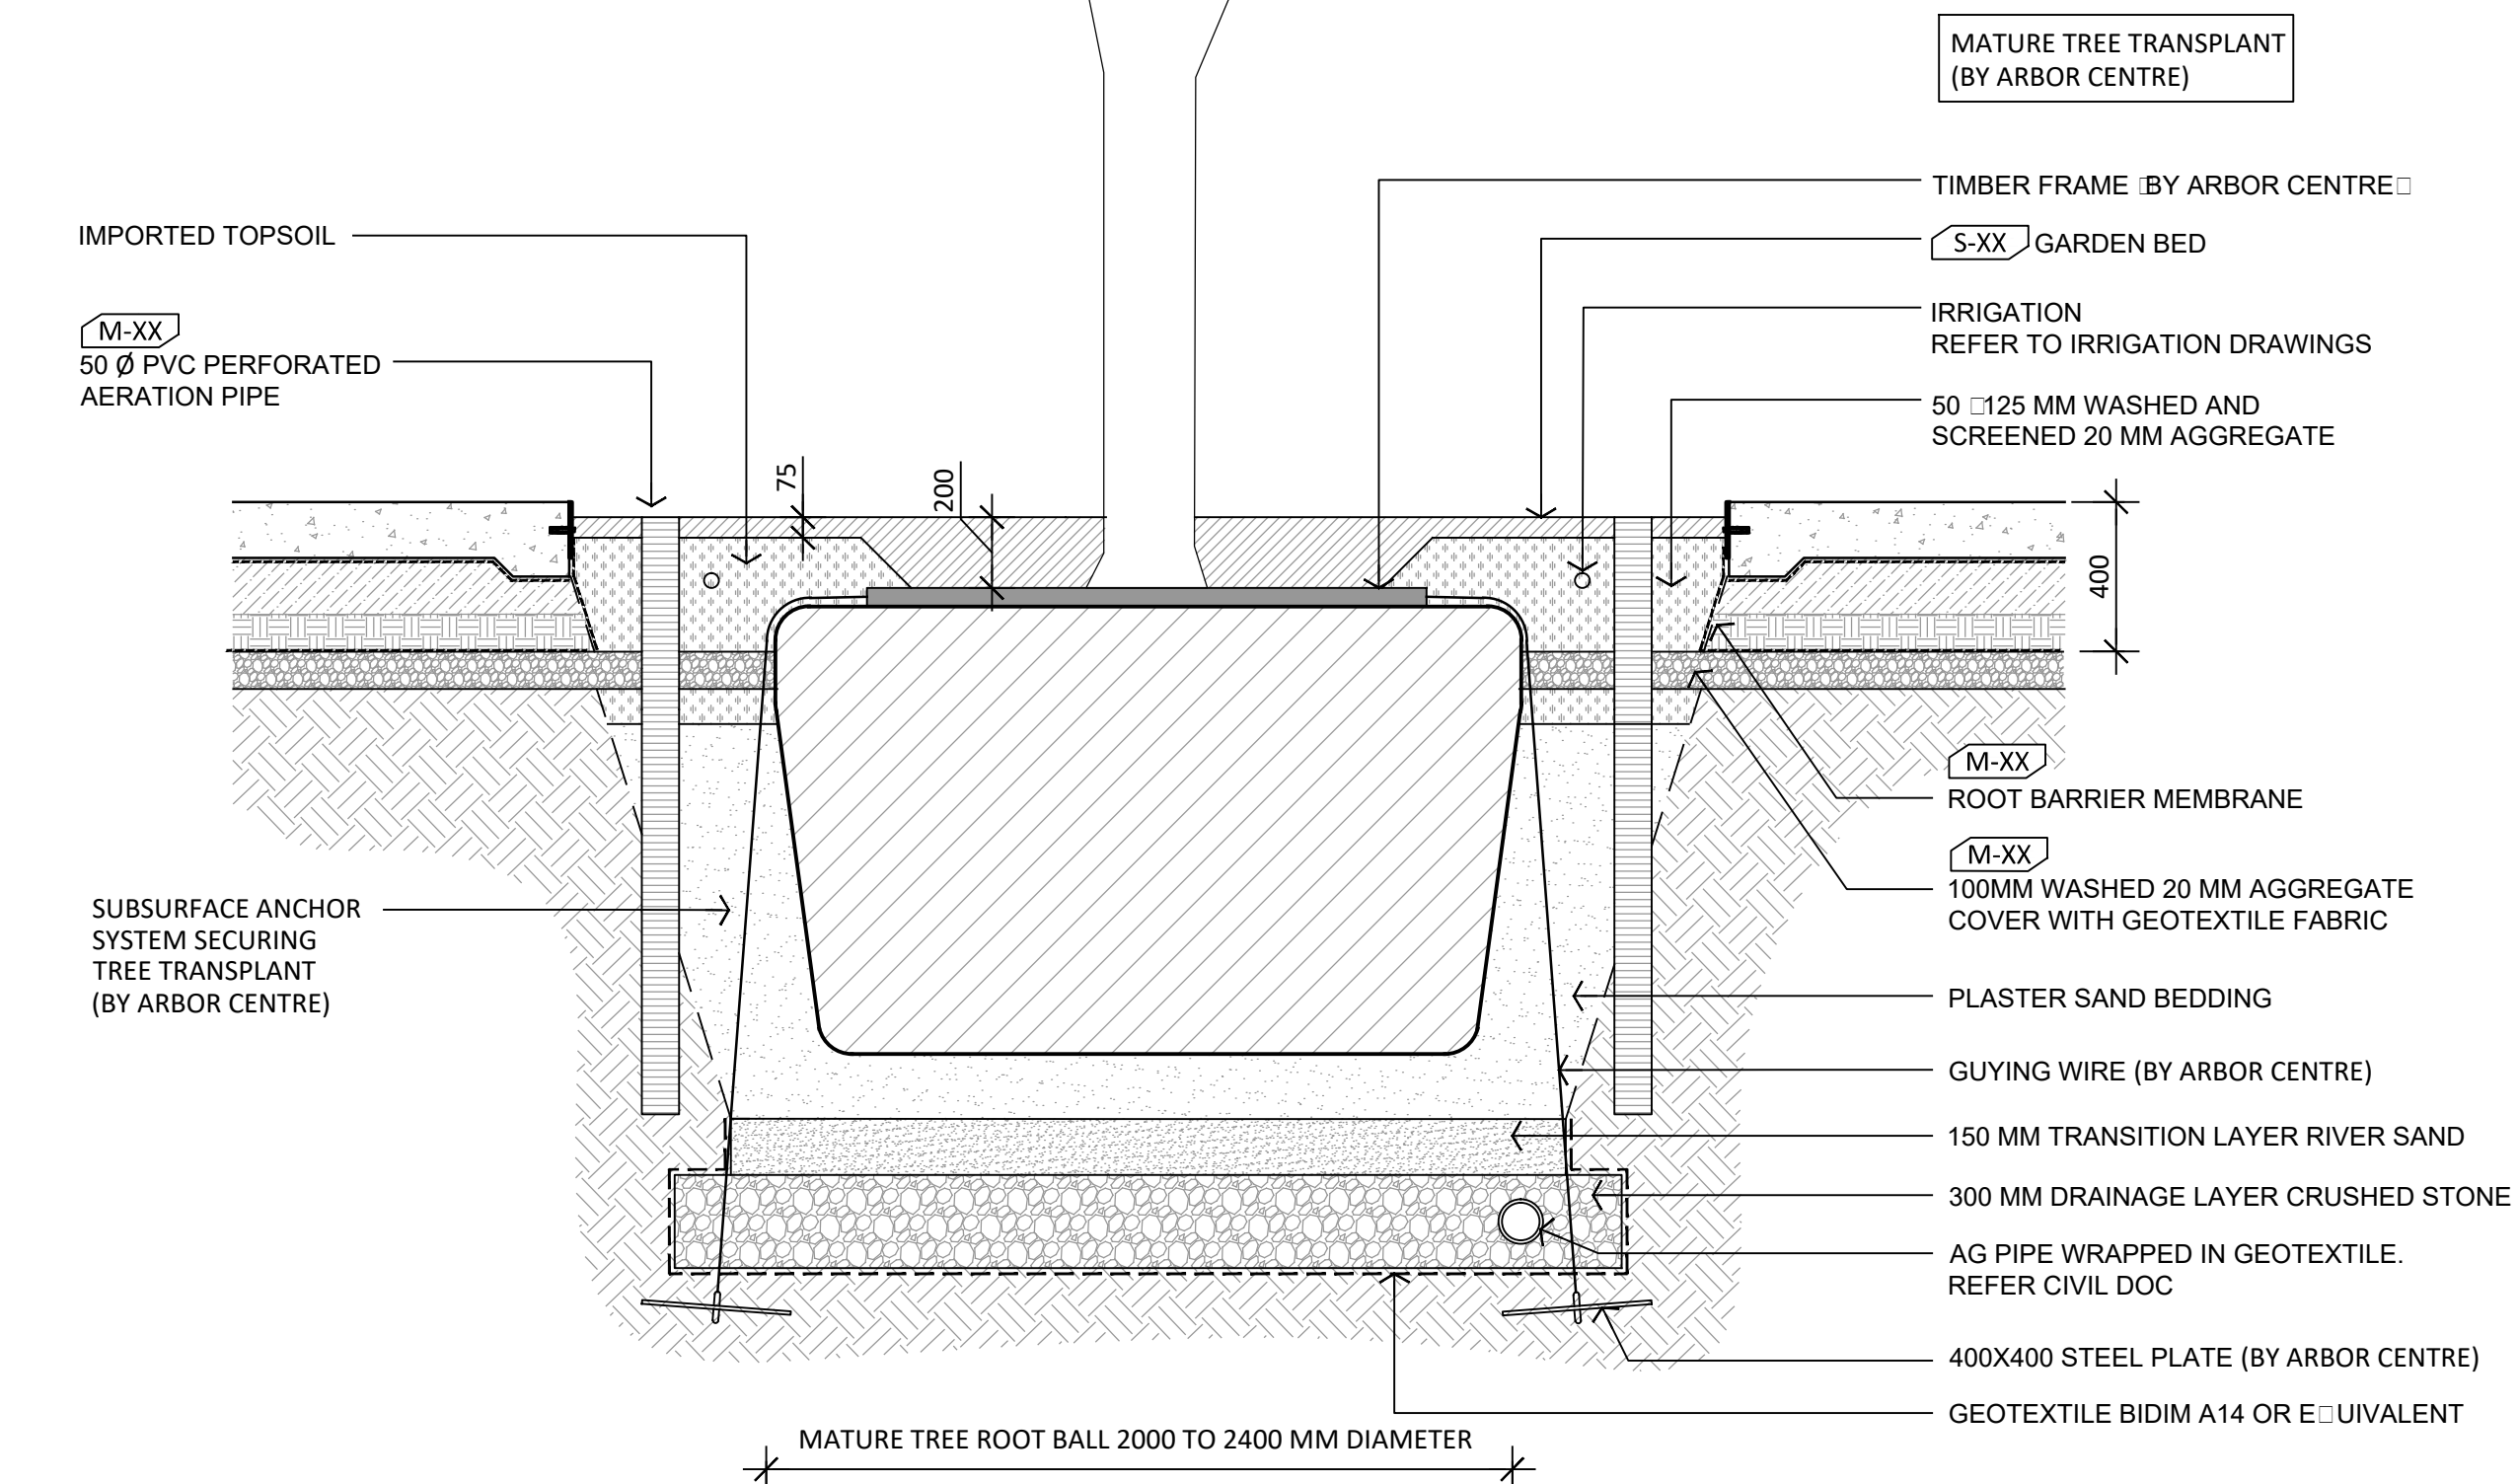

TREE TRANSPLANT & SUBSURFACE GUYING - GROUND TYP.

SECTION


1:20

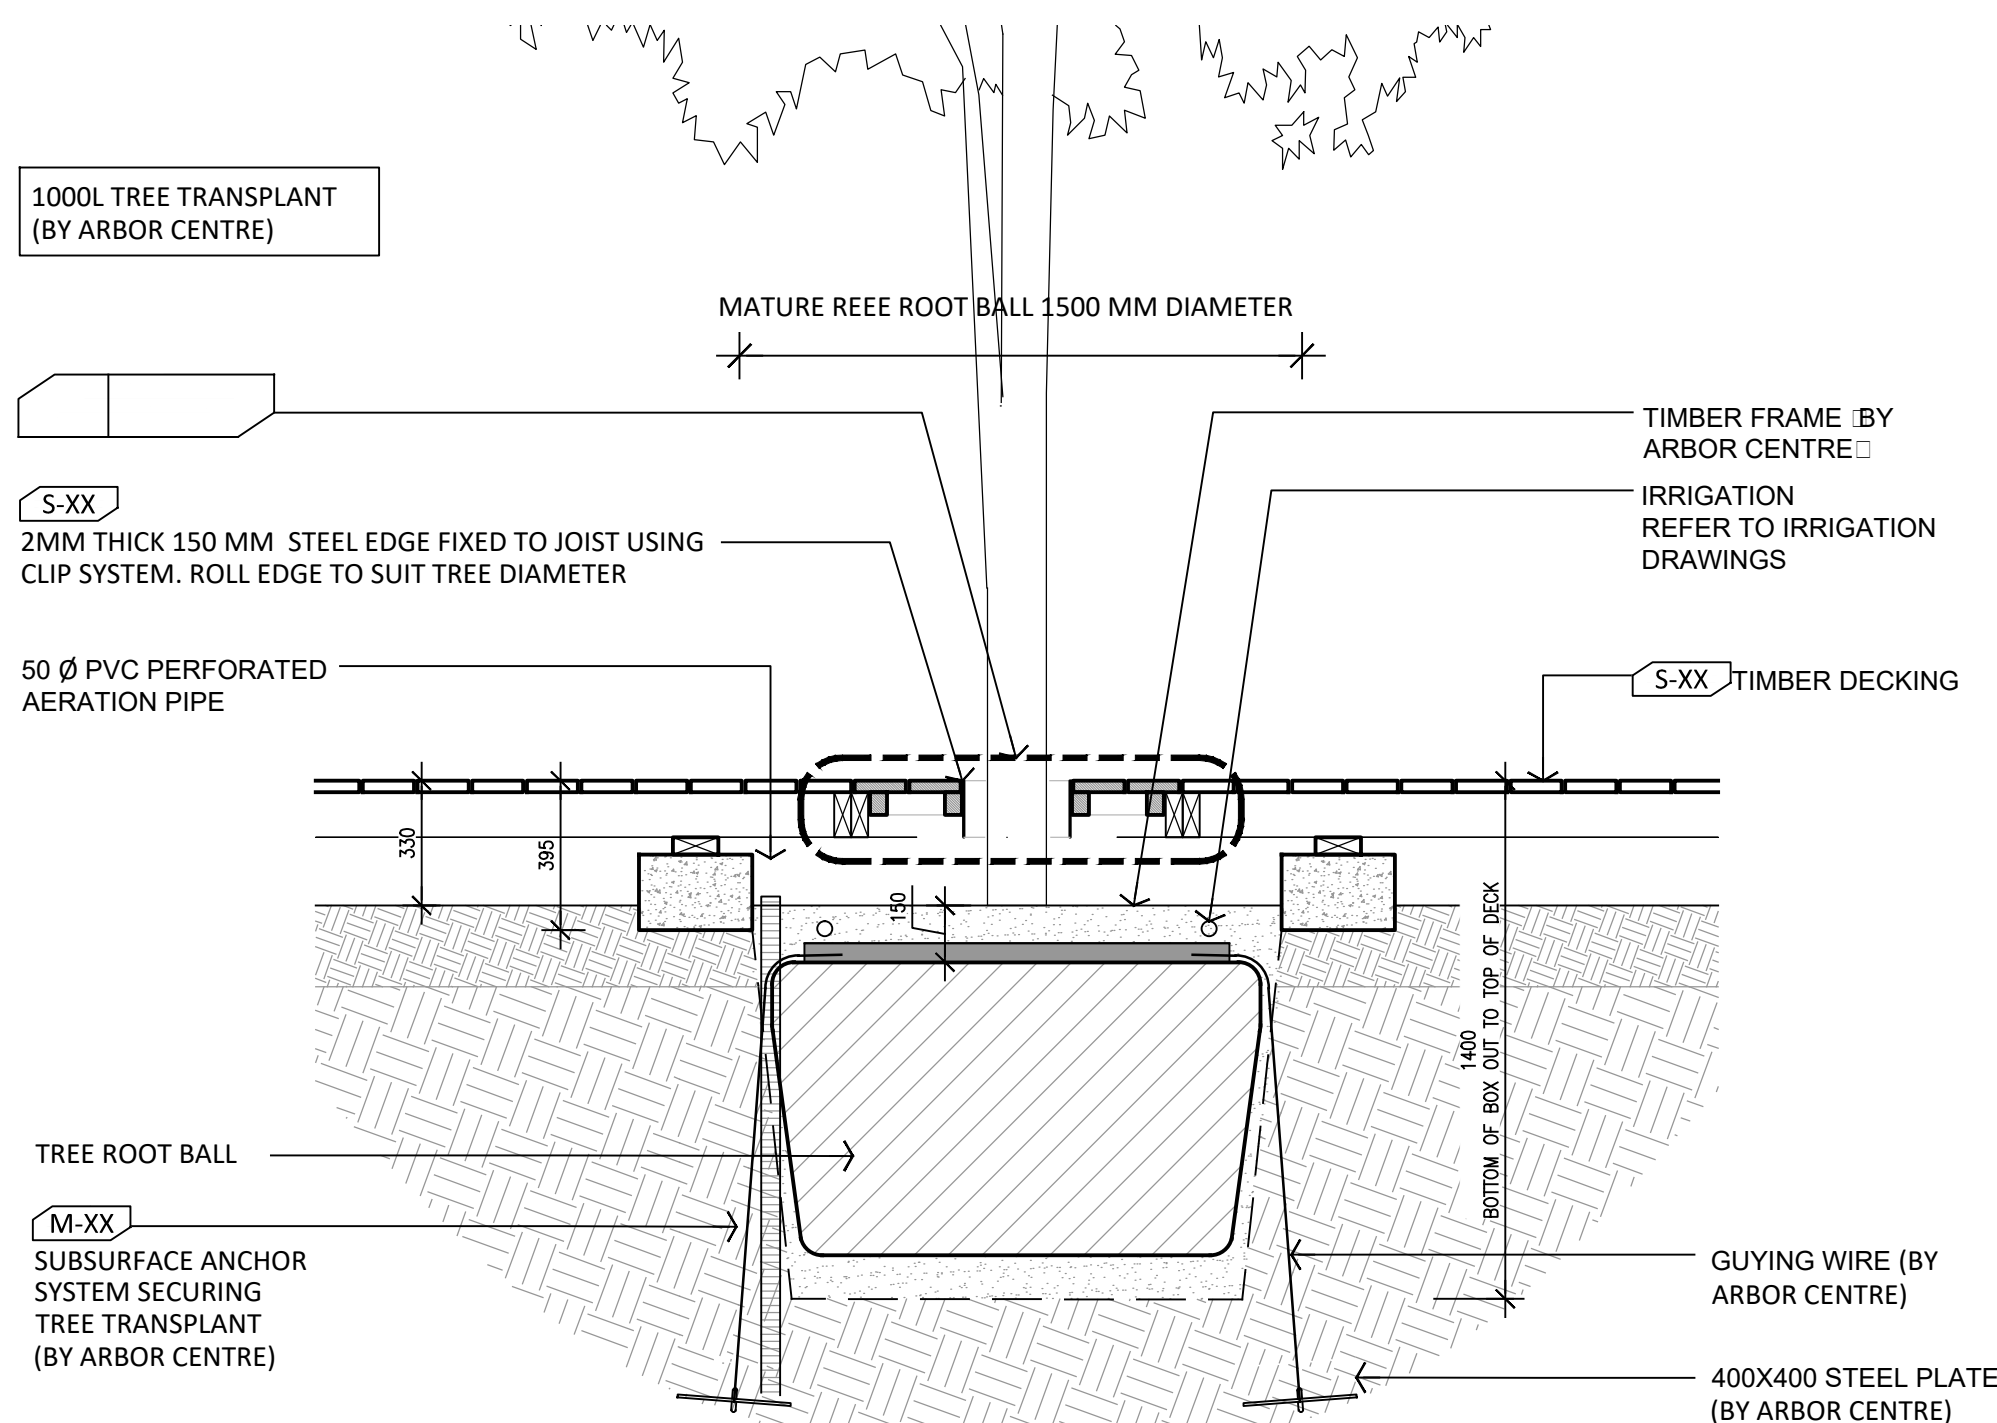

TREE TRANSPLANT - DECK TYP. (SECTION)

SECTION

1:20

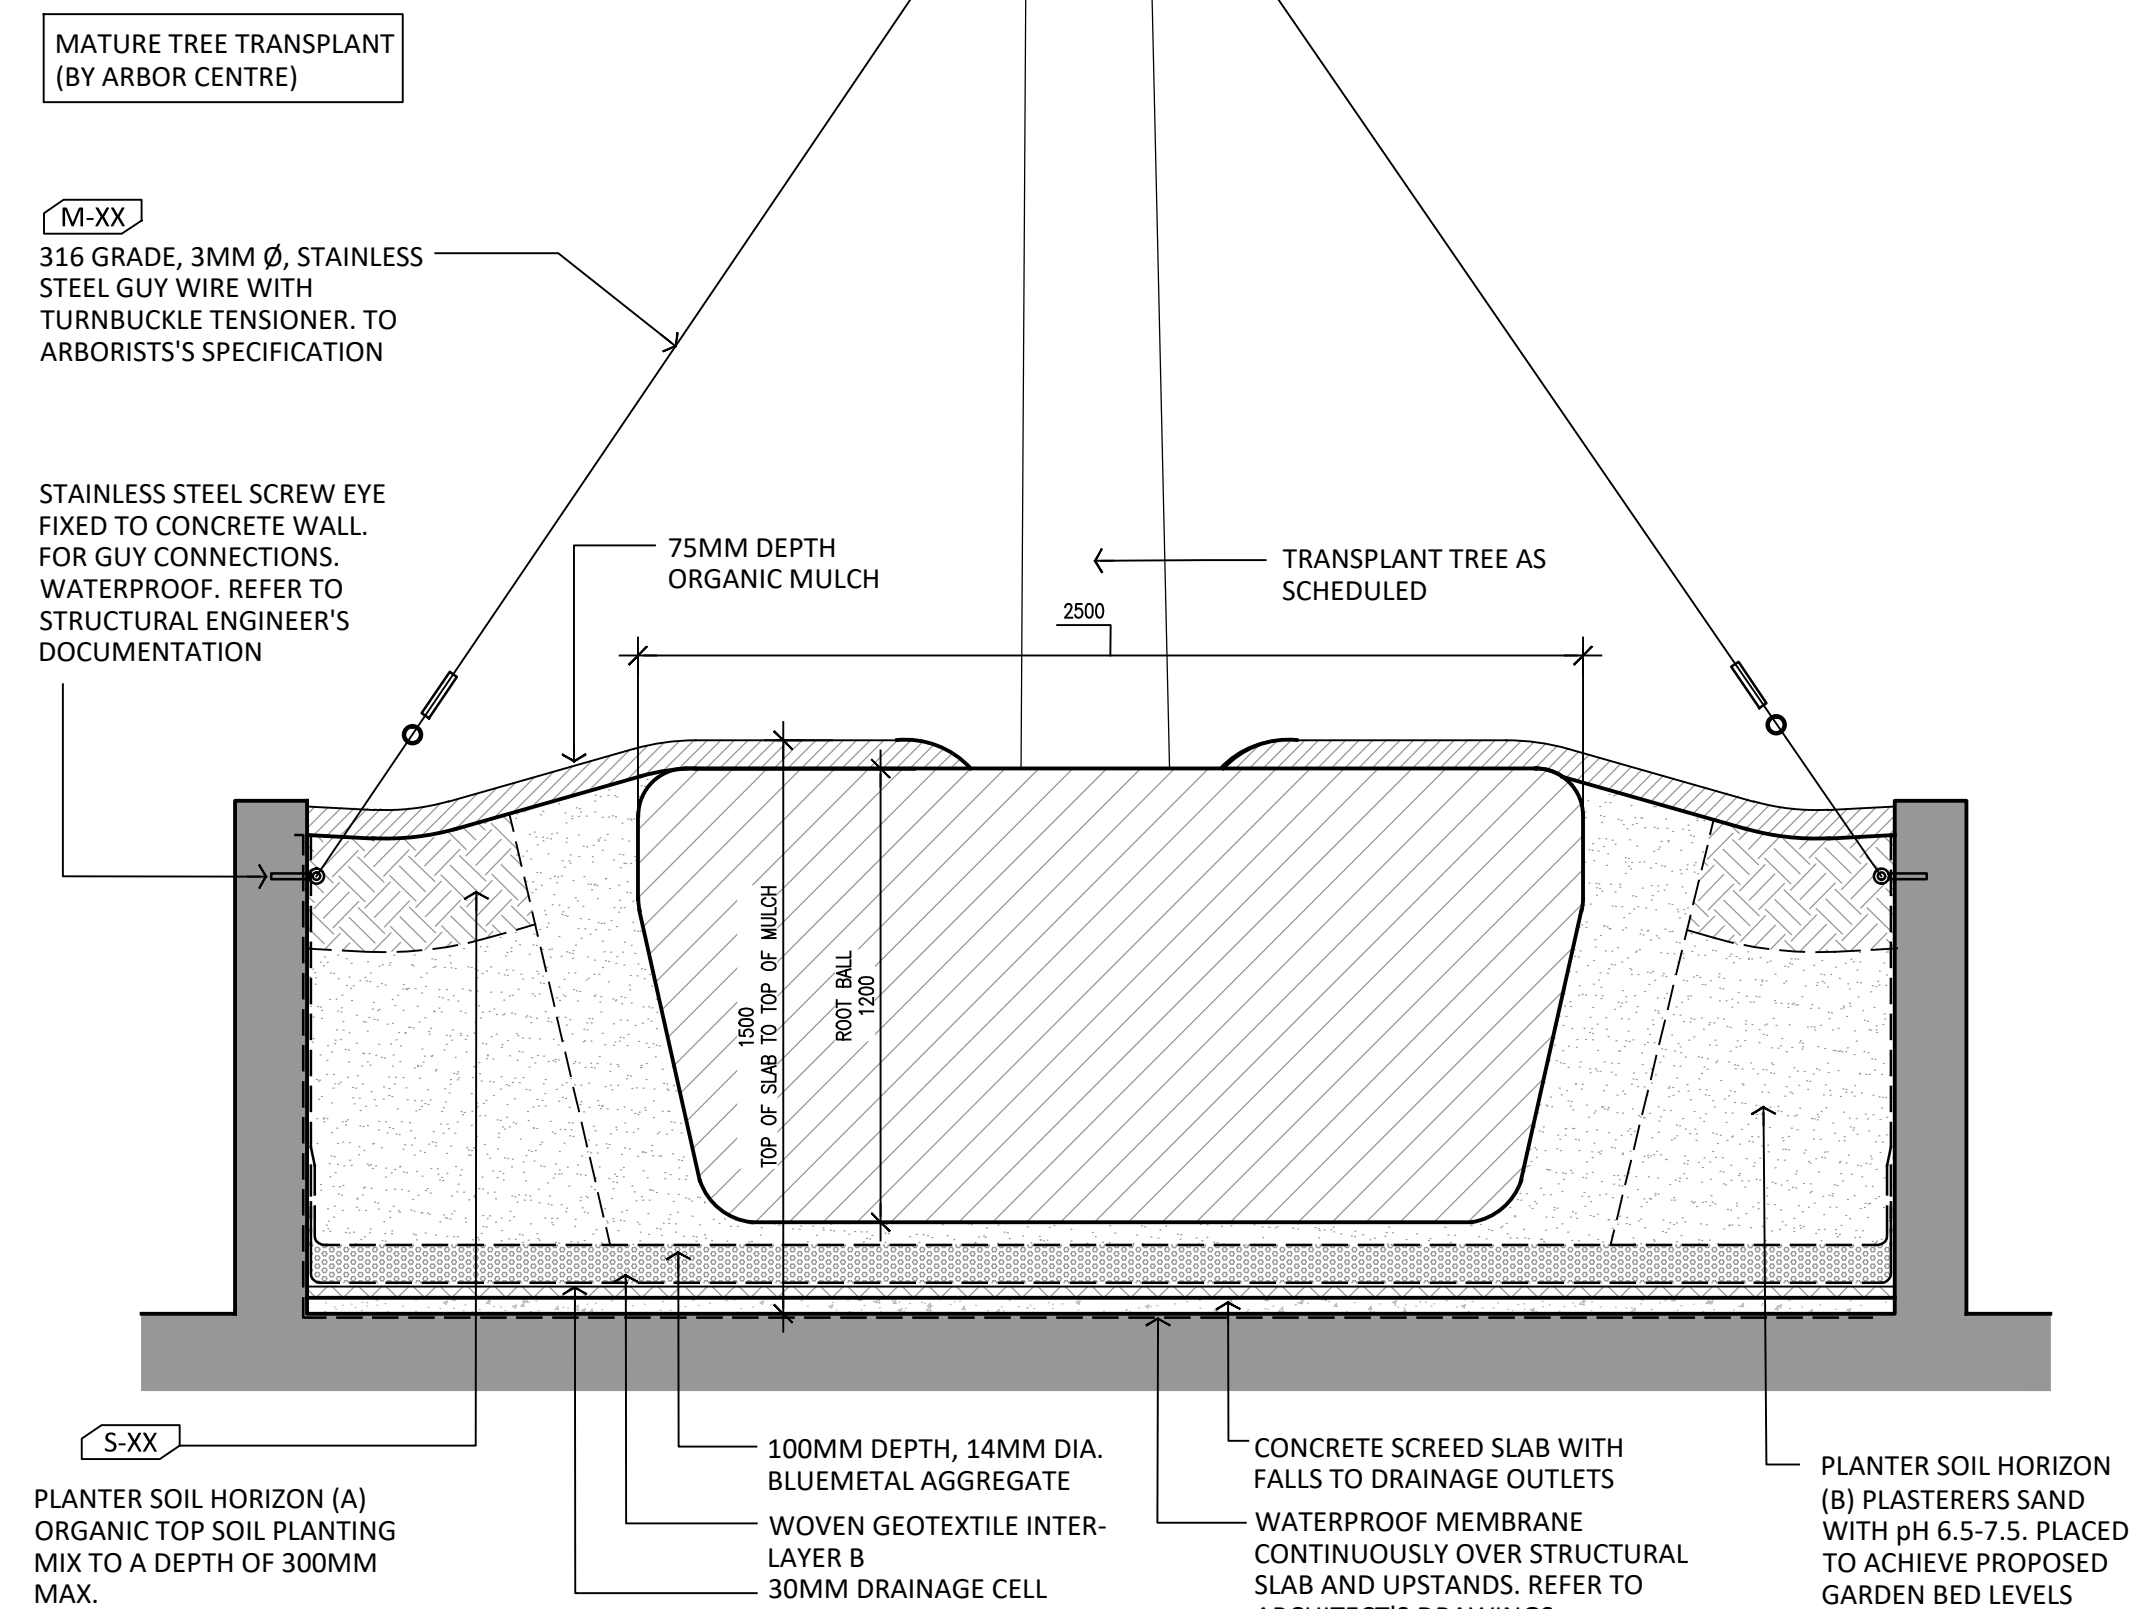

TREE TRANSPLANT & GUYING - SLAB TYP.

SECTION

1:20

- ### **TREE TRANSPLANT NOTES:**
1. CONTRACTOR TO ALLOW FOR COORDINATION OF THE WORK WITH ARBOR CENTRE.
 2. ELECTRICAL CONDUITS FOR LIGHTS TO BE INTEGRATED WITH ROOT BALL OF TRANSPLANTED TREES BY ARBORCULTURIST PRIOR TO PLANTING. REFER TO ELECTRICAL ENGINEER'S DOCUMENTATION FOR FURTHER DETAIL.
 3. CONTRACTOR SHALL ENSURE THAT IRRIGATION WATERING TO THE TRANSPLANT TREES IS AVAILABLE ON INSTALLATION OF TREES.
 4. CONTRACTOR SHALL LIAISE WITH ARBORCULTURIST TO ENSURE THAT PLANTING HOLES AND IN-GROUND GUYING DON'T CONFLICT WITH PROPOSED AND EXISTING SERVICES.
 5. GUYING SPECIFIED ARE TO COMPLY WITH THE AUSTRALIAN LOADING CODE FOR WINDS APPLICABLE TO PERTH (AS 1170.2:2014). (SUPPLY BY ARBOR CENTRE)
 6. INSTALLATION OF AERATION LAYER TO BE INITIATED UNDER THE SUPERVISION OF THE PROJECT ARBORICULTURIST
 7. CONTRACTOR SHALL ENSURE CARE IS TAKEN WHEN POURING FINISHING CONCRETE TO AVOID CONTAMINATION OF TREE PIT
 8. INSTALLATION, METHOD FOR CABLEING, CONDUITS AND LIGHT FITTINGS TO BE ESTABLISHED WITH ARBOR CENTRE PRIOR TO INSTALLATION.