


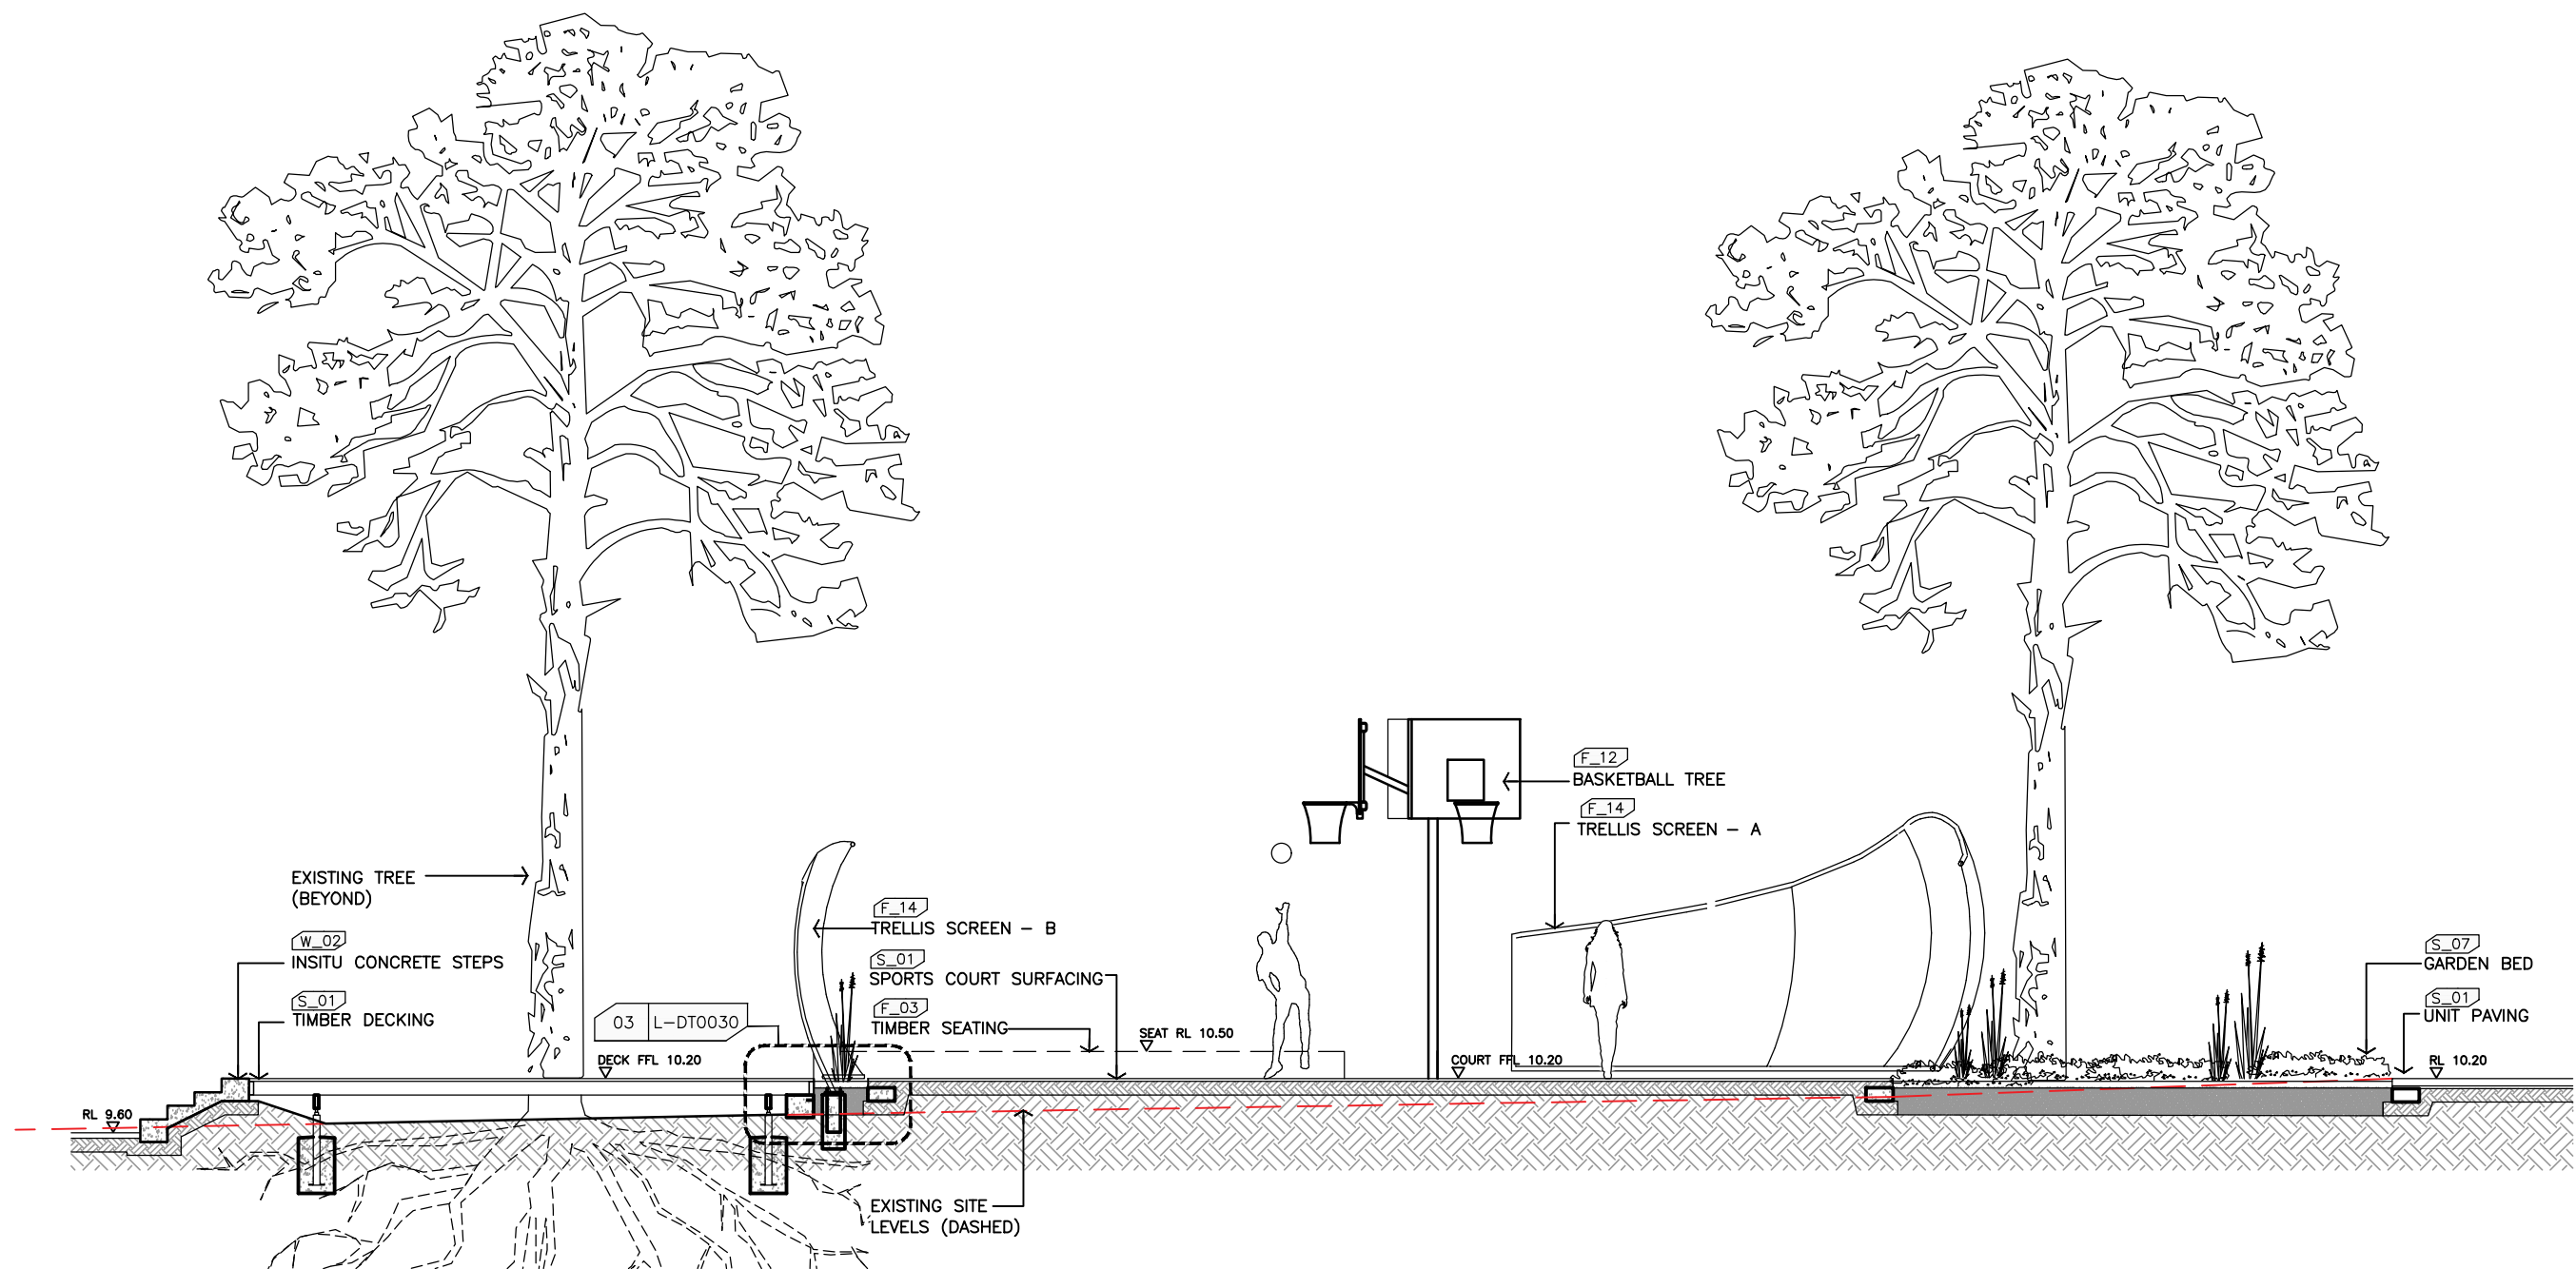



01

L-GA0001

GAMES COURT & DECK SECTION

SECTION

1:50

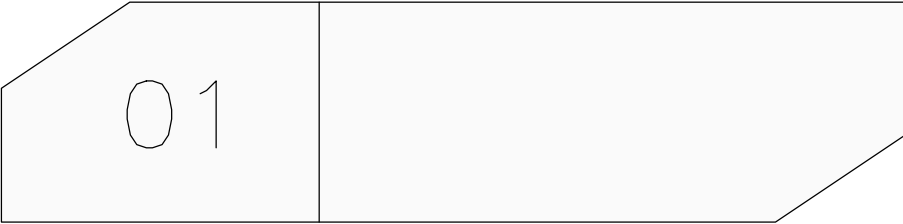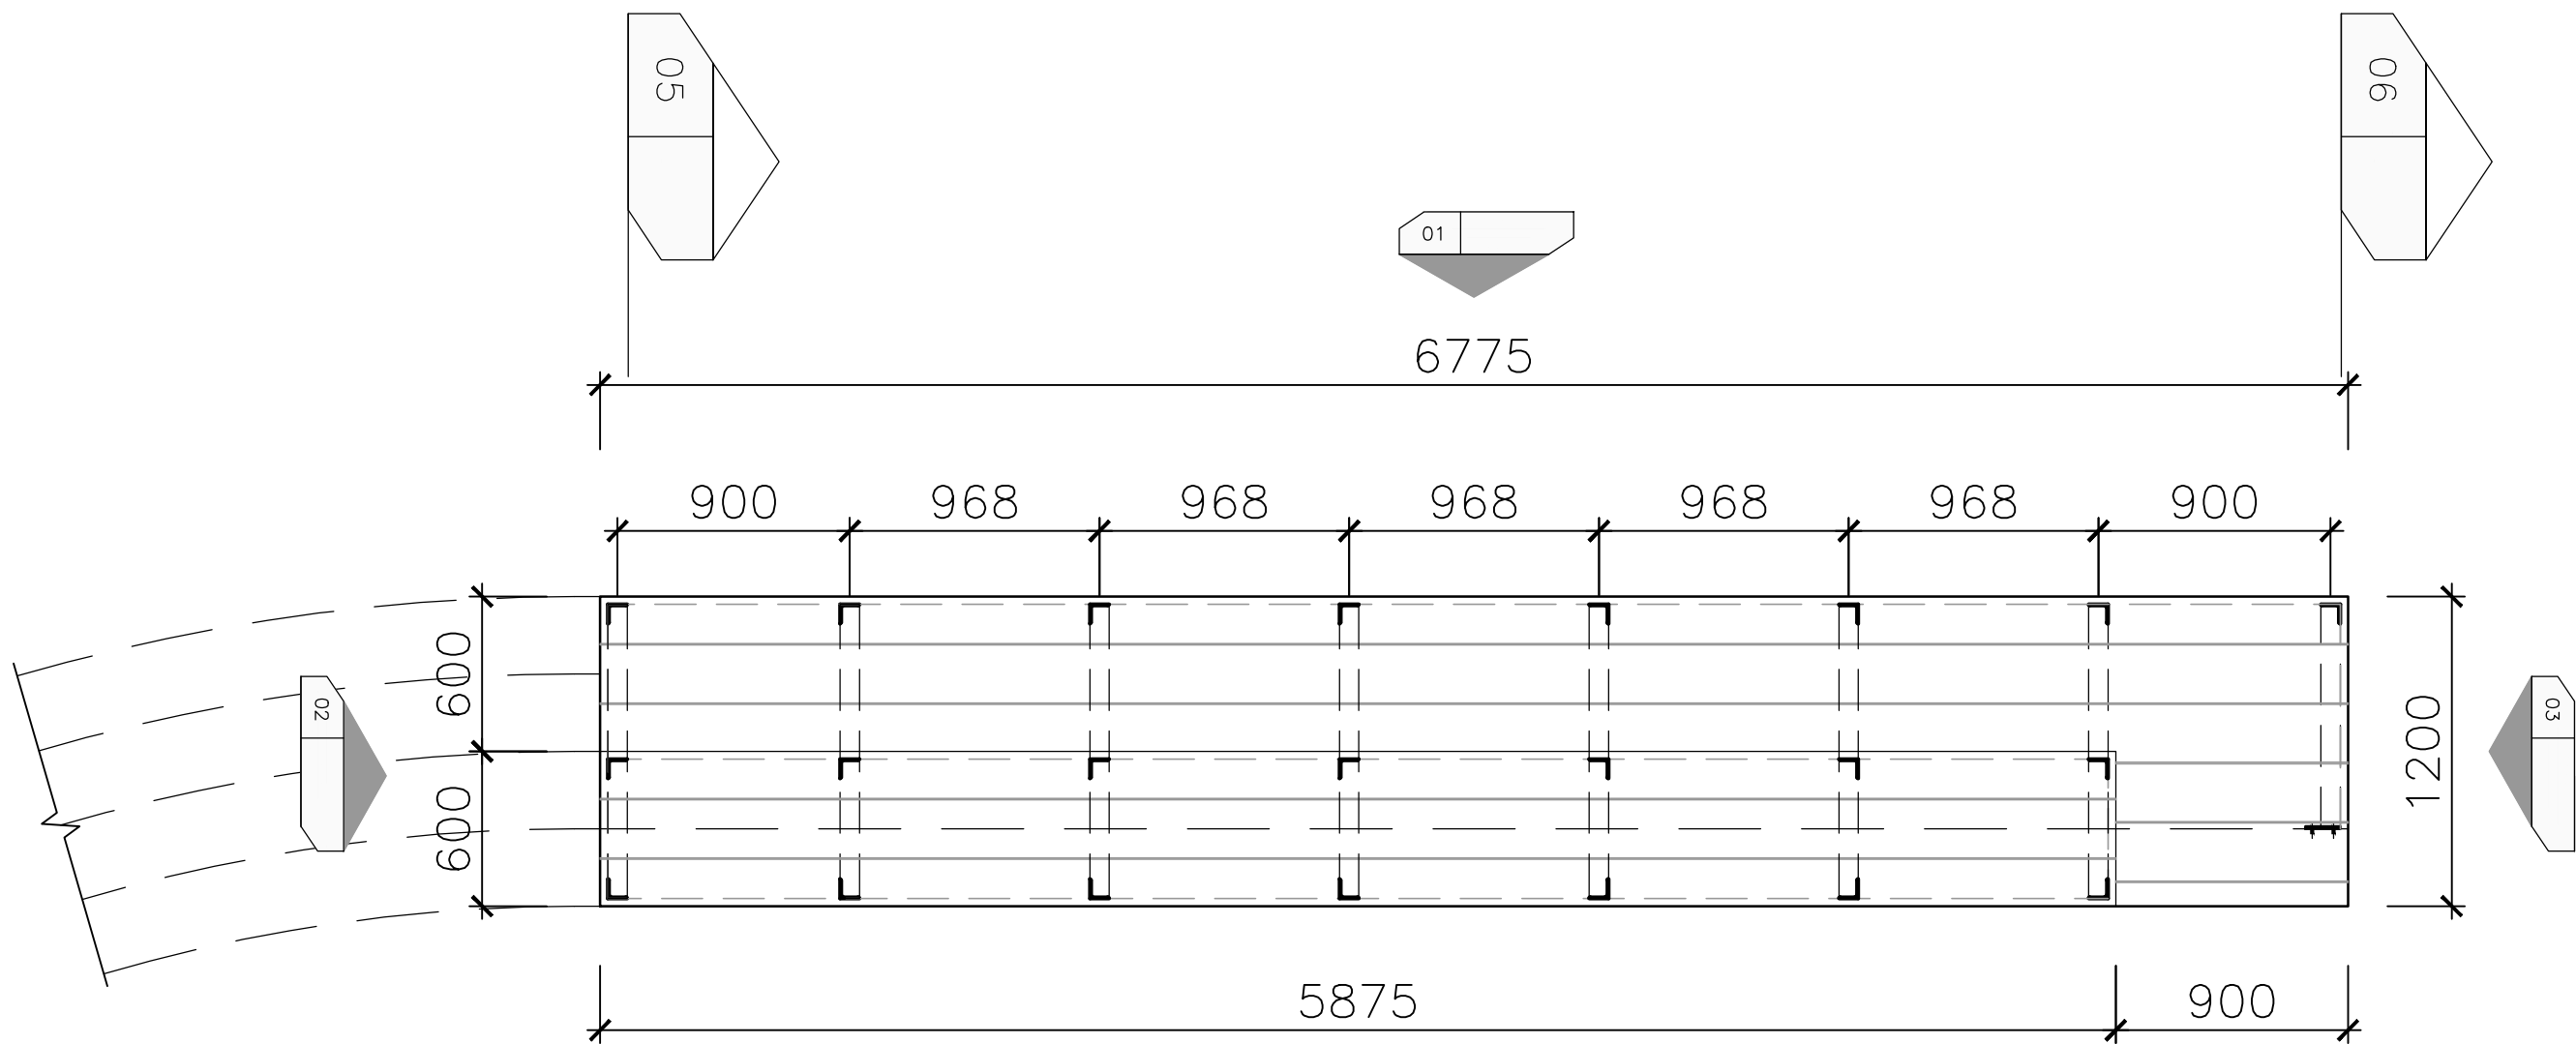


F-03 TIMBER SEATING - STRUCTURE

DETAIL PLAN

1:50

is this not
more like 9.7?

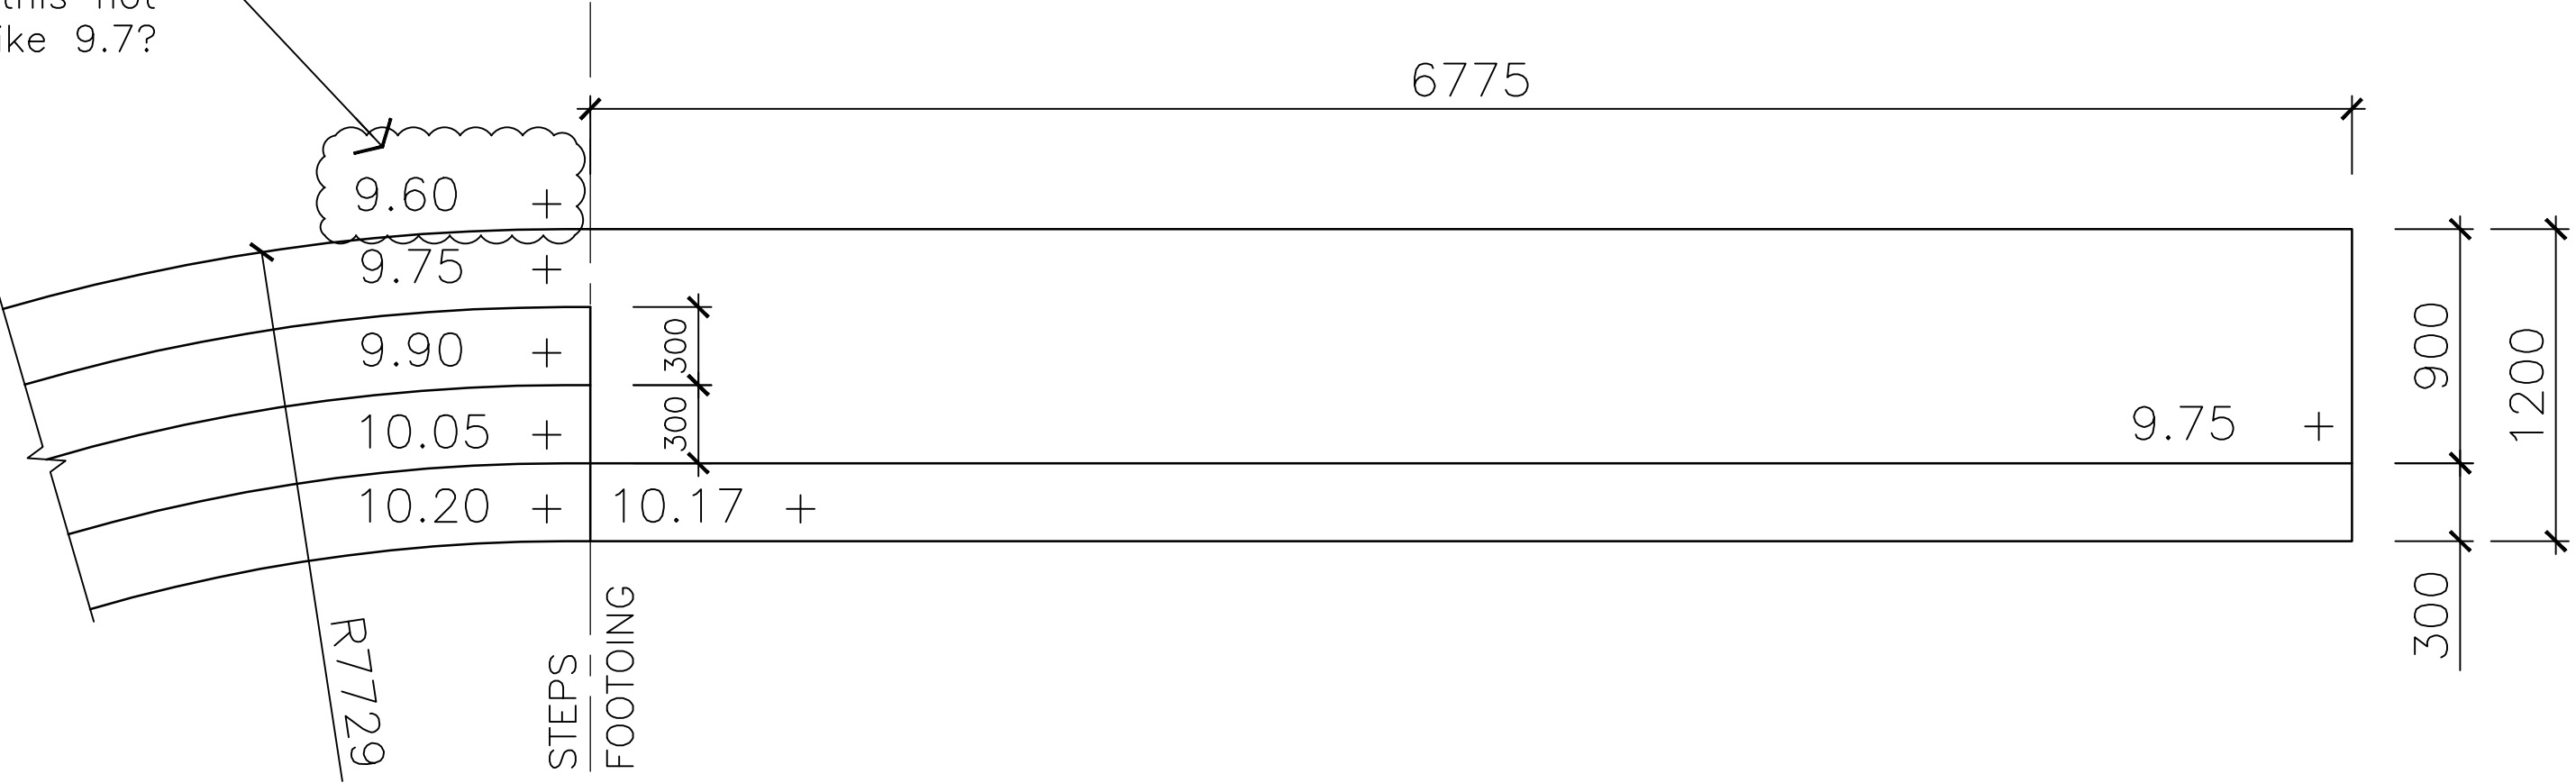


01


F-03 TIMBER SEATING - FOOTING PLAN

DETAIL PLAN



1:50

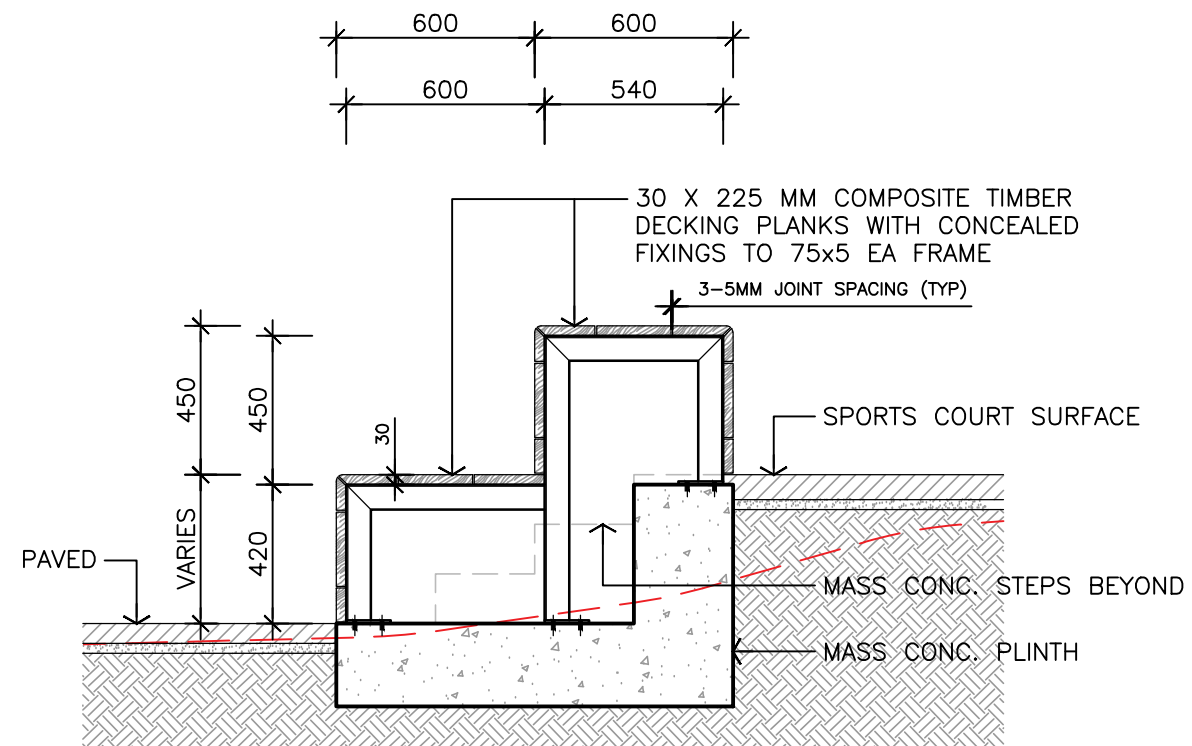


05 SECTION
SECTION 1:20

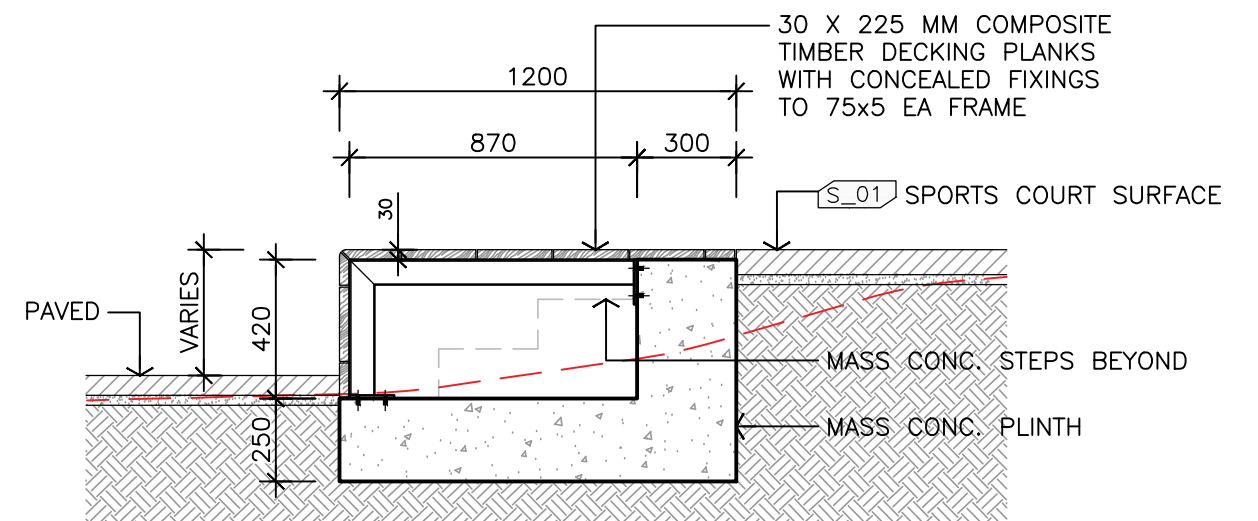

06 SECTION
SECTION 1:20

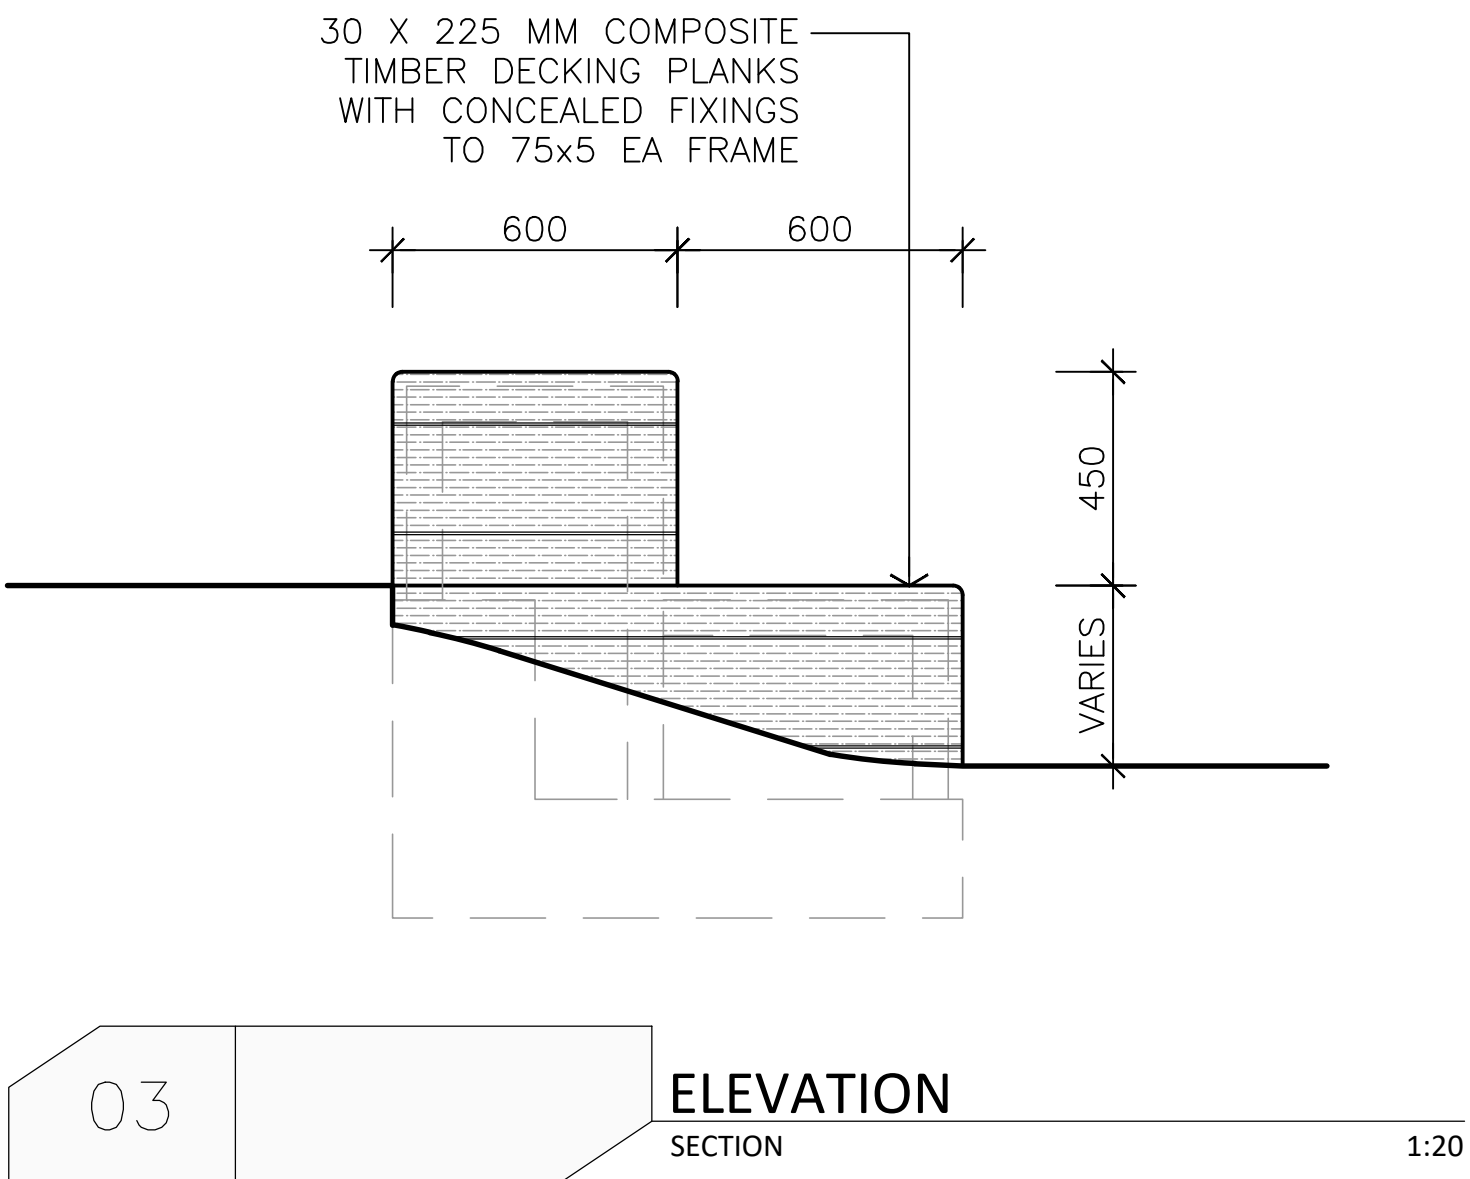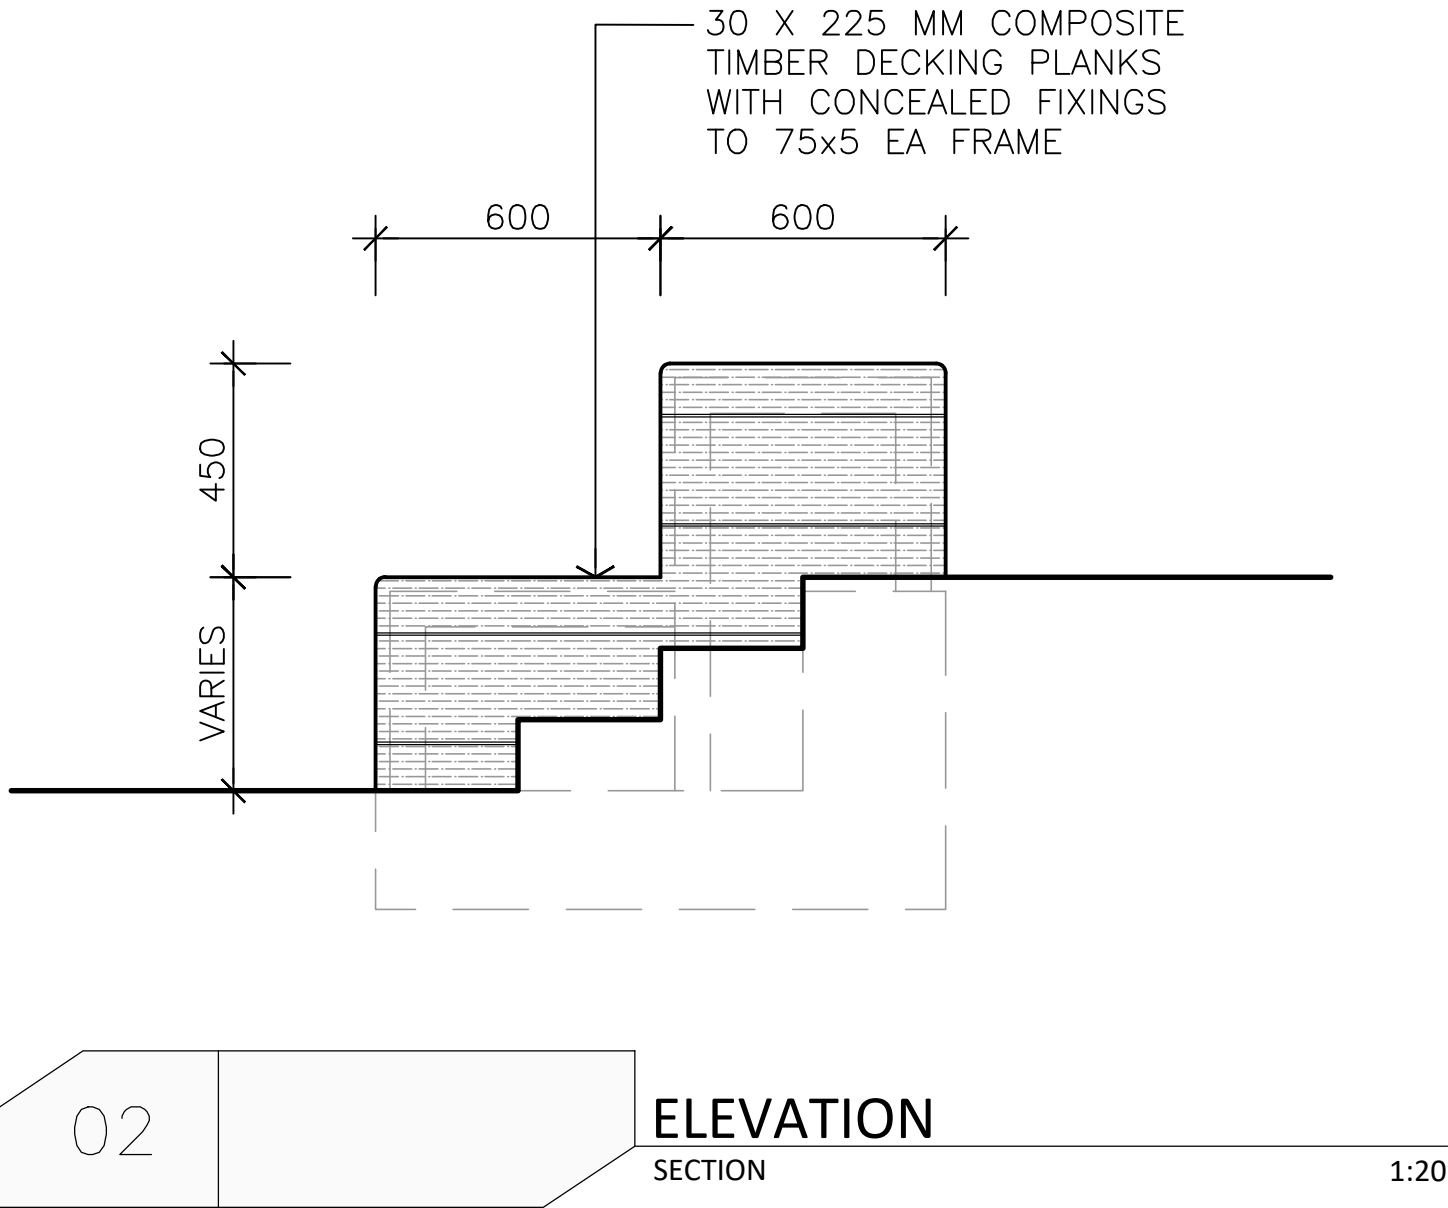

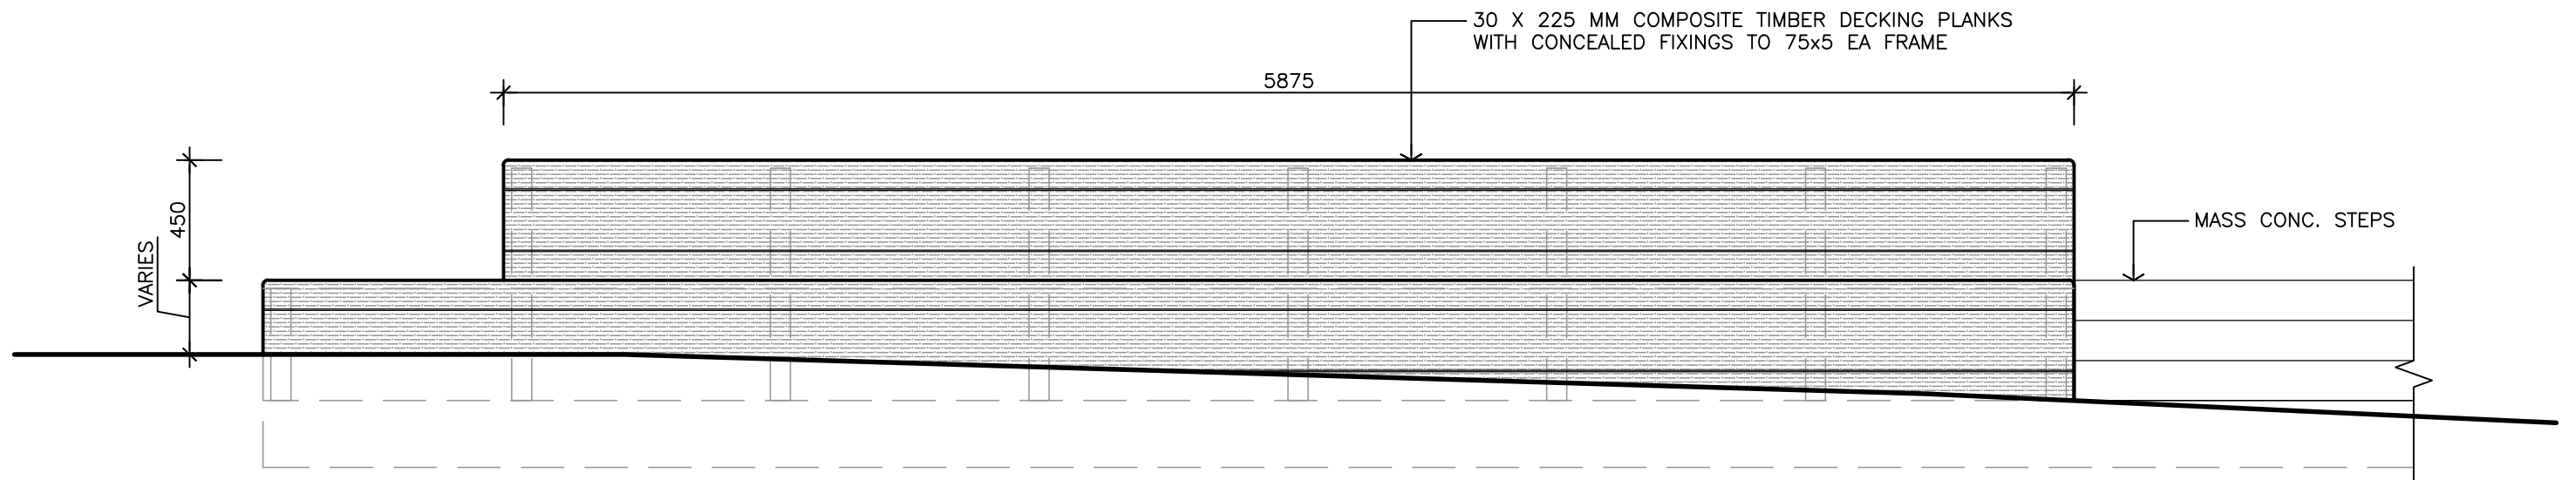








01


ELEVATION









SECTION


1:20

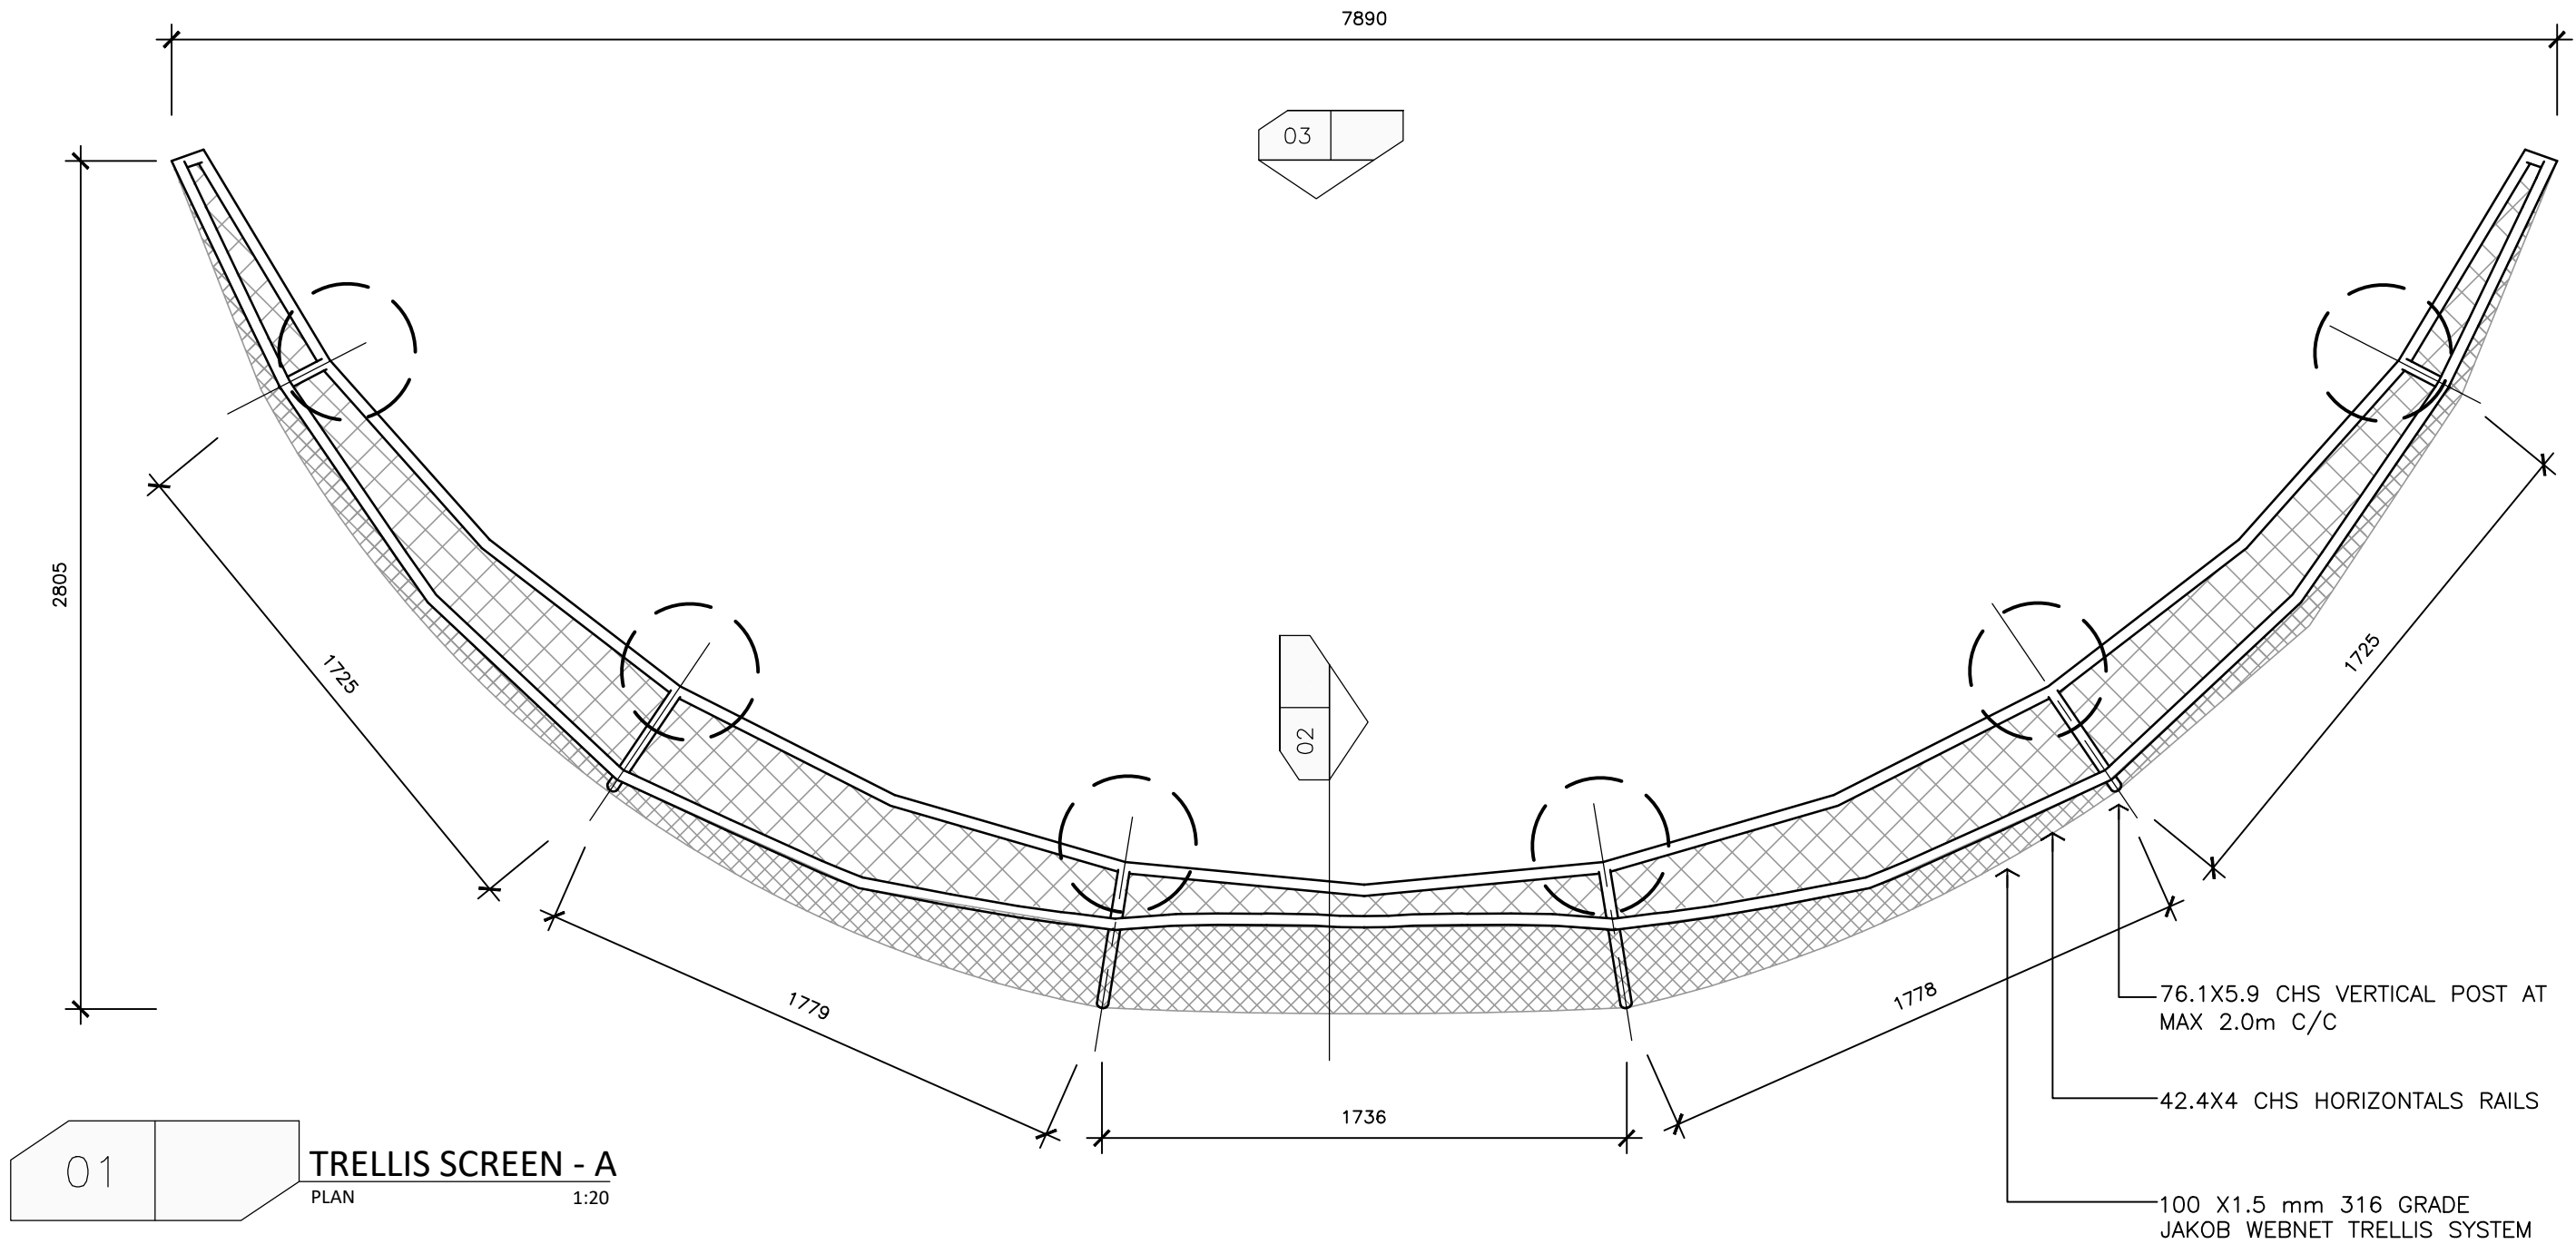

      

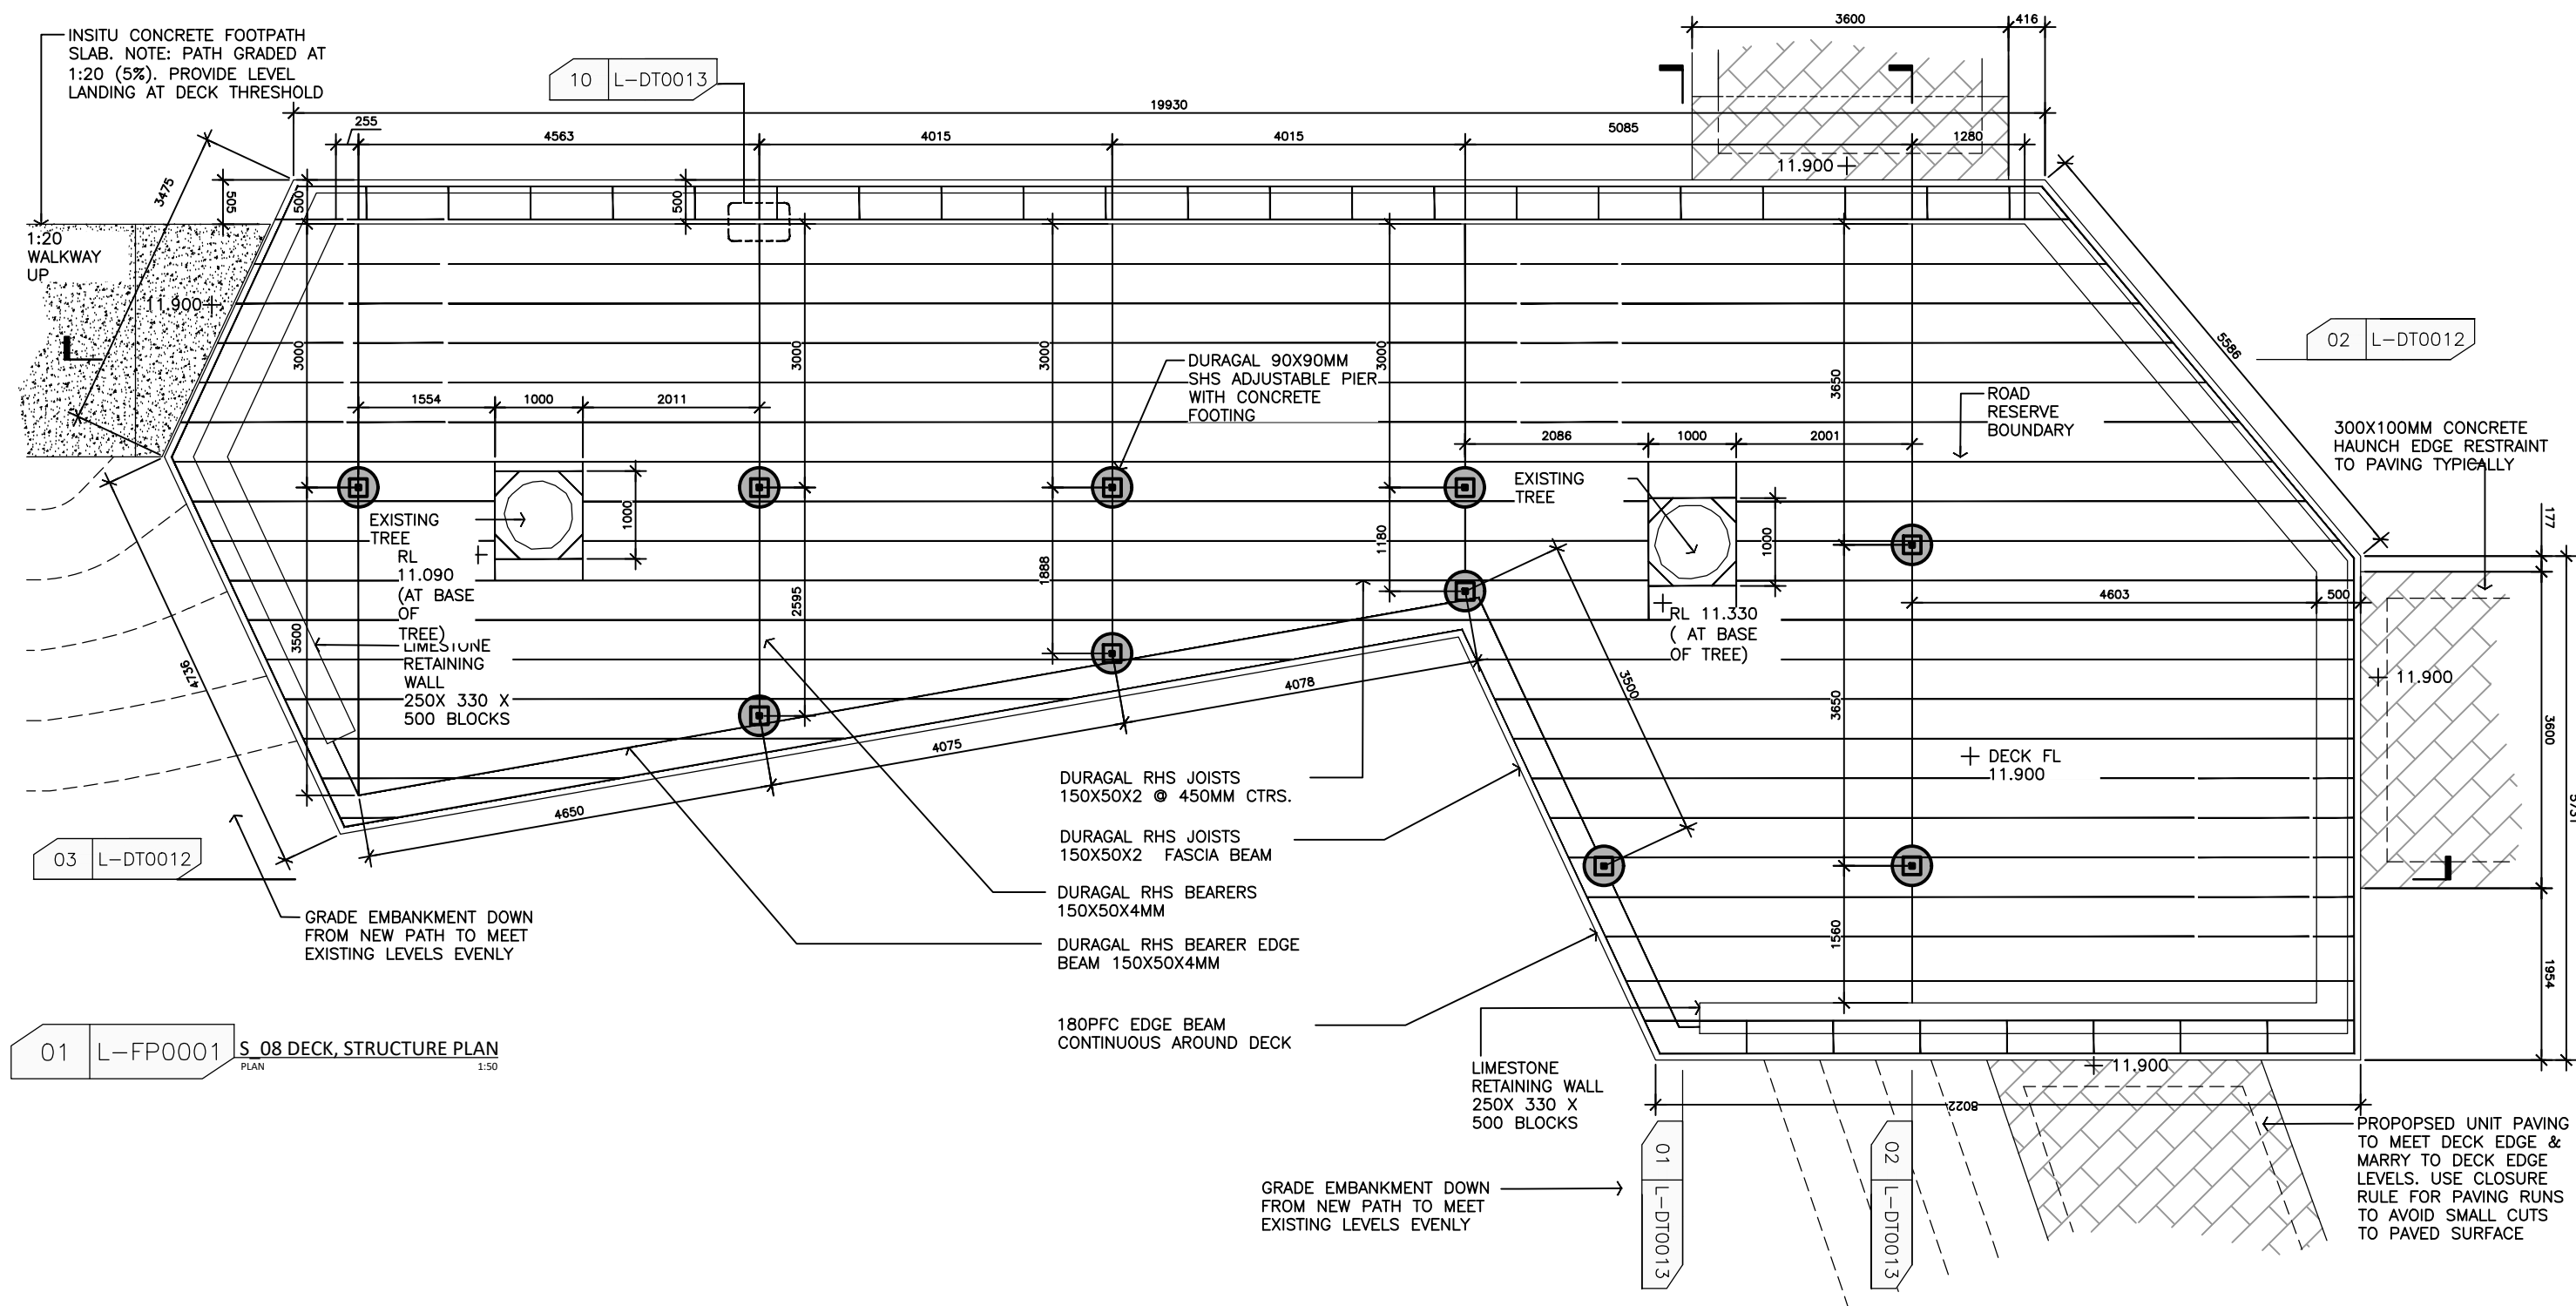

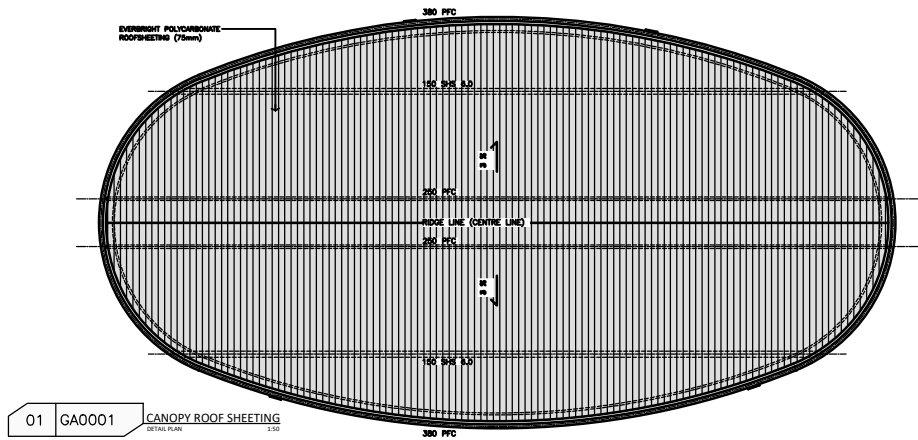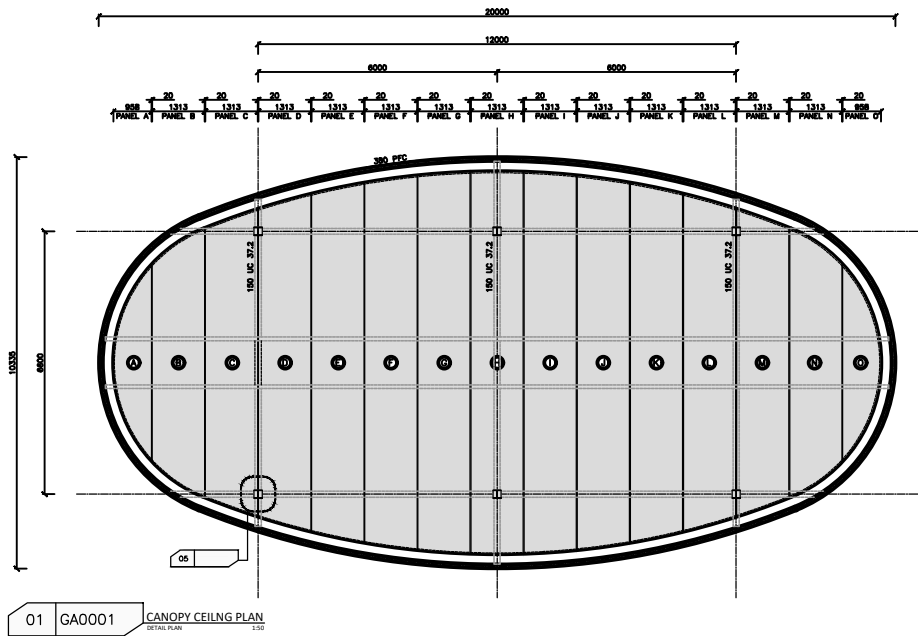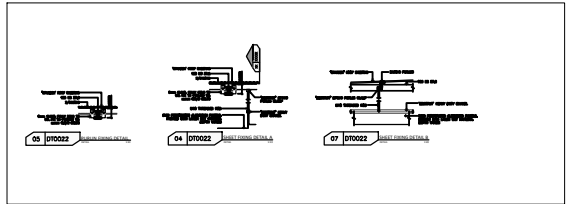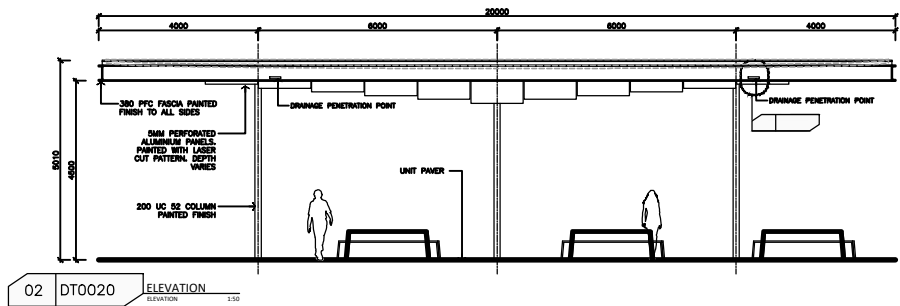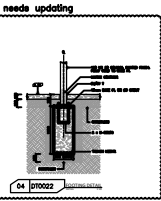
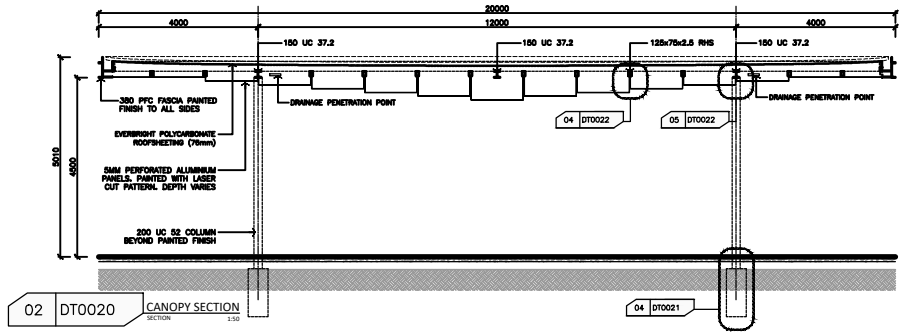
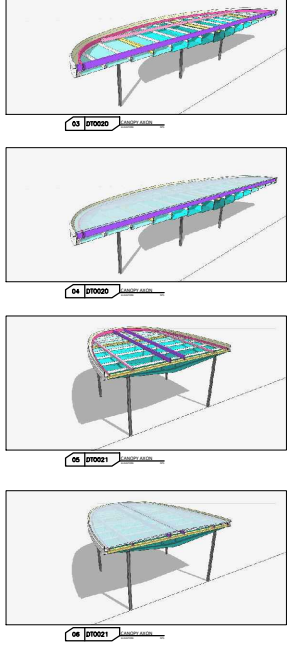
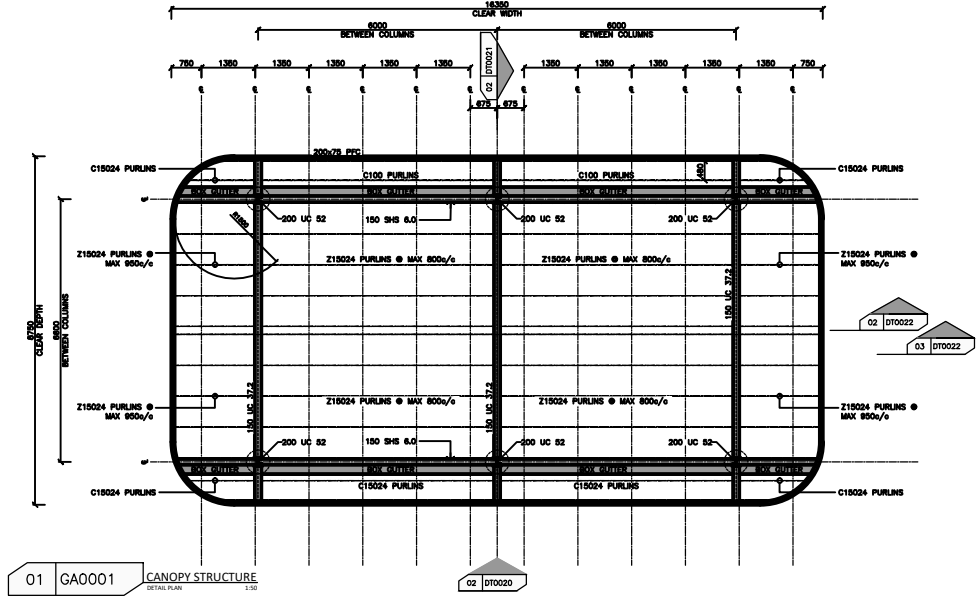


















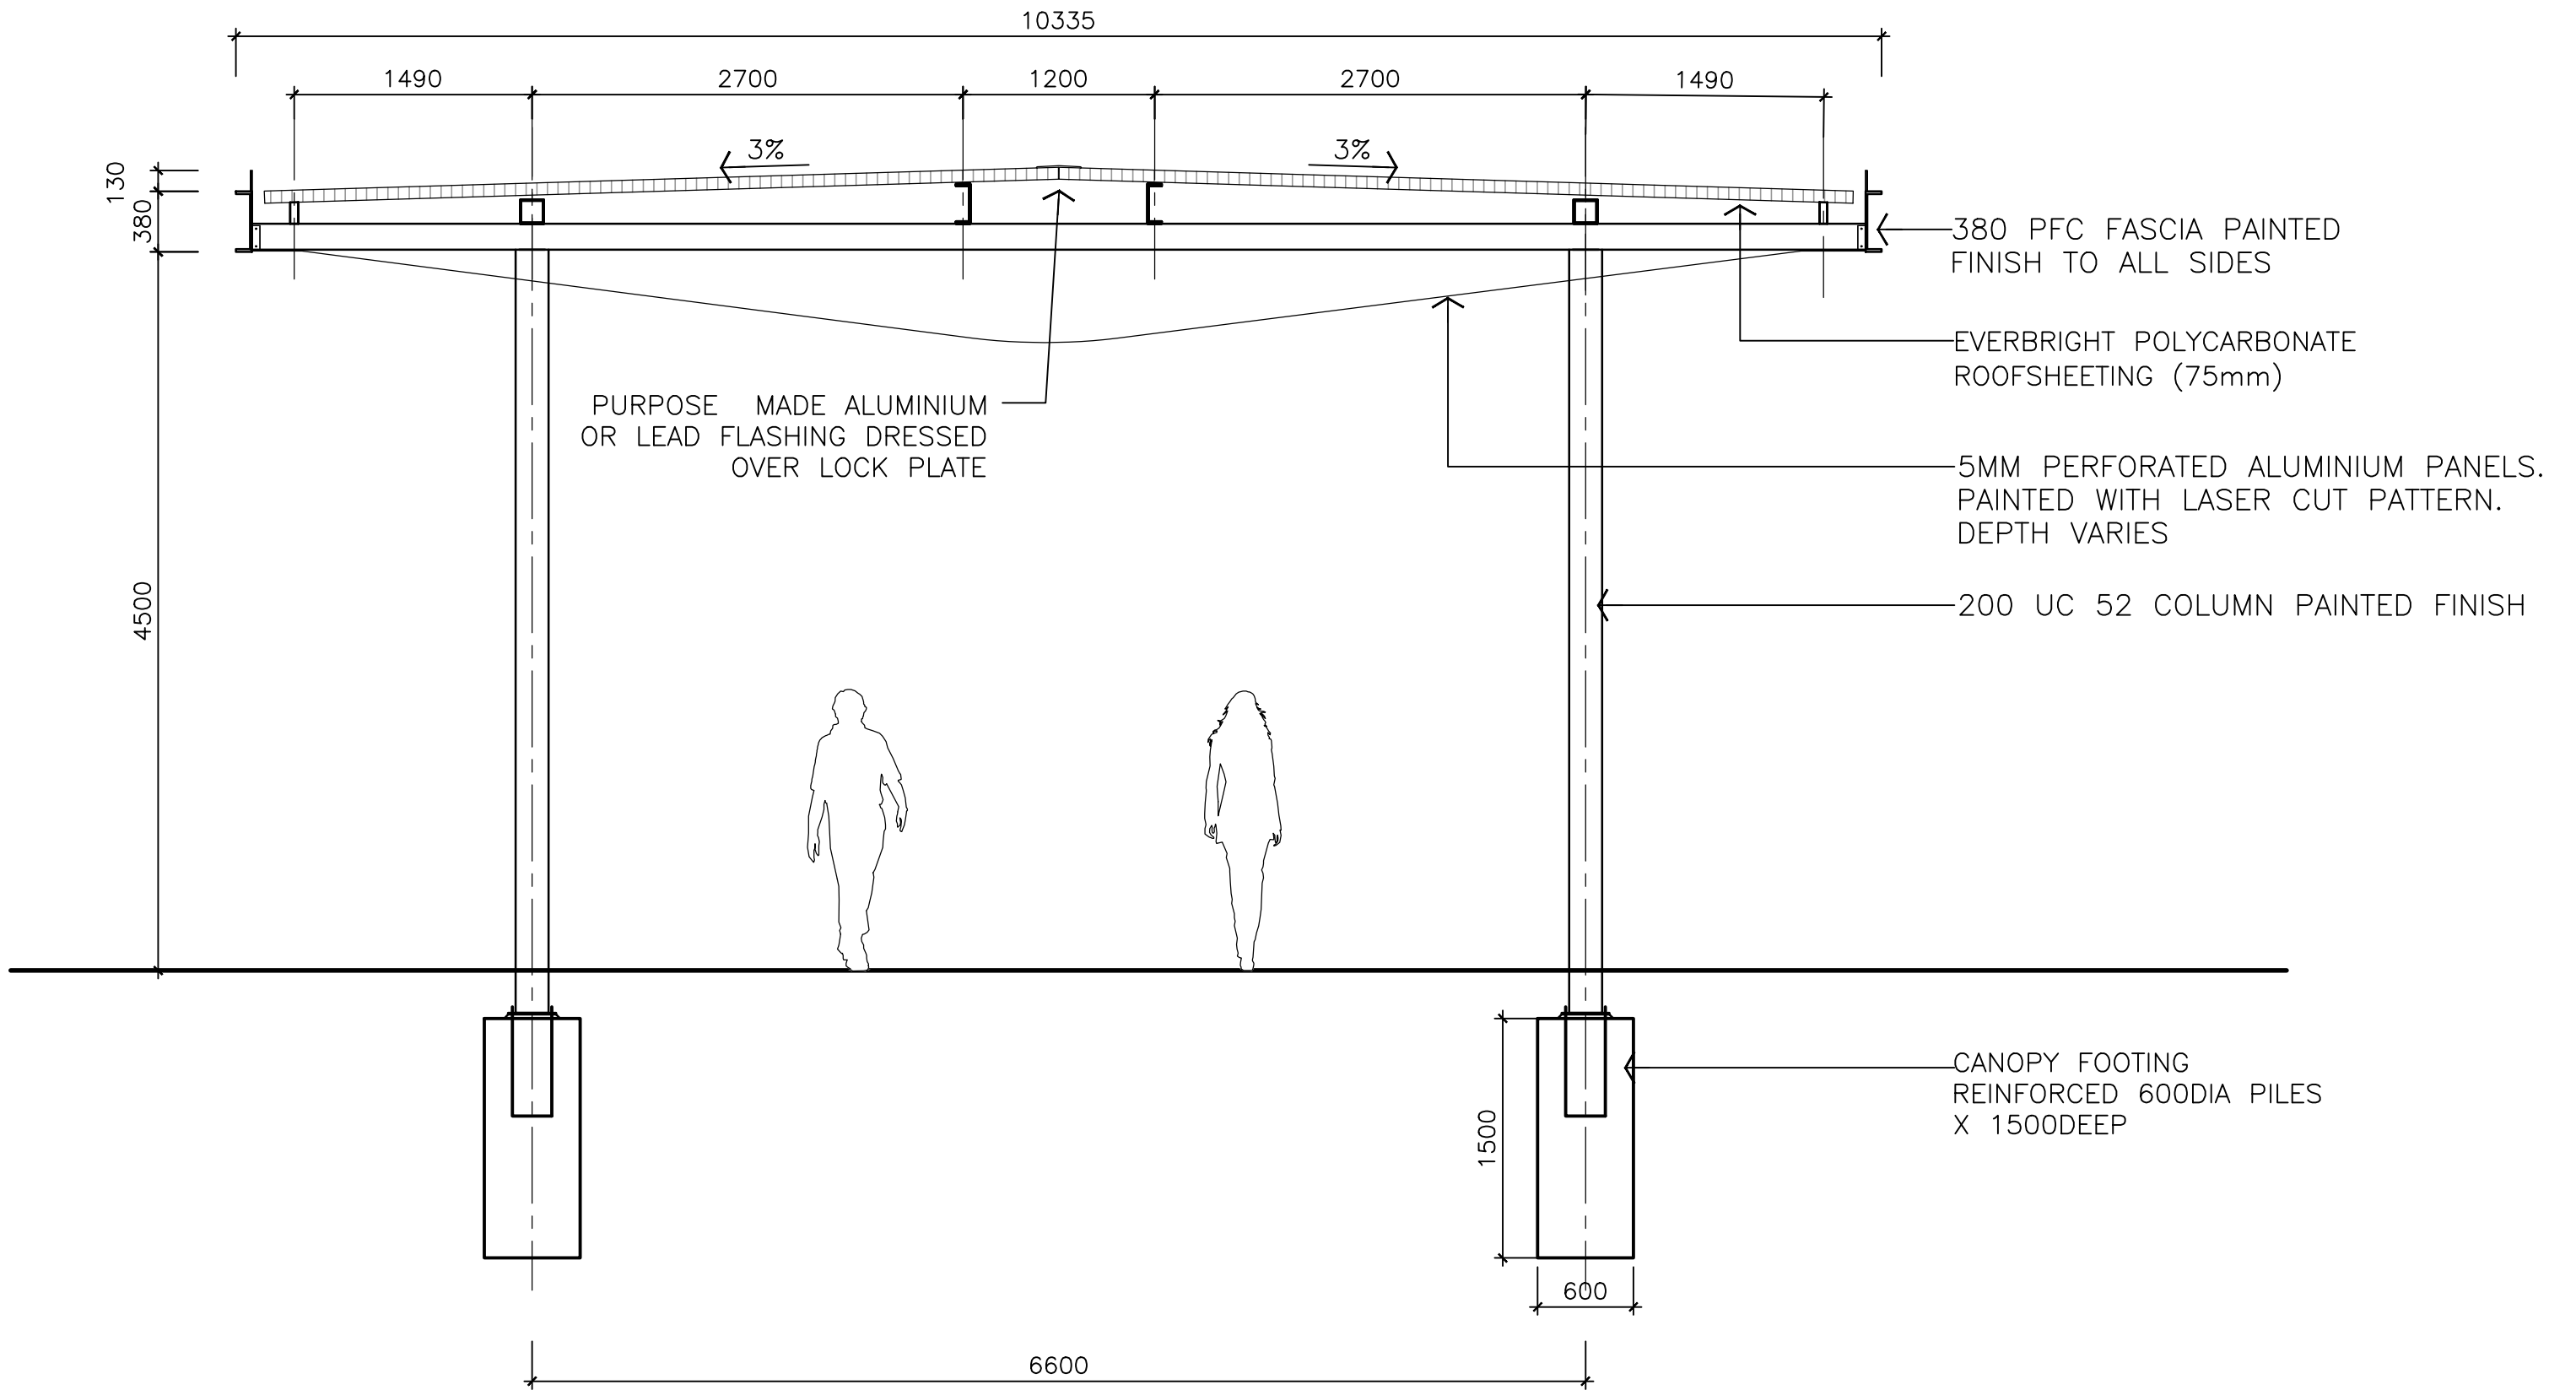



02

CANOPY SECTION

SECTION 1:50

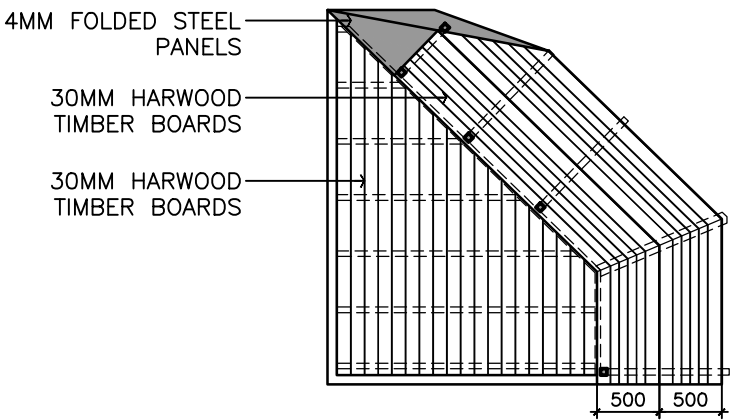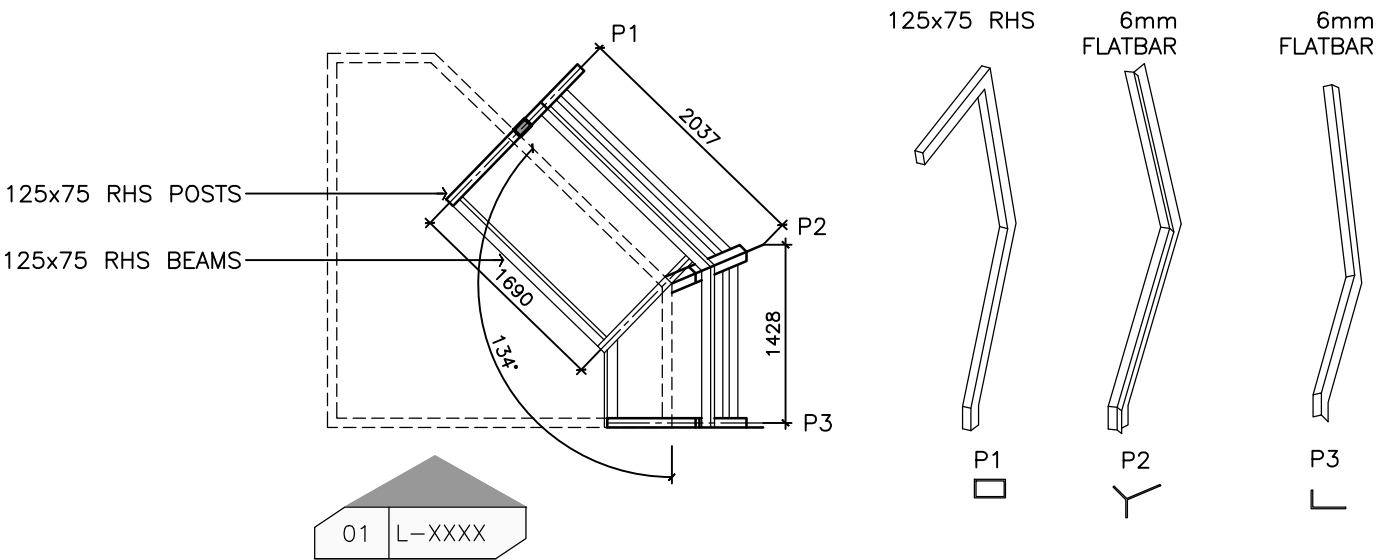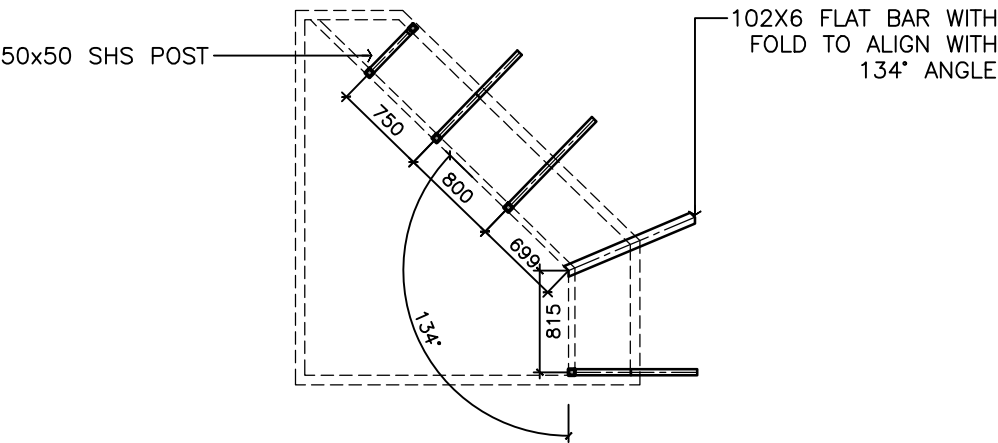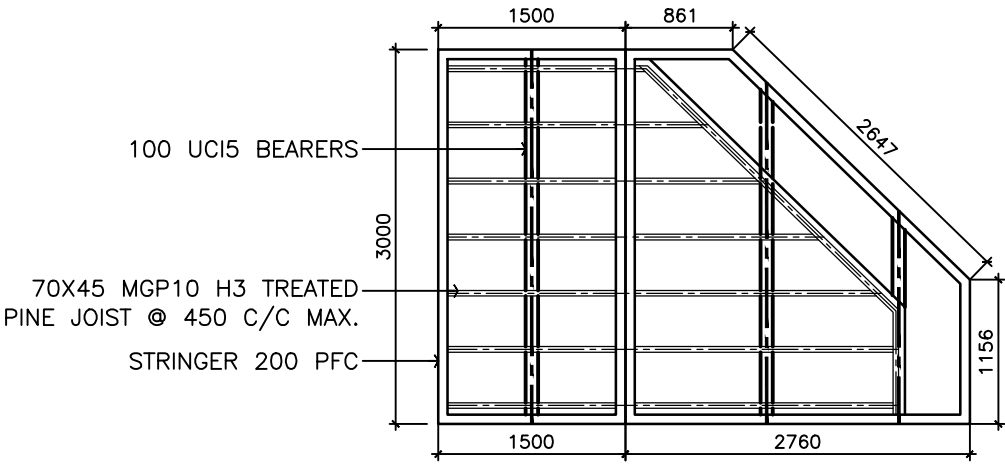

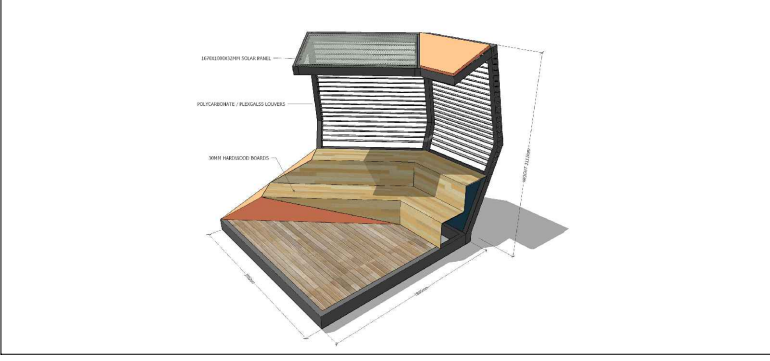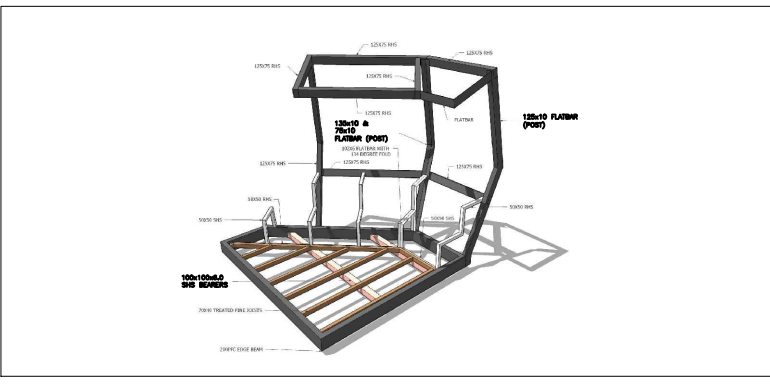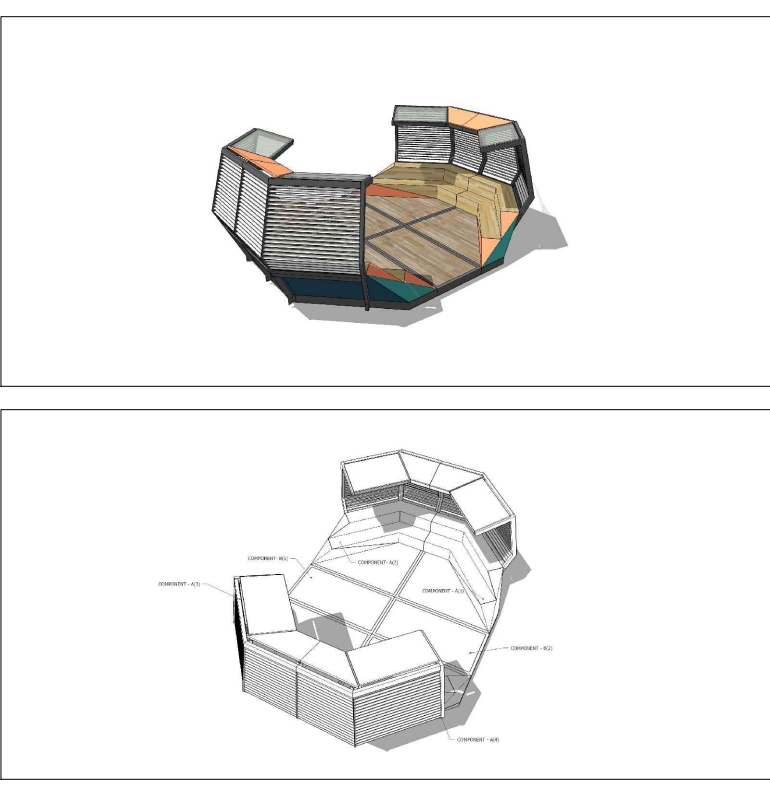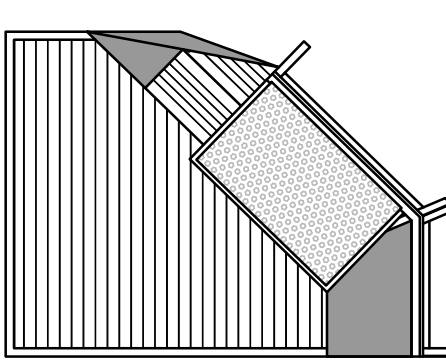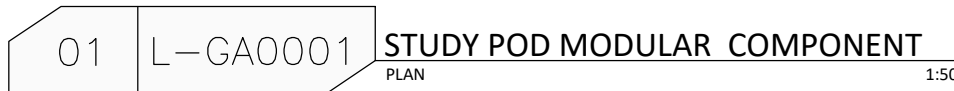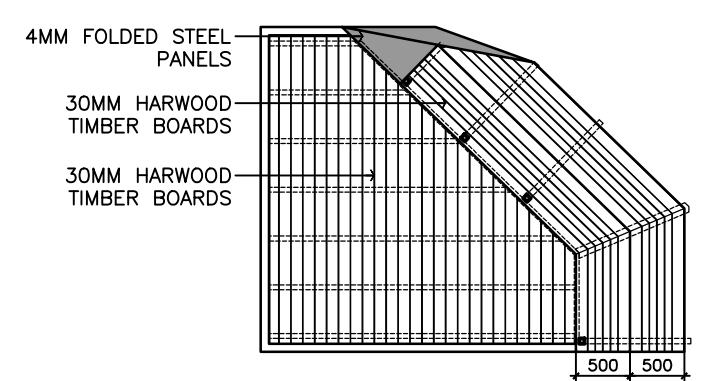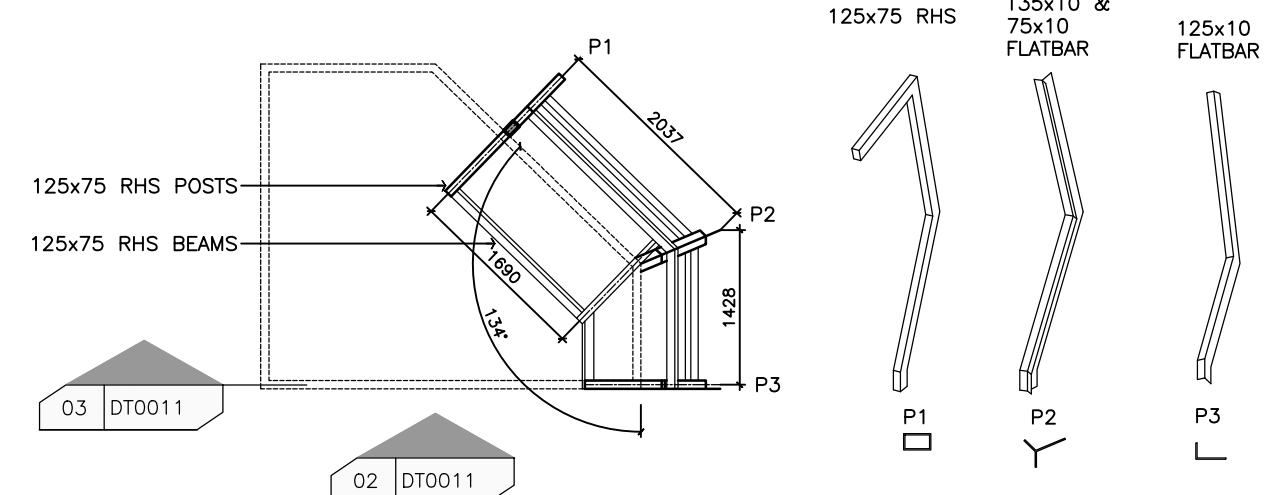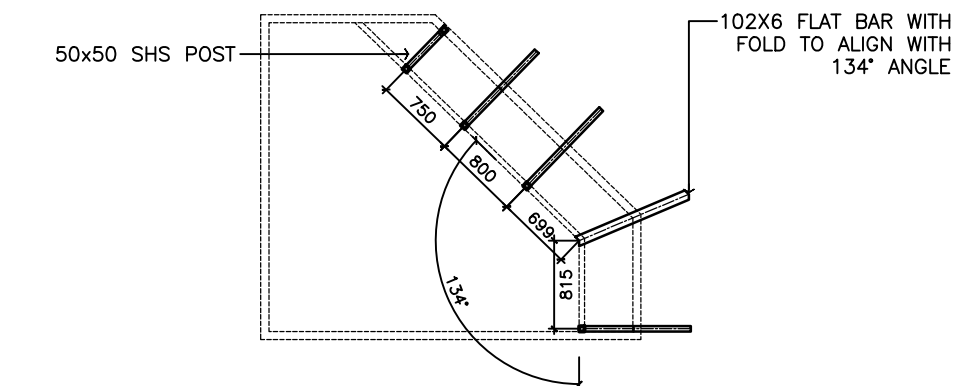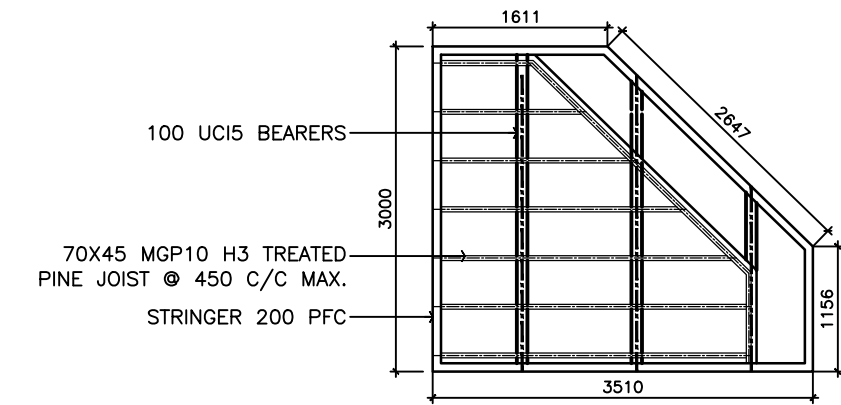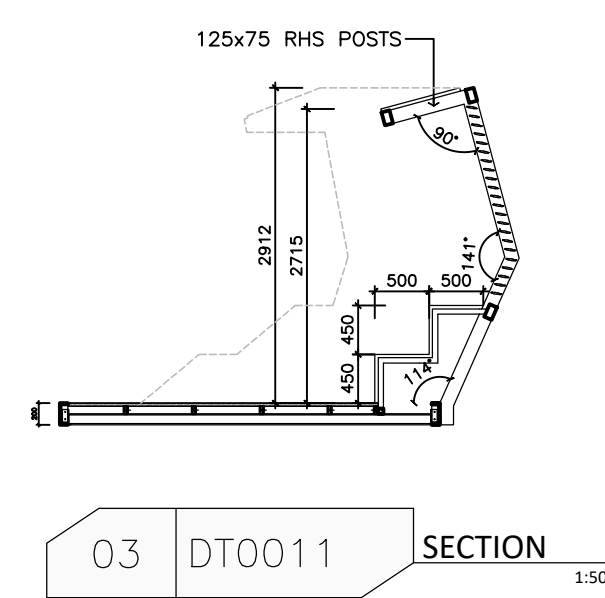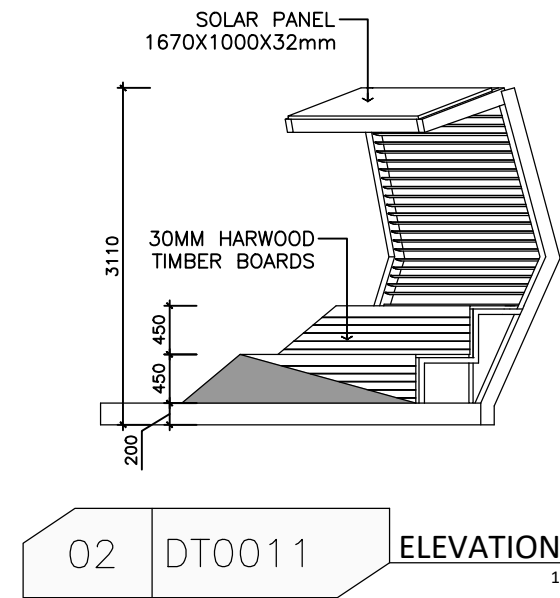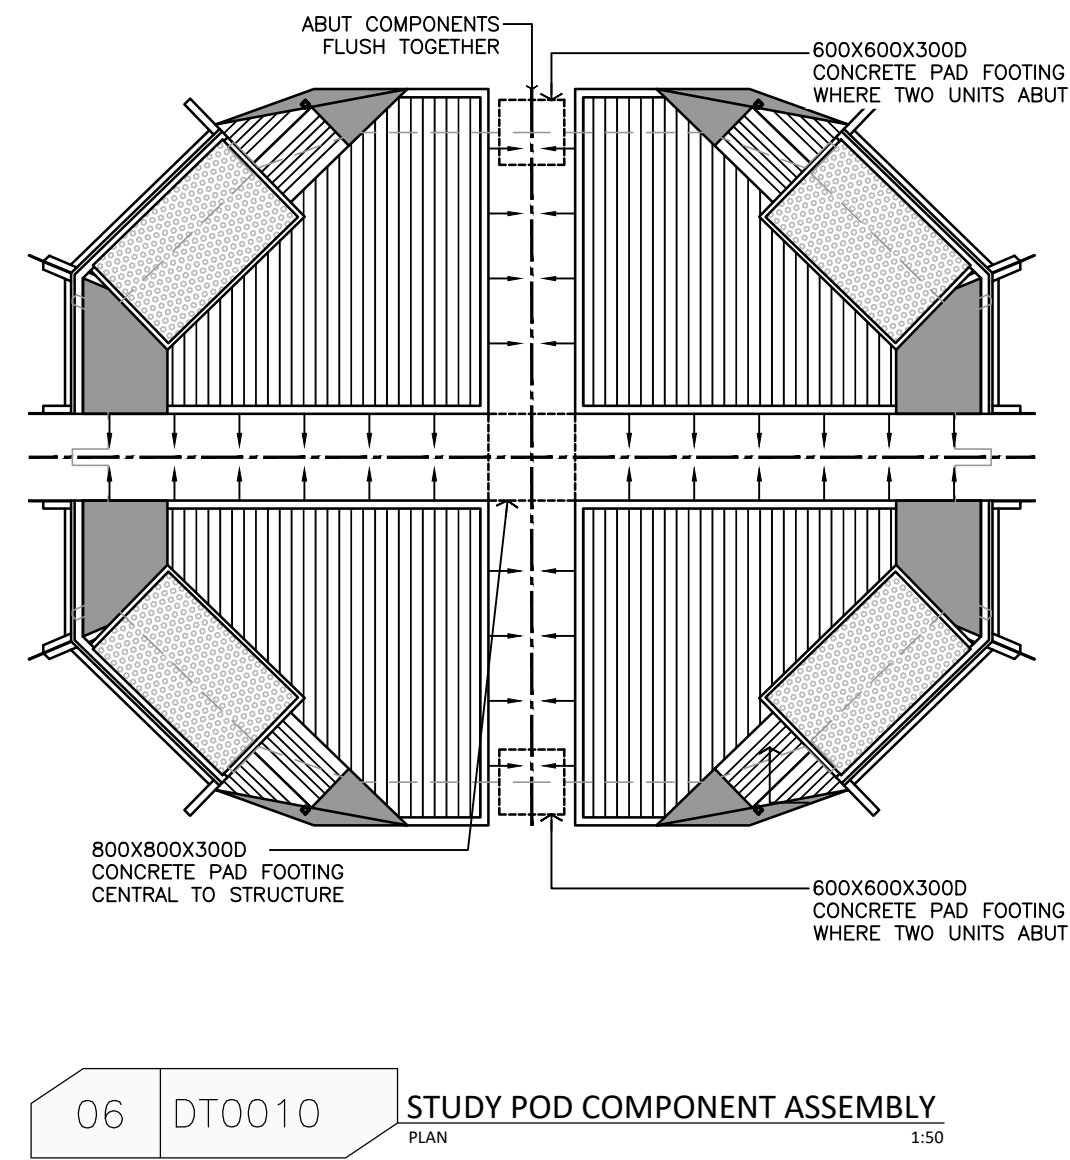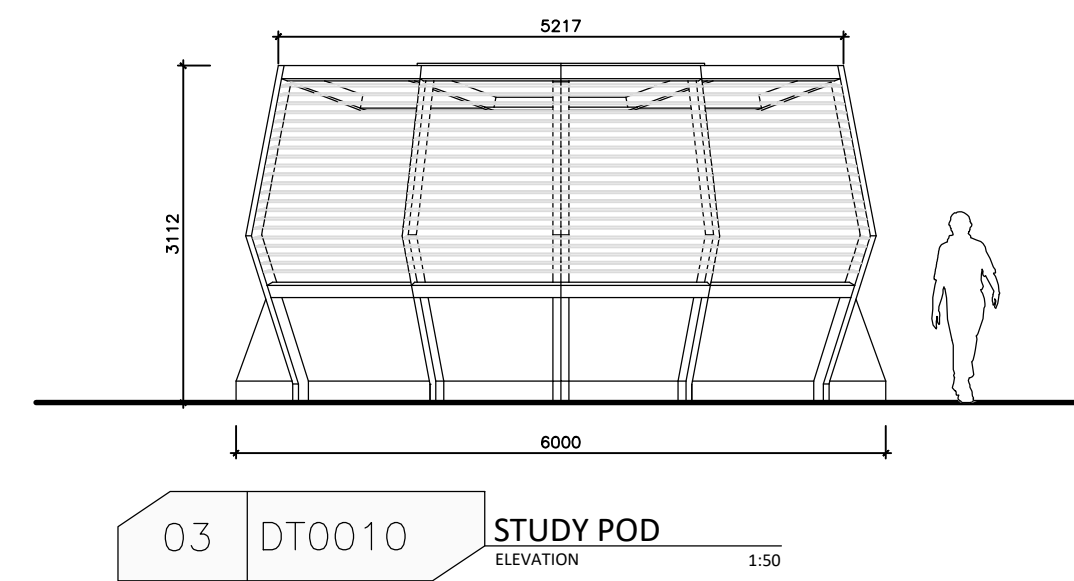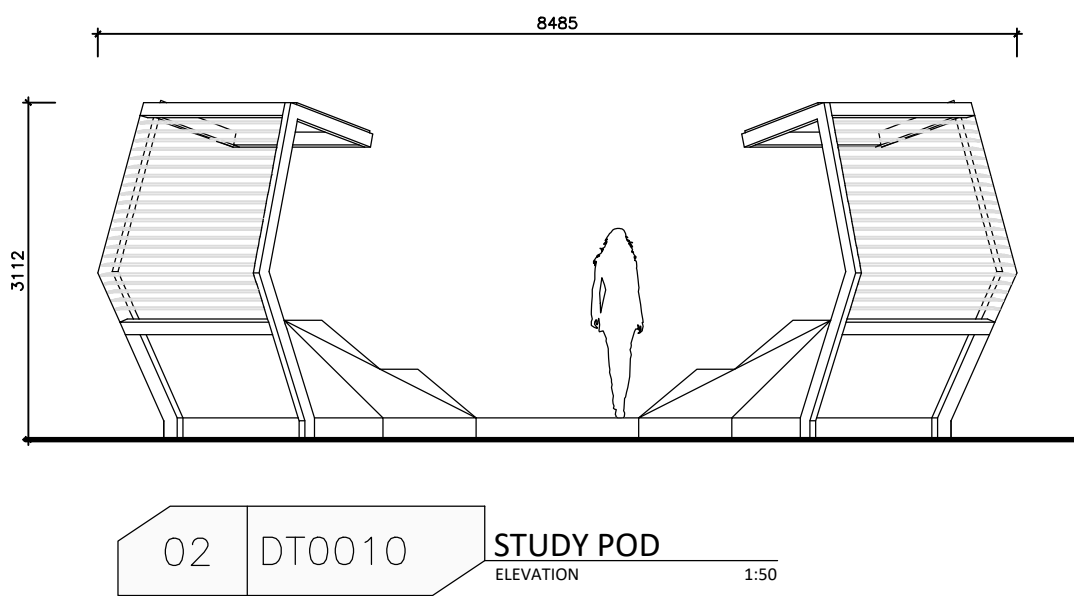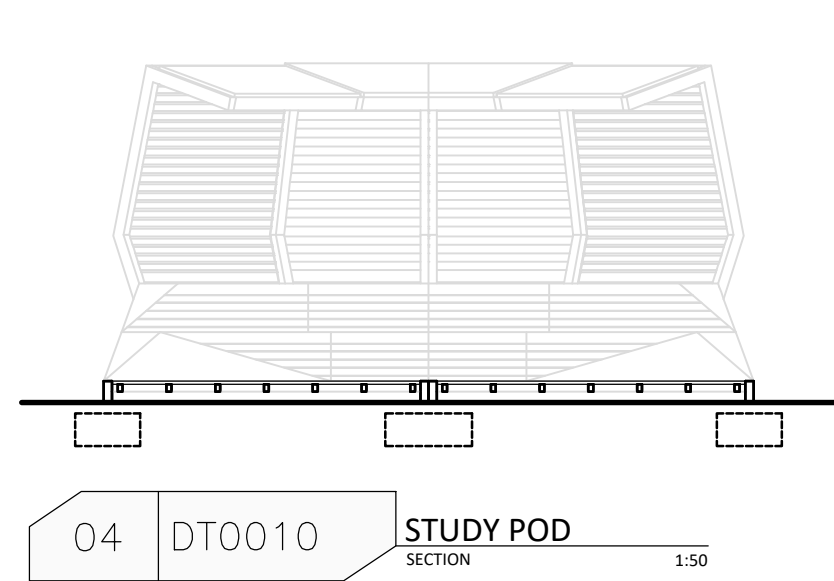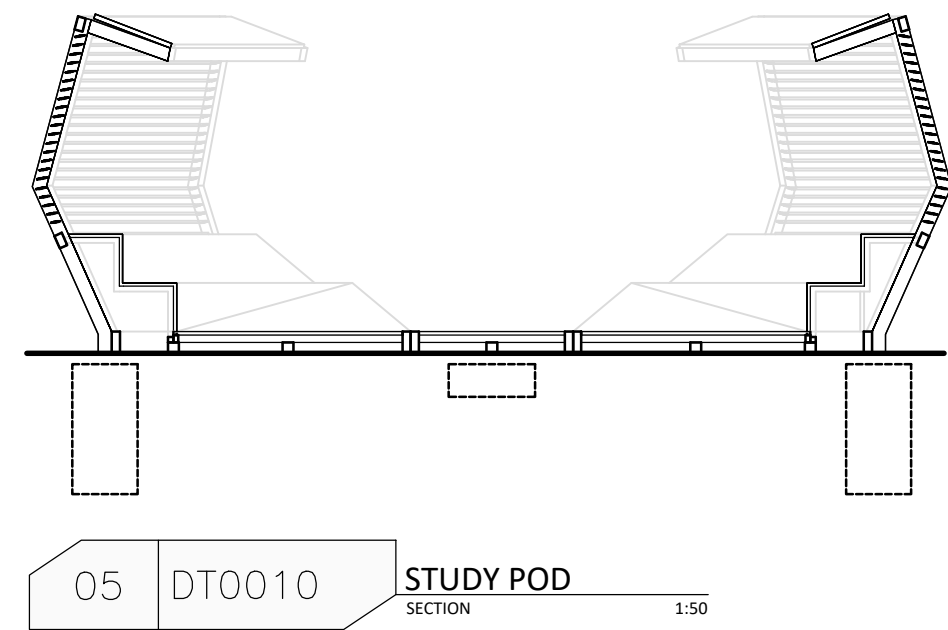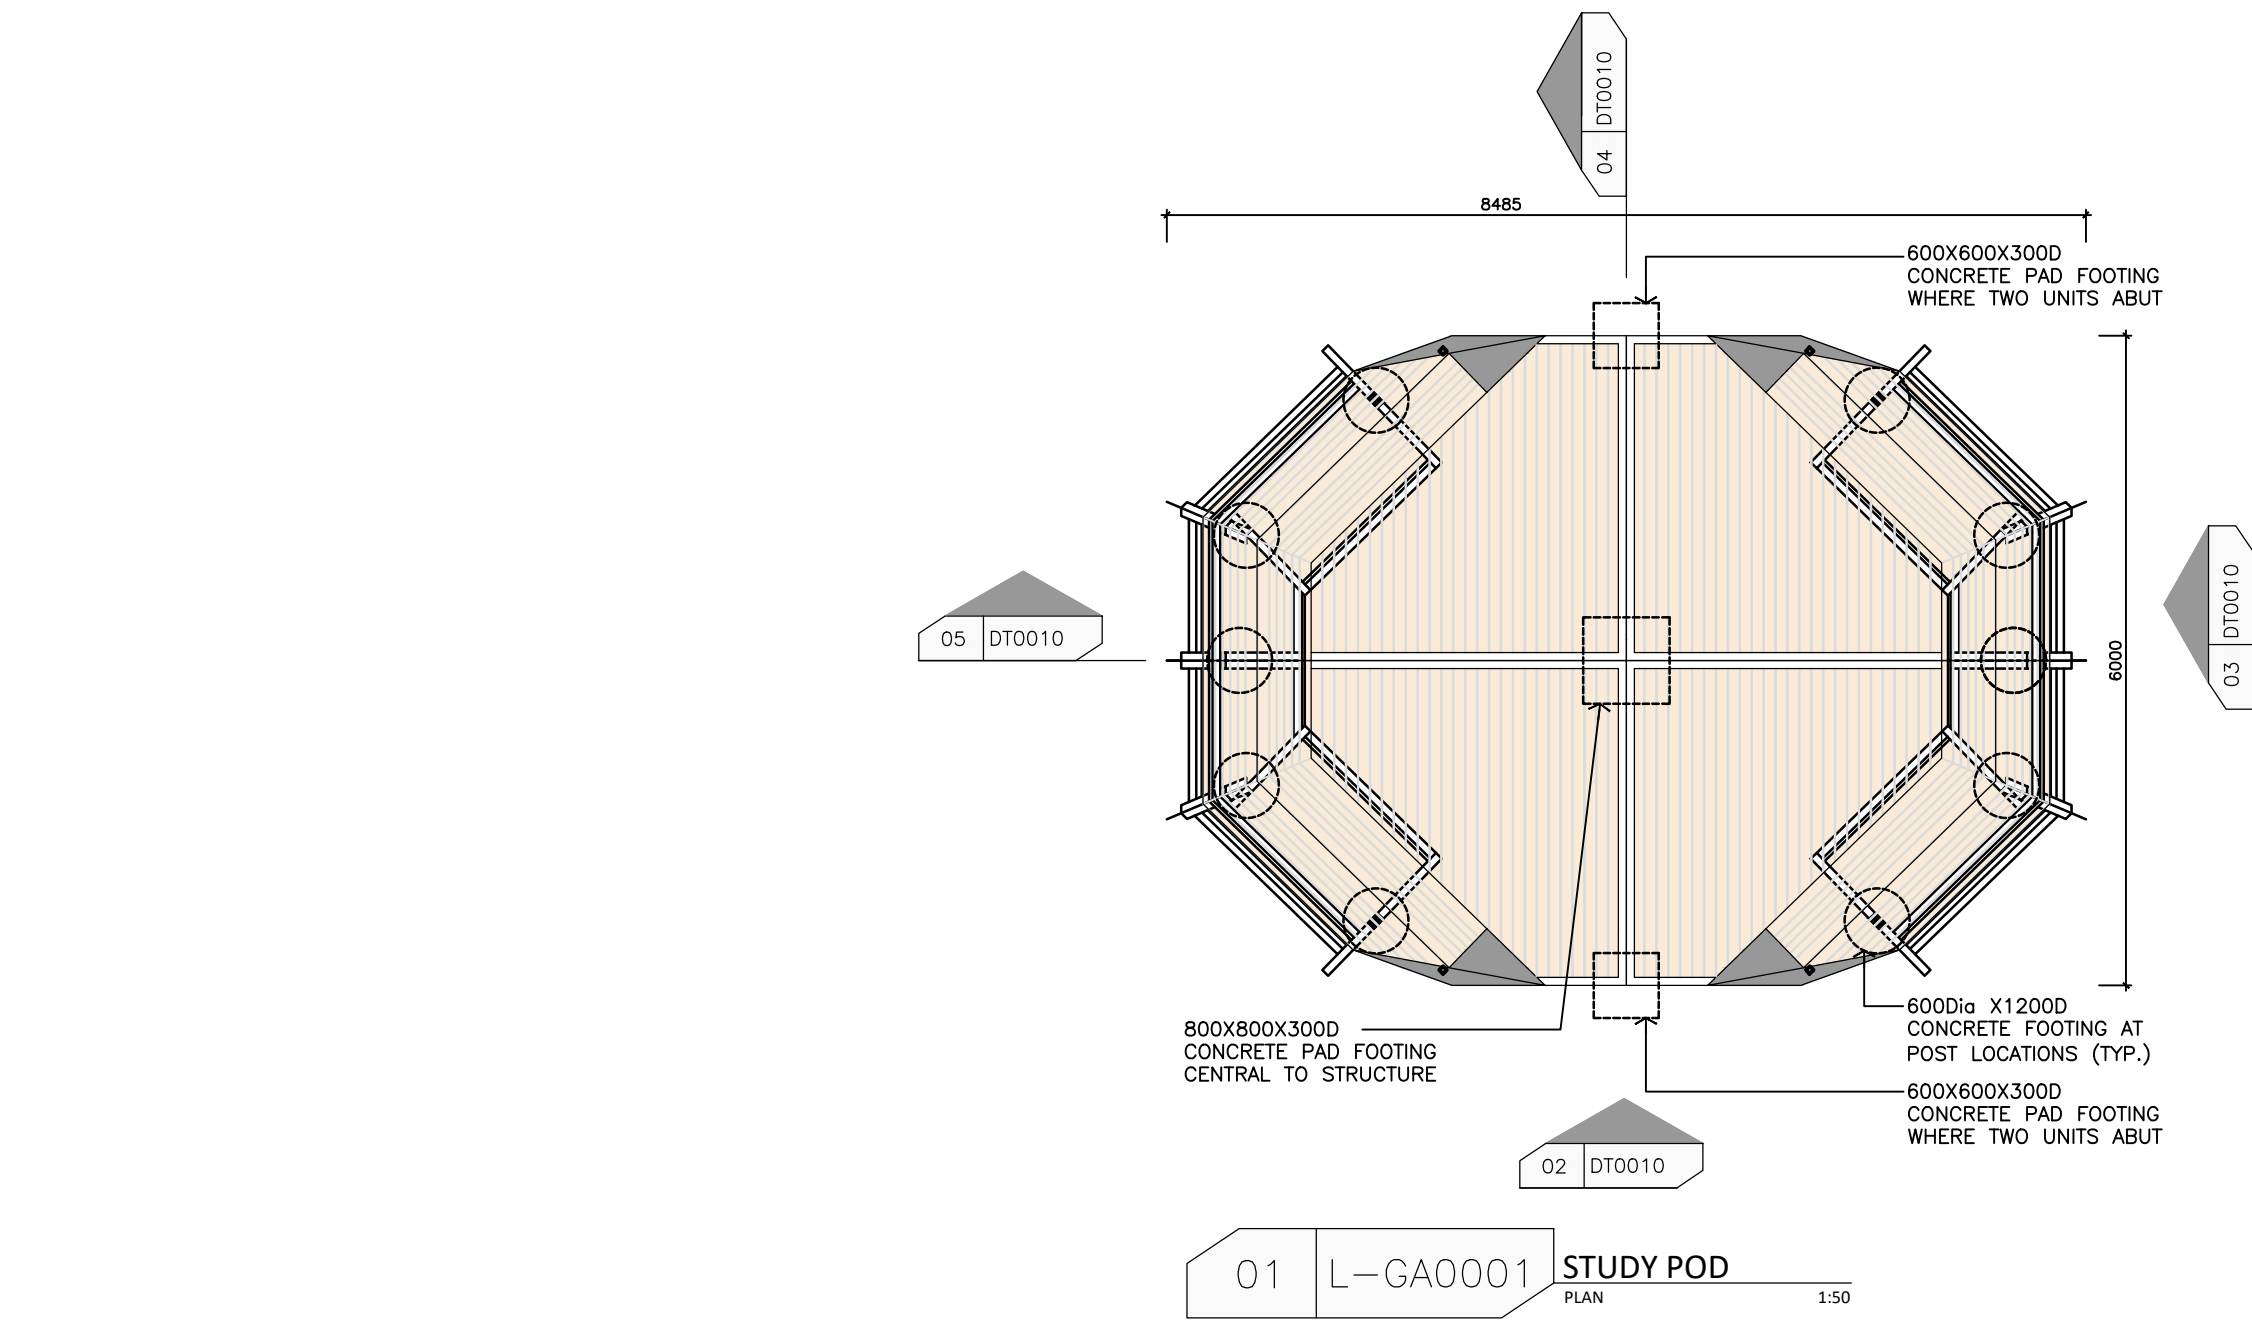

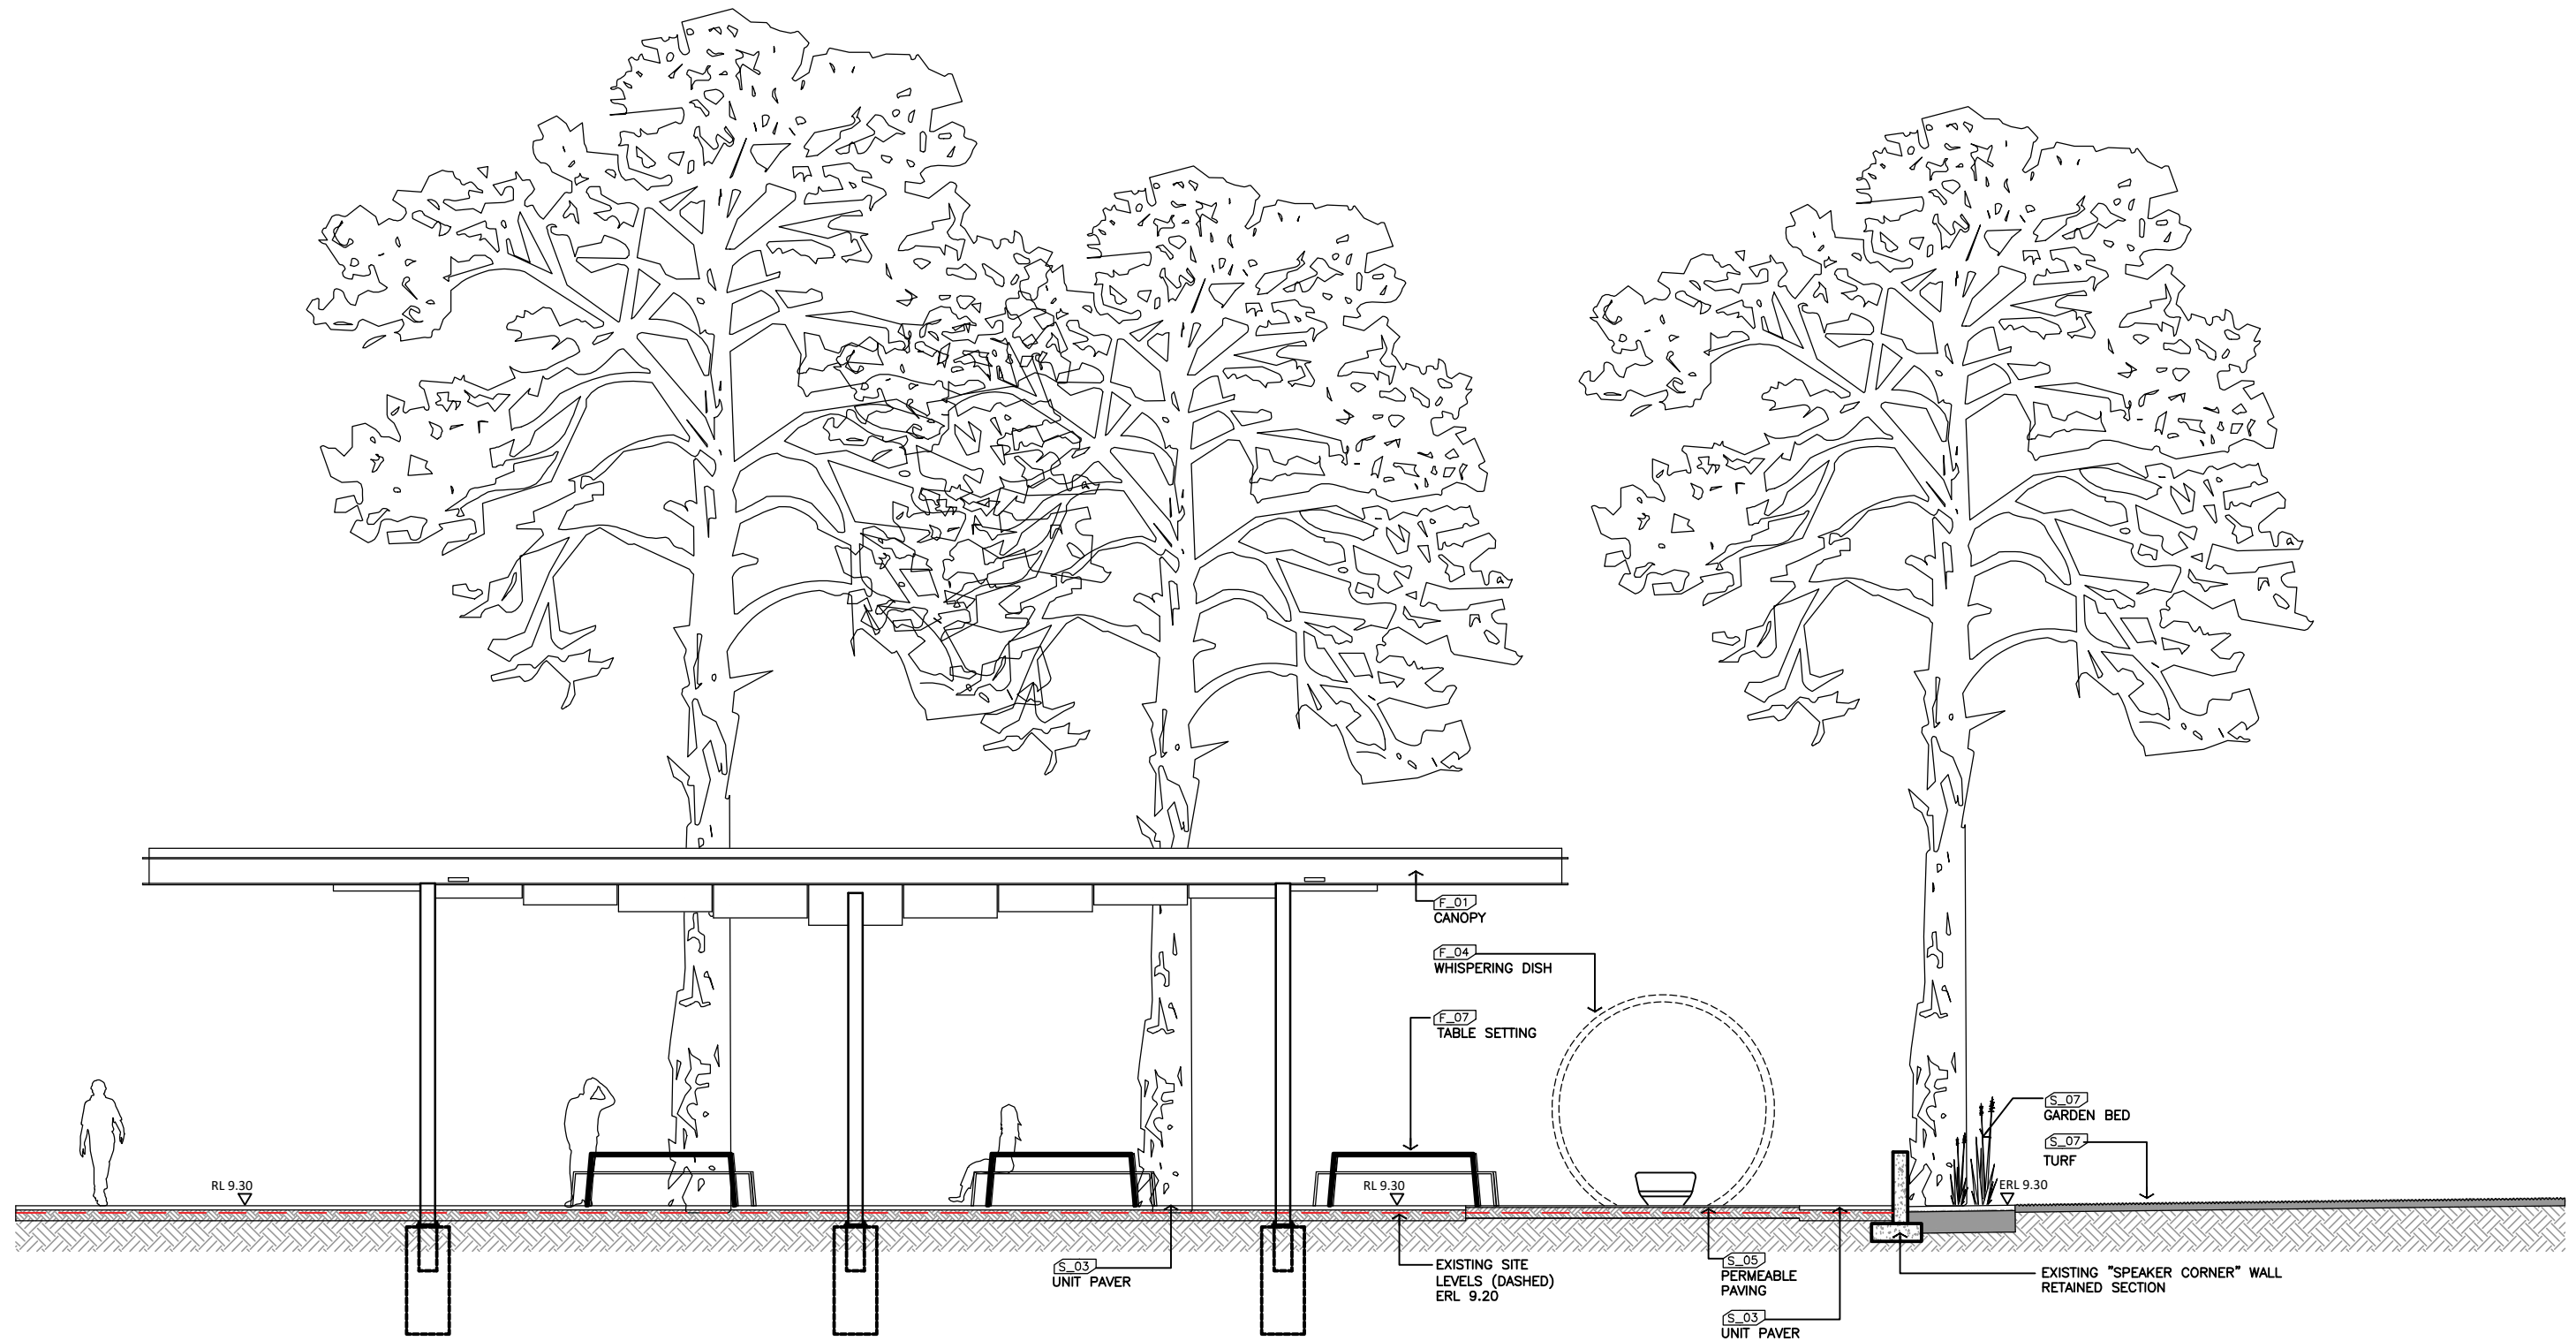

01

L-GA0001

SPEAKERS CORNER & CANOPY

SECTION

1:50




01

L-GA0001


CONTAINER GALLERY

SECTION


1:50

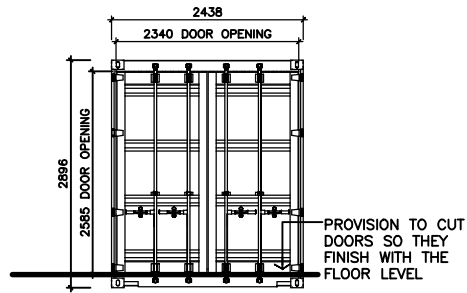


07 DT0040 REAR ELEVATION - SOUTH
ELEVATION 1:50

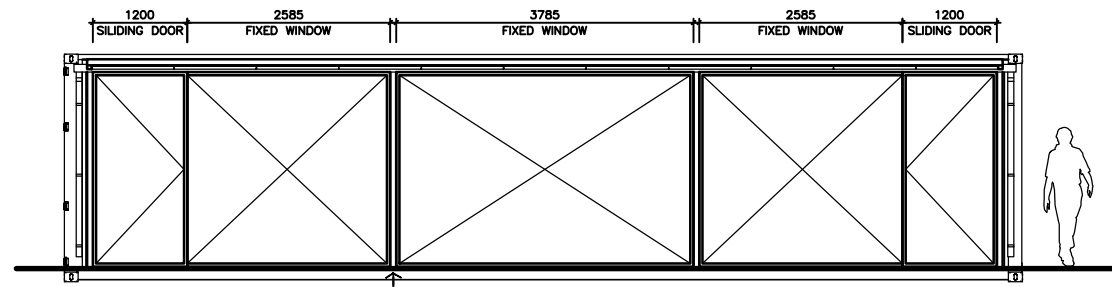


04 DT0040 SIDE ELEVATION - EAST
ELEVATION 1:50

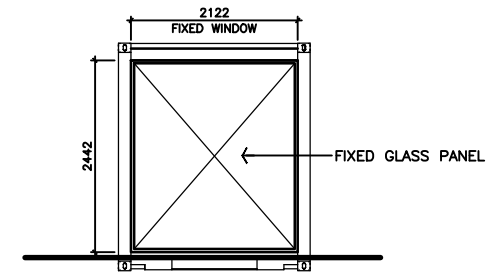



06 DT0040 FRONT ELEVATION - NORTH
ELEVATION 1:50

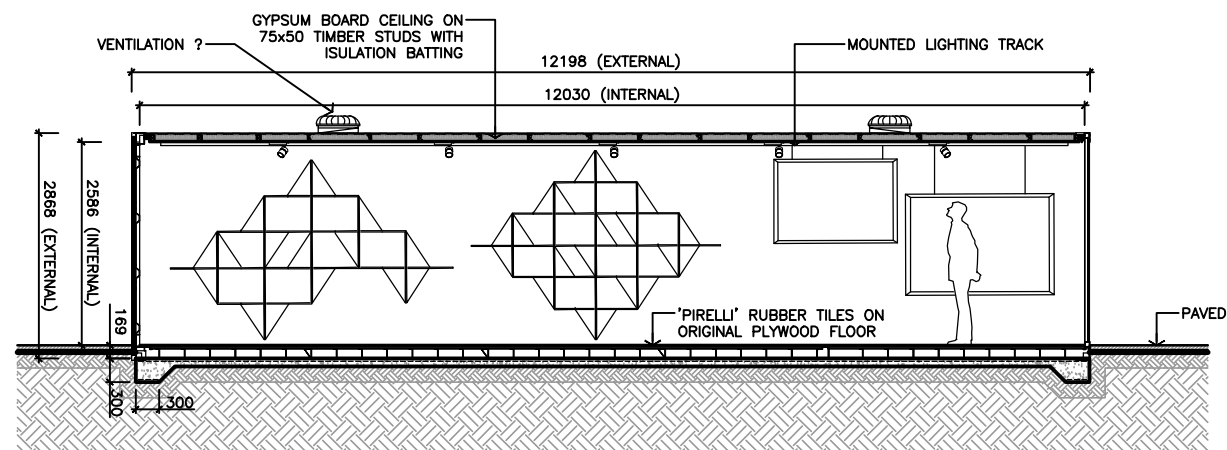


05 DT0040 SECTION
1:50

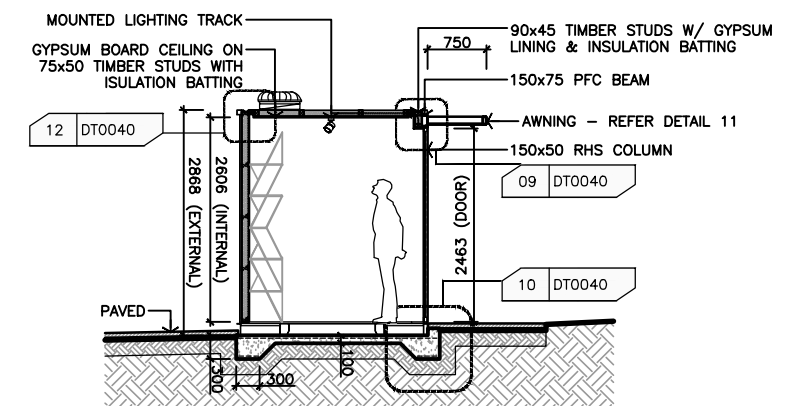


08 DT0040 SECTION
1:50

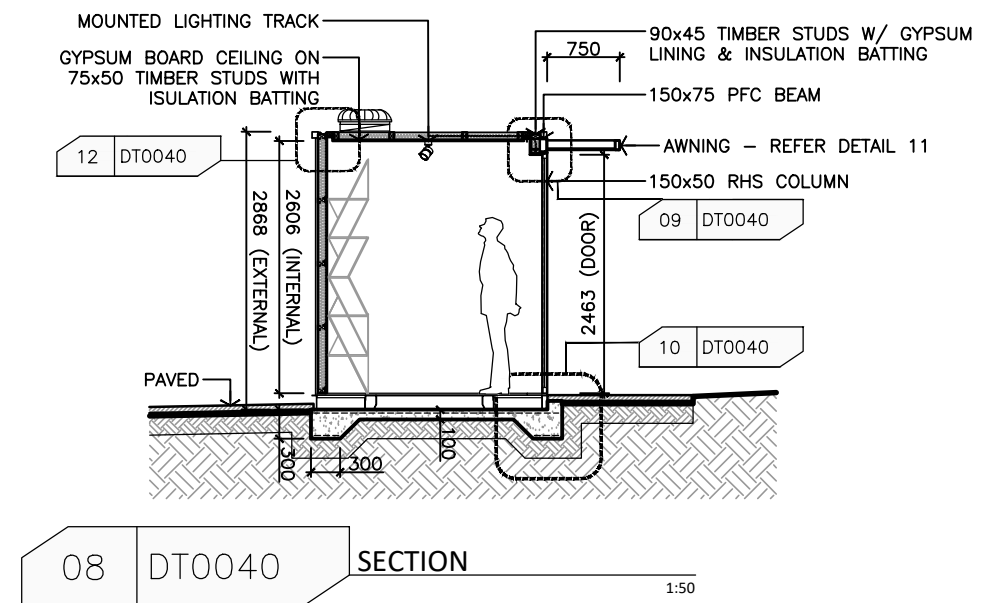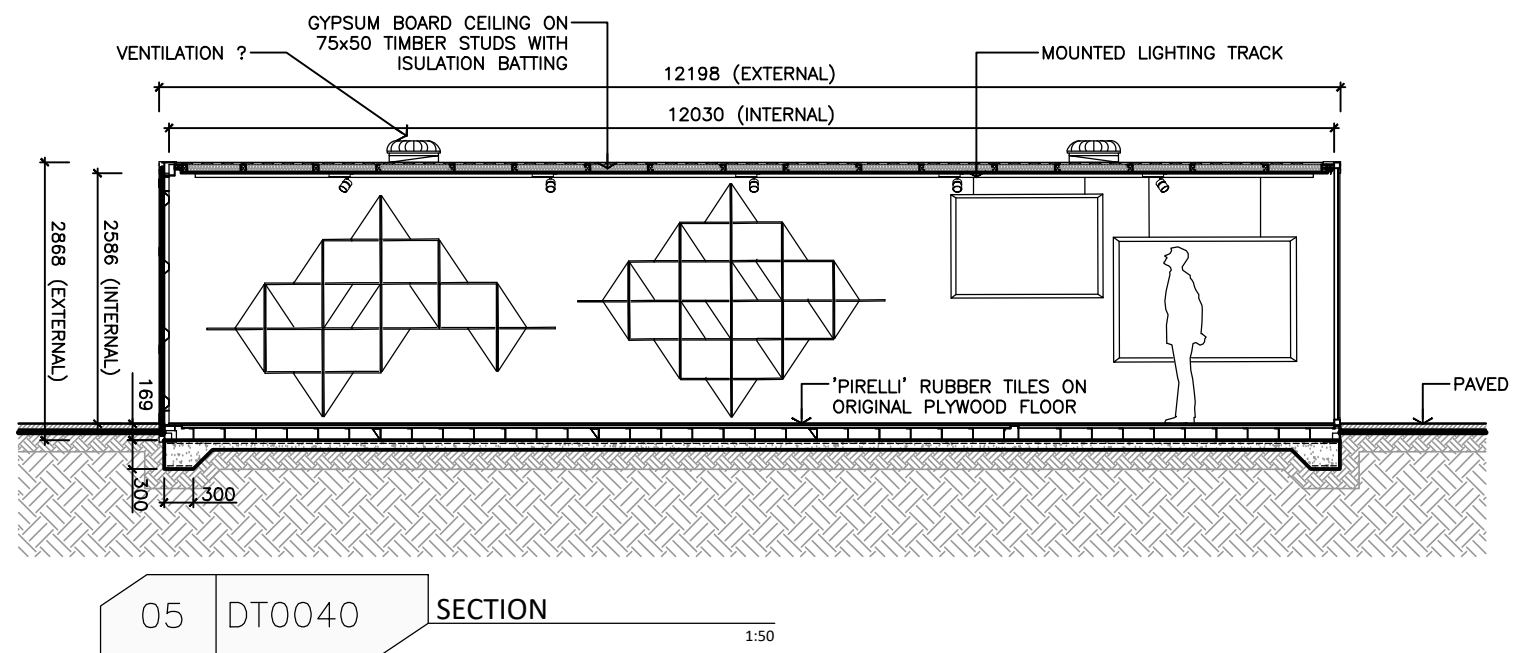


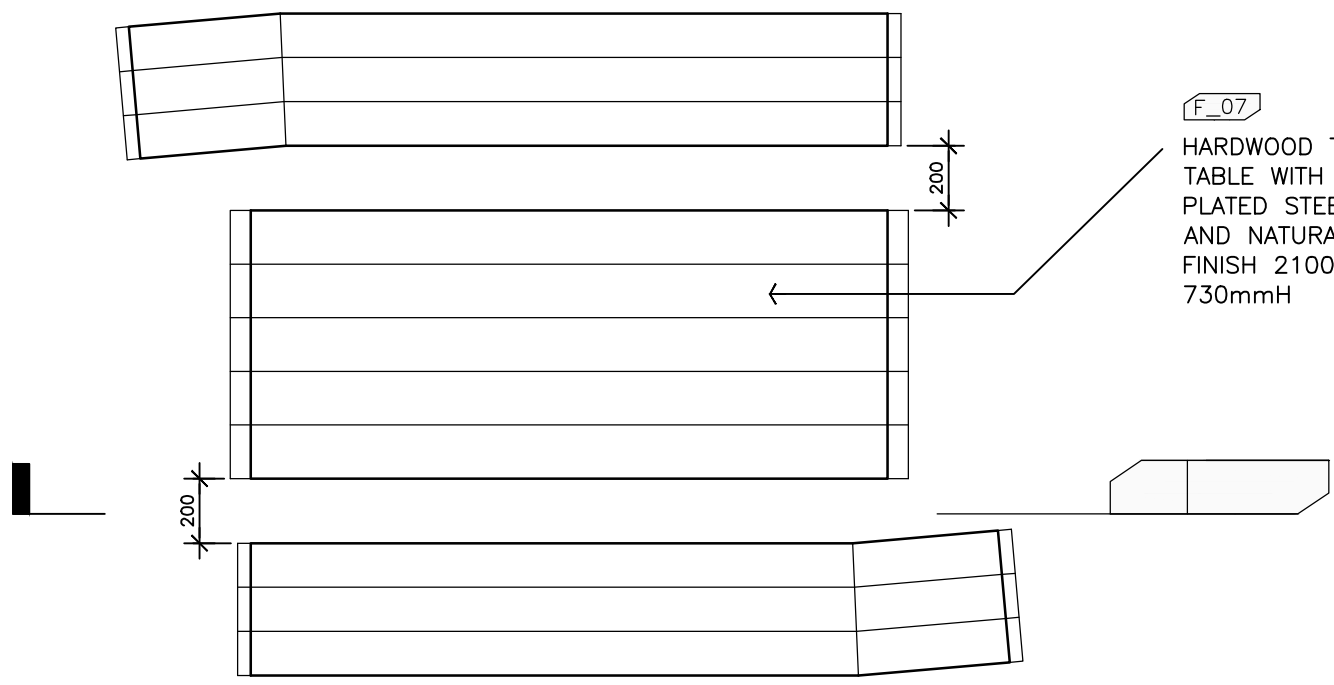

F_03 TIMBER TABLE AND BENCHES
PLAN
1:20

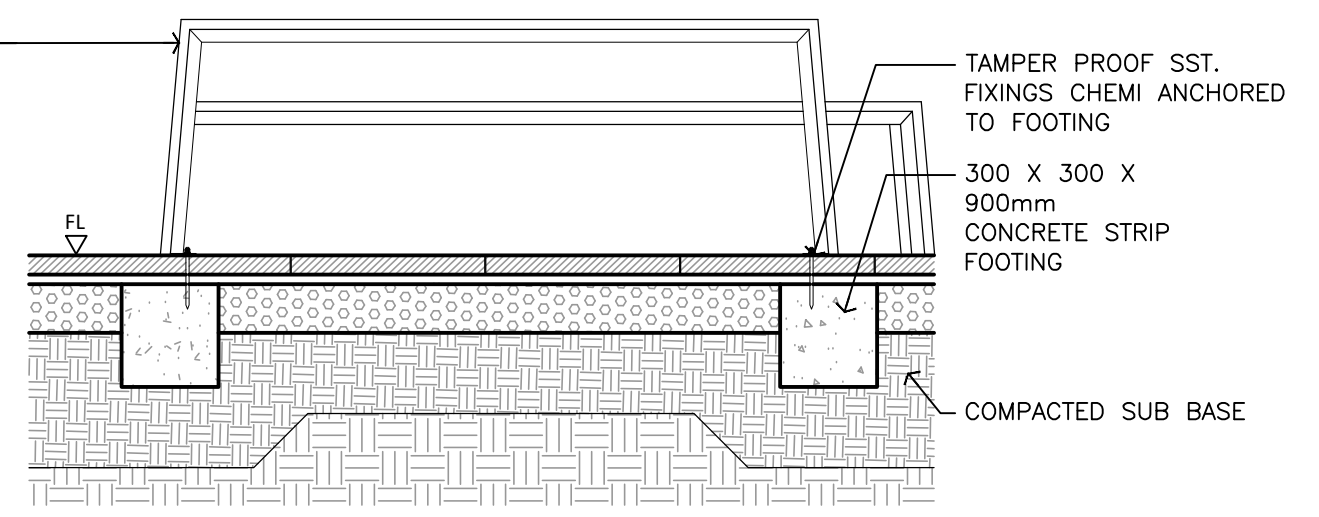


F_03 TIMBER TABLE AND BENCHES
SECTION
1:20

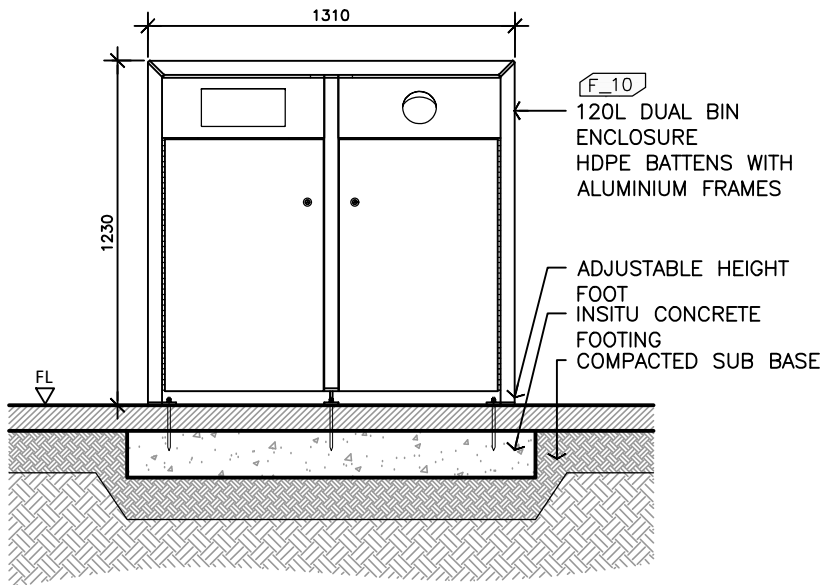


DOUBLE BIN ENCLOSURE - 120L
ELEVATION - FRONT (TYPICAL)

1:20

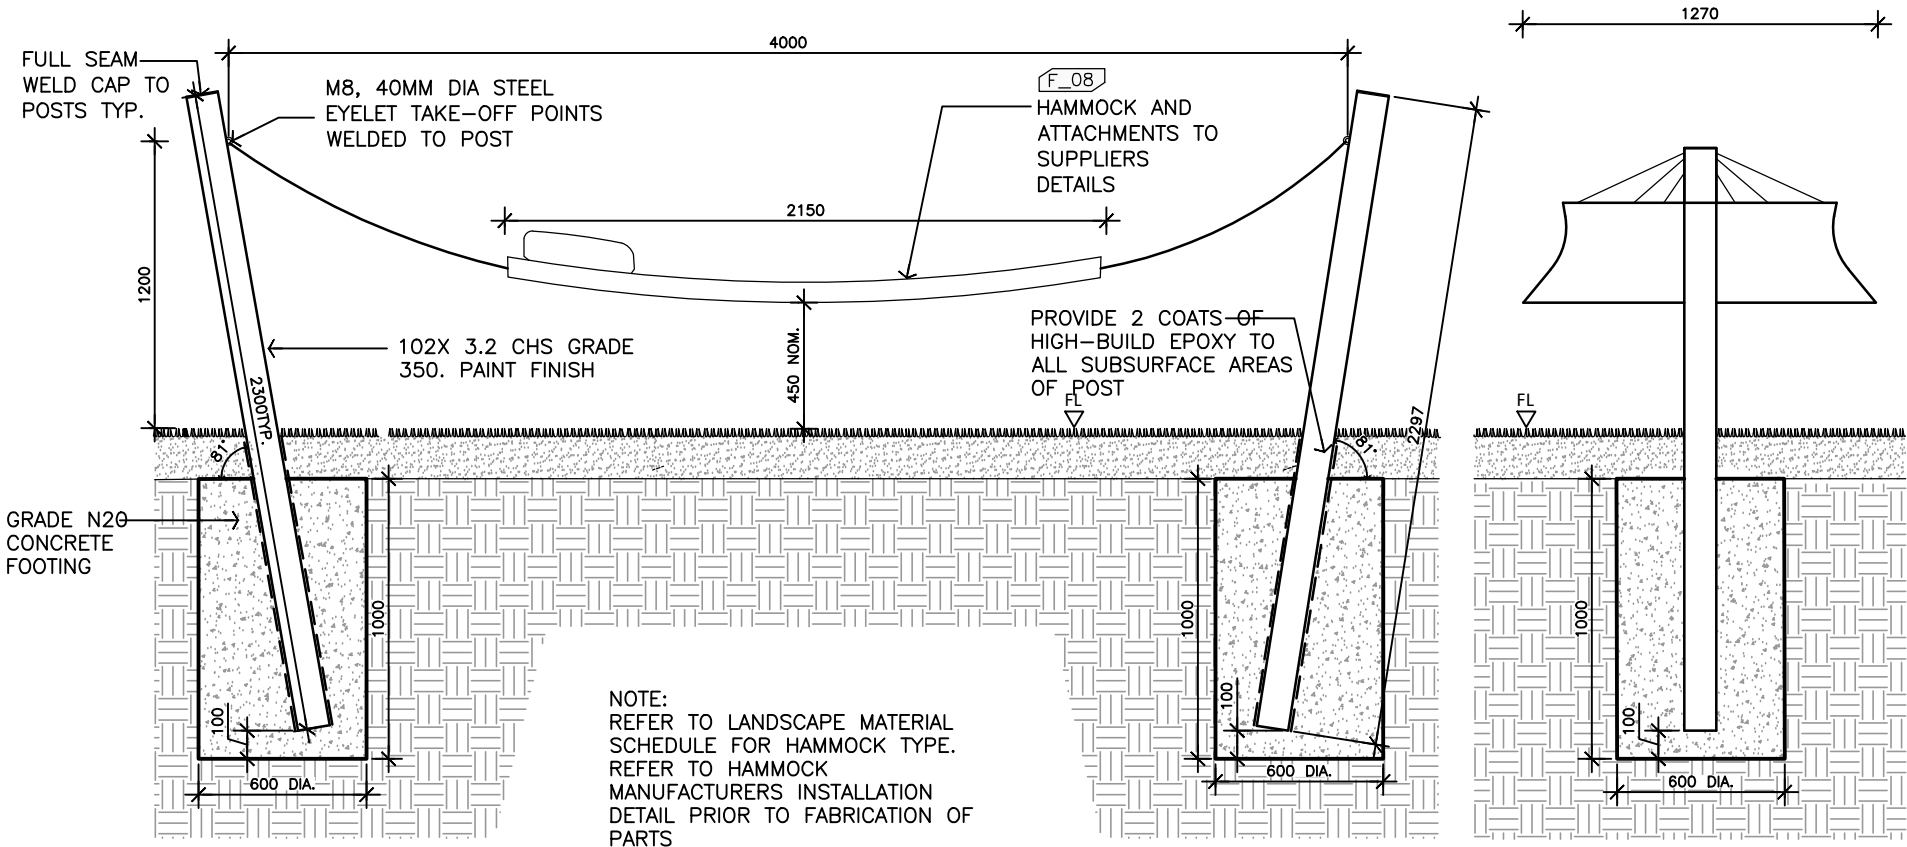

HAMMOCK
SECTION

1:20

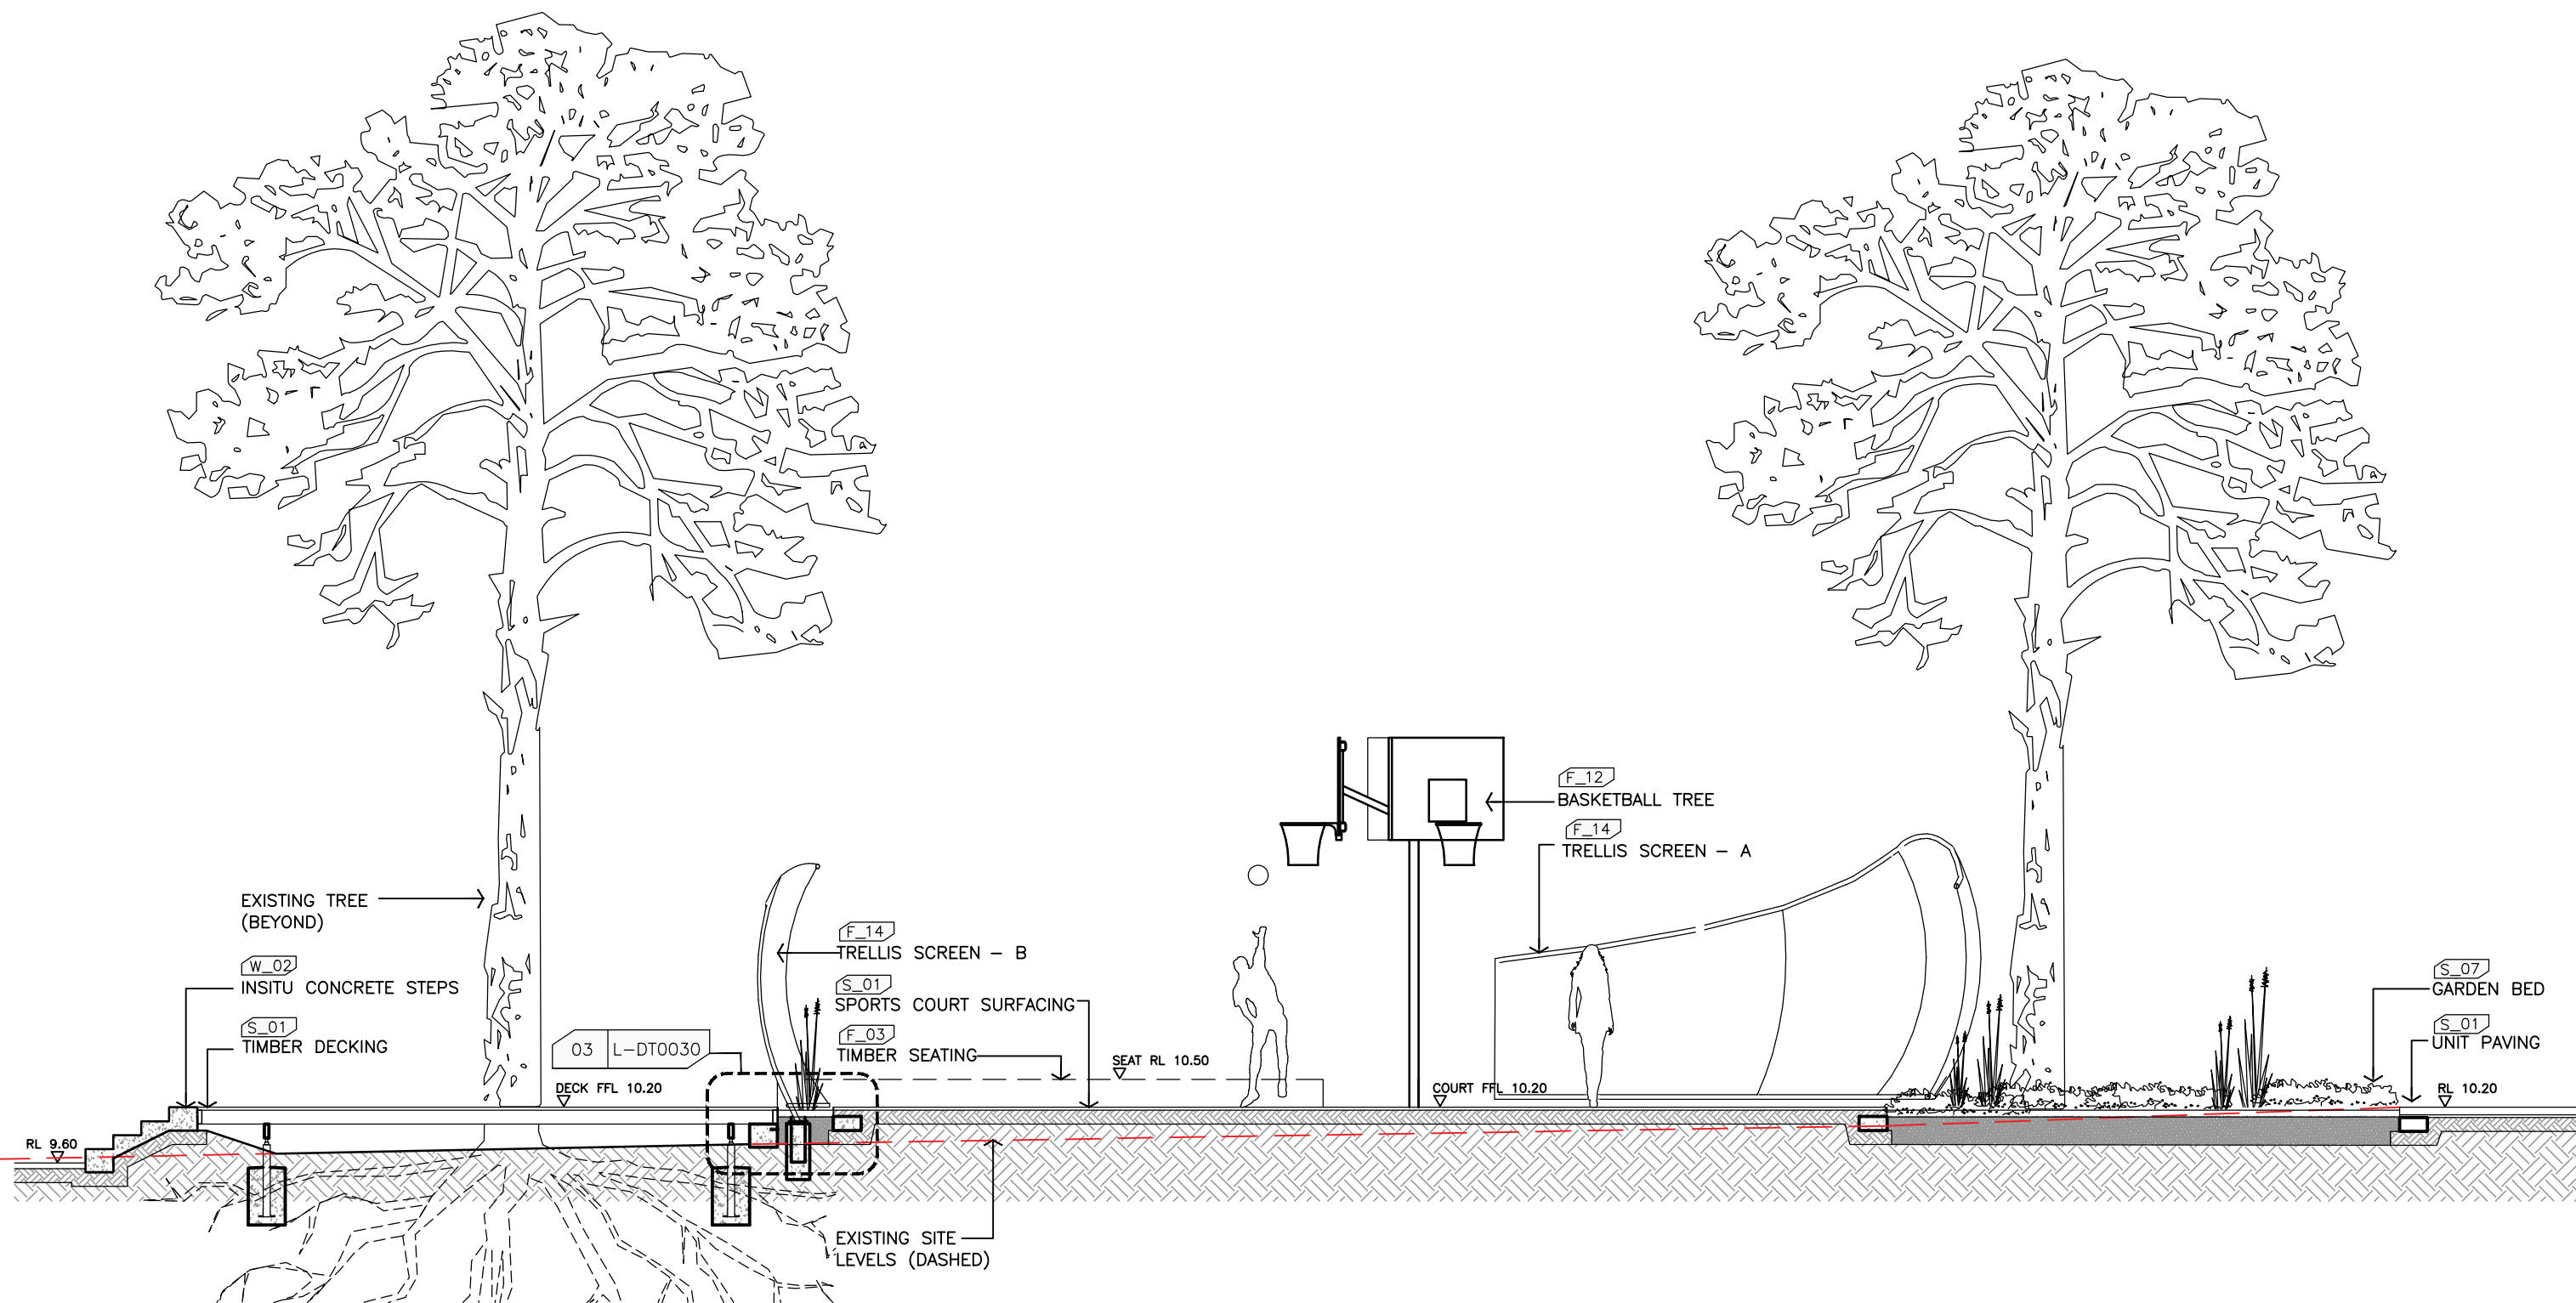






01


L-GA0001

GAMES COURT & DECK SECTION

SECTION

1:50

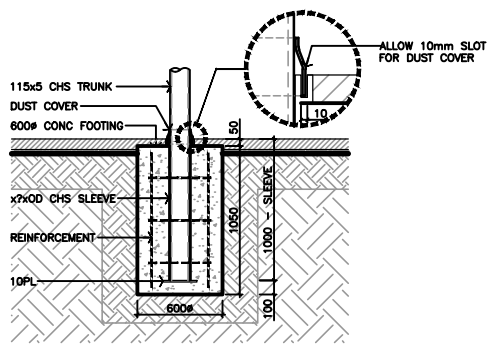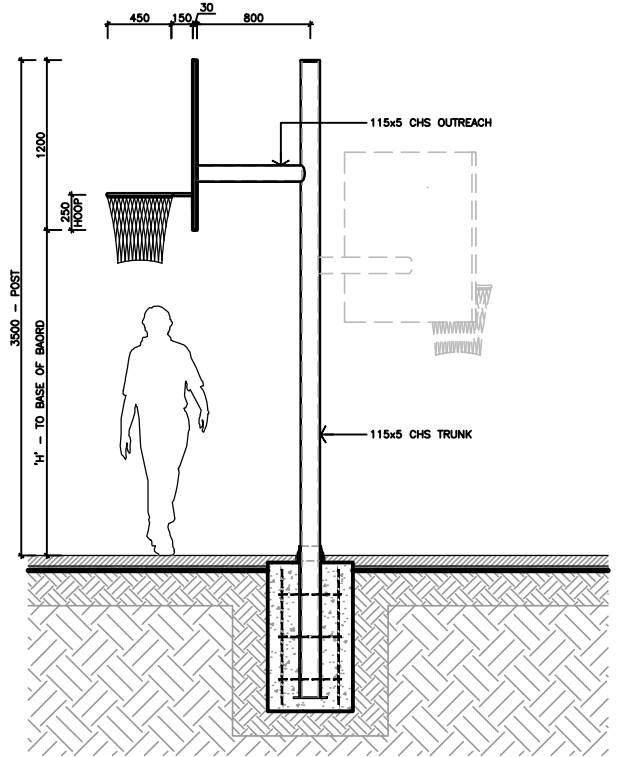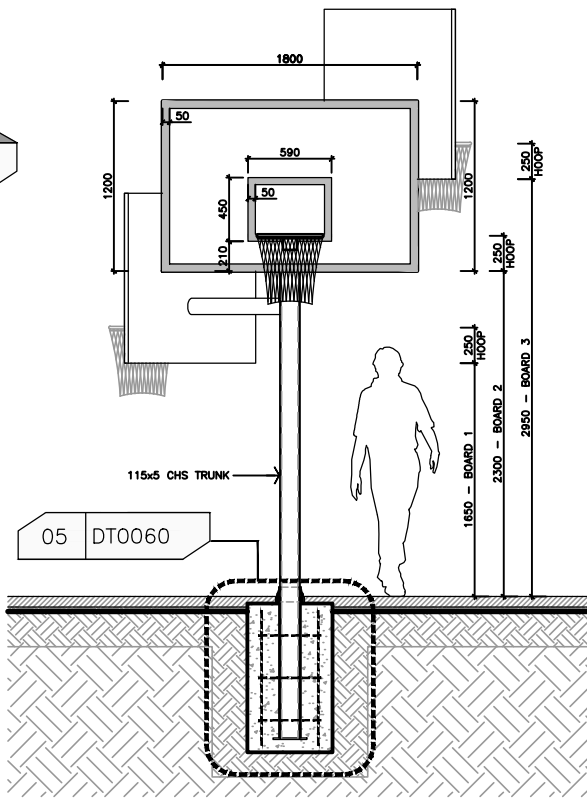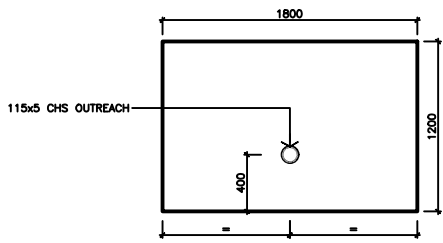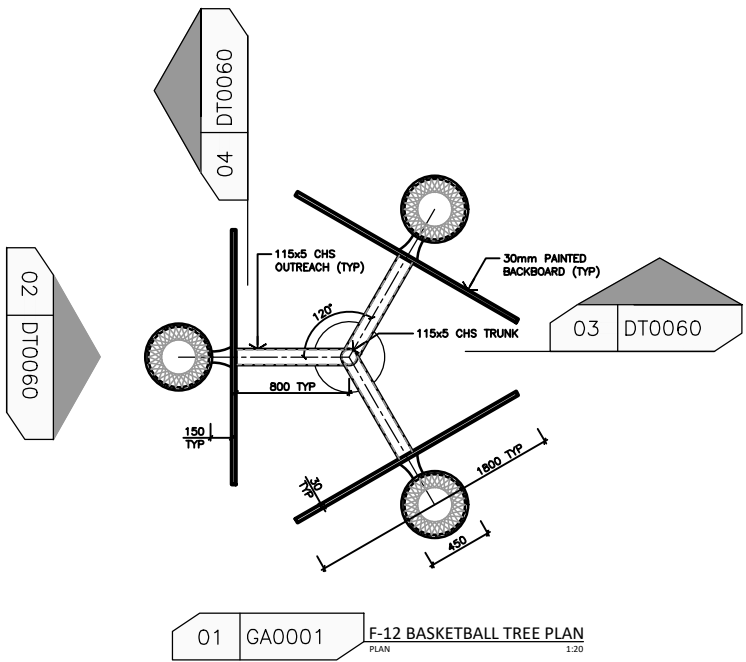


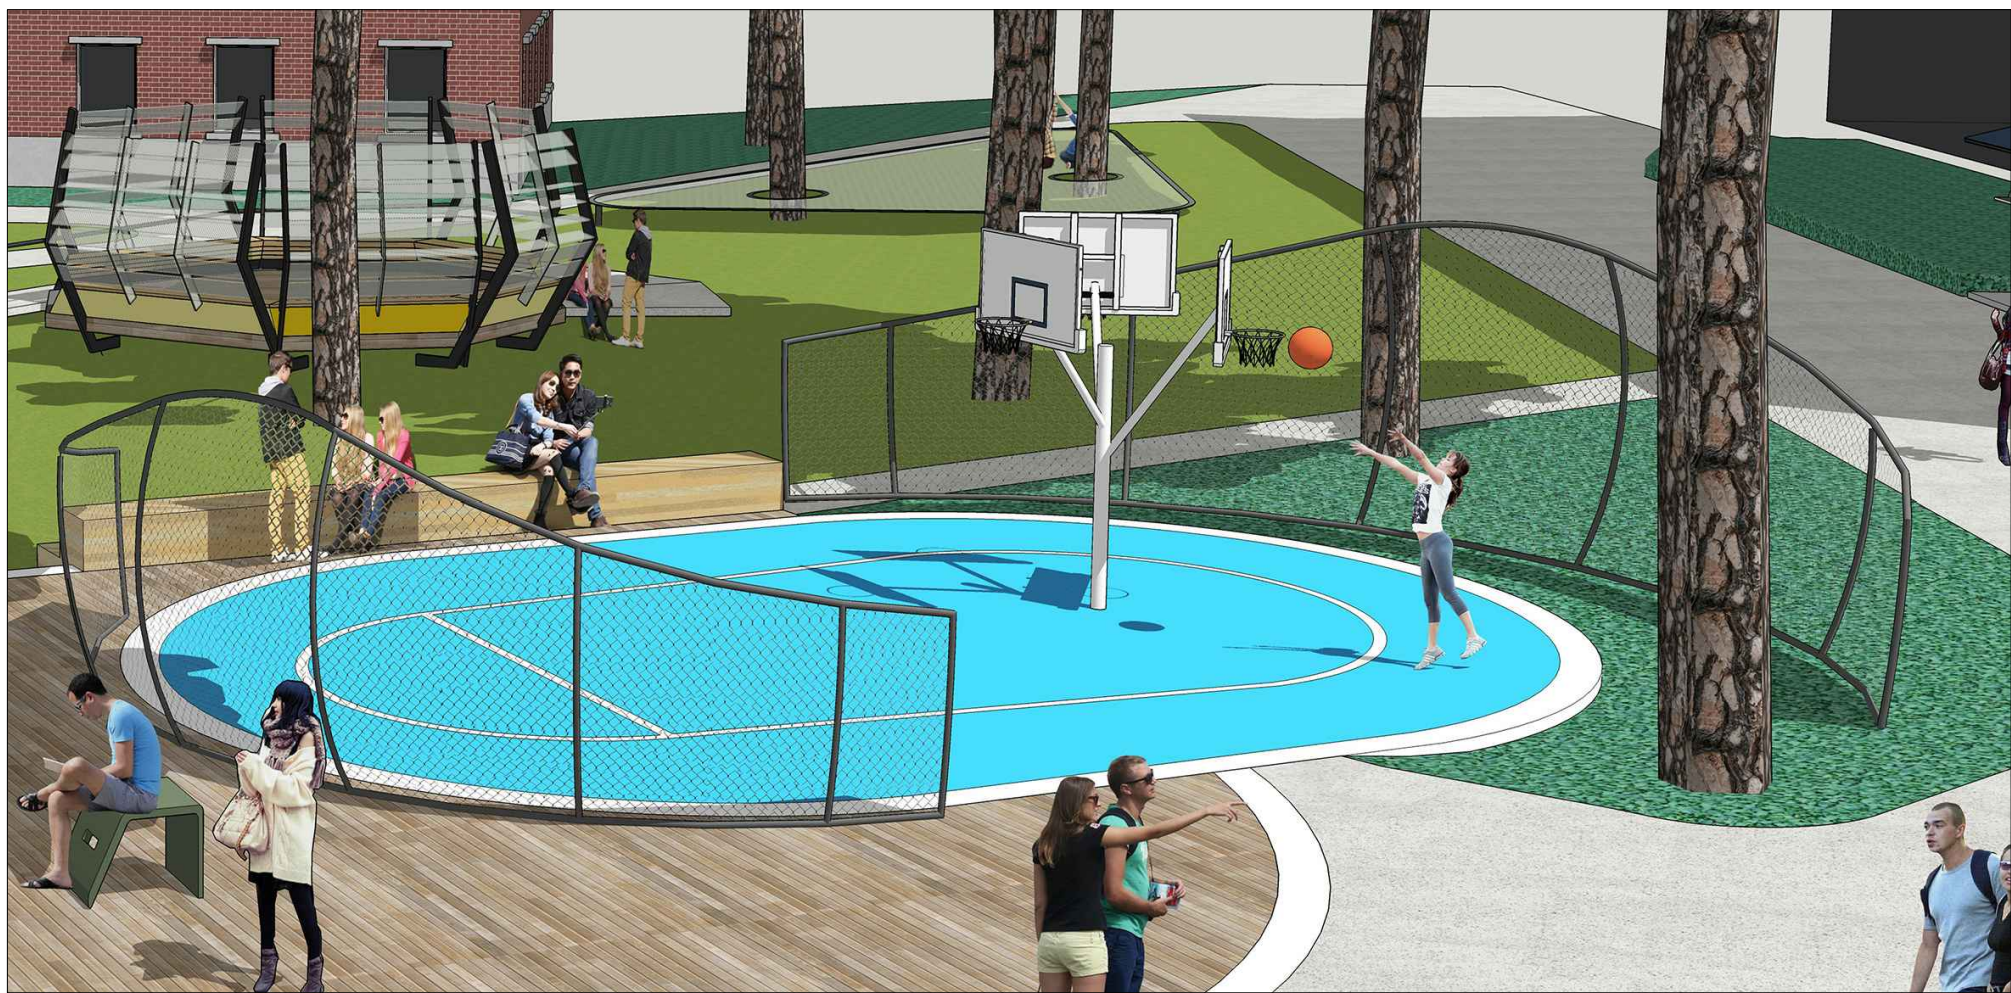

04

PERSPECTIVE


NTS

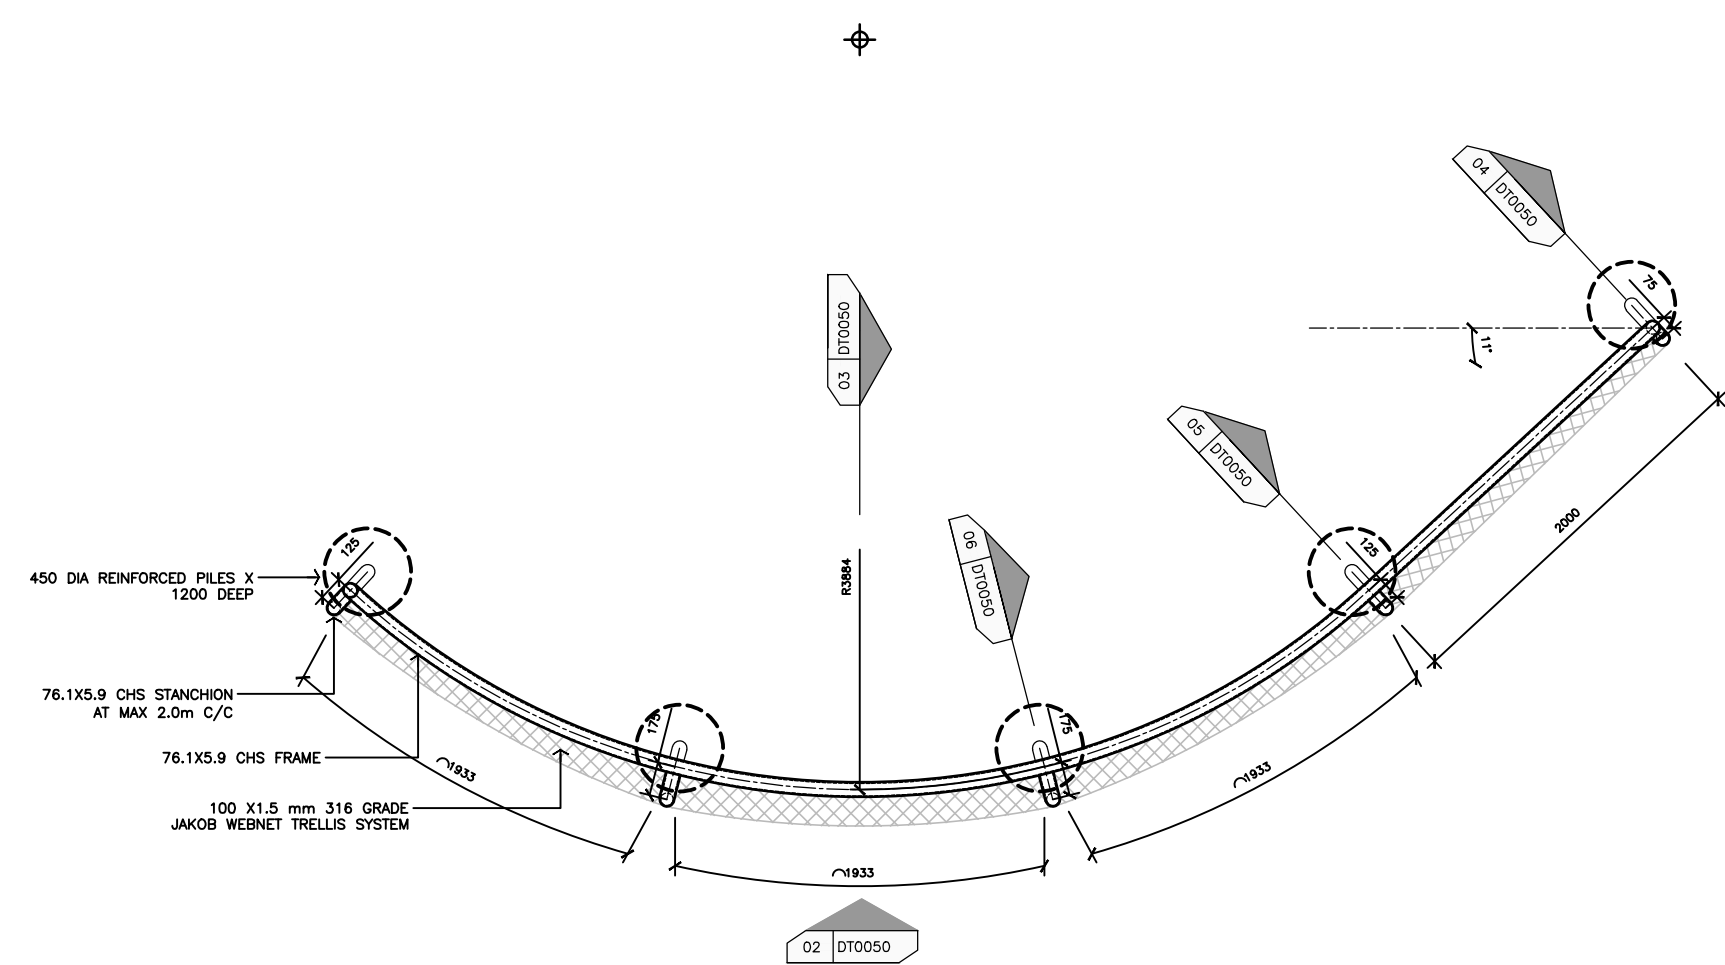

01 GA0001 F-14 TRELLIS SCREEN - A

PLAN


1:20

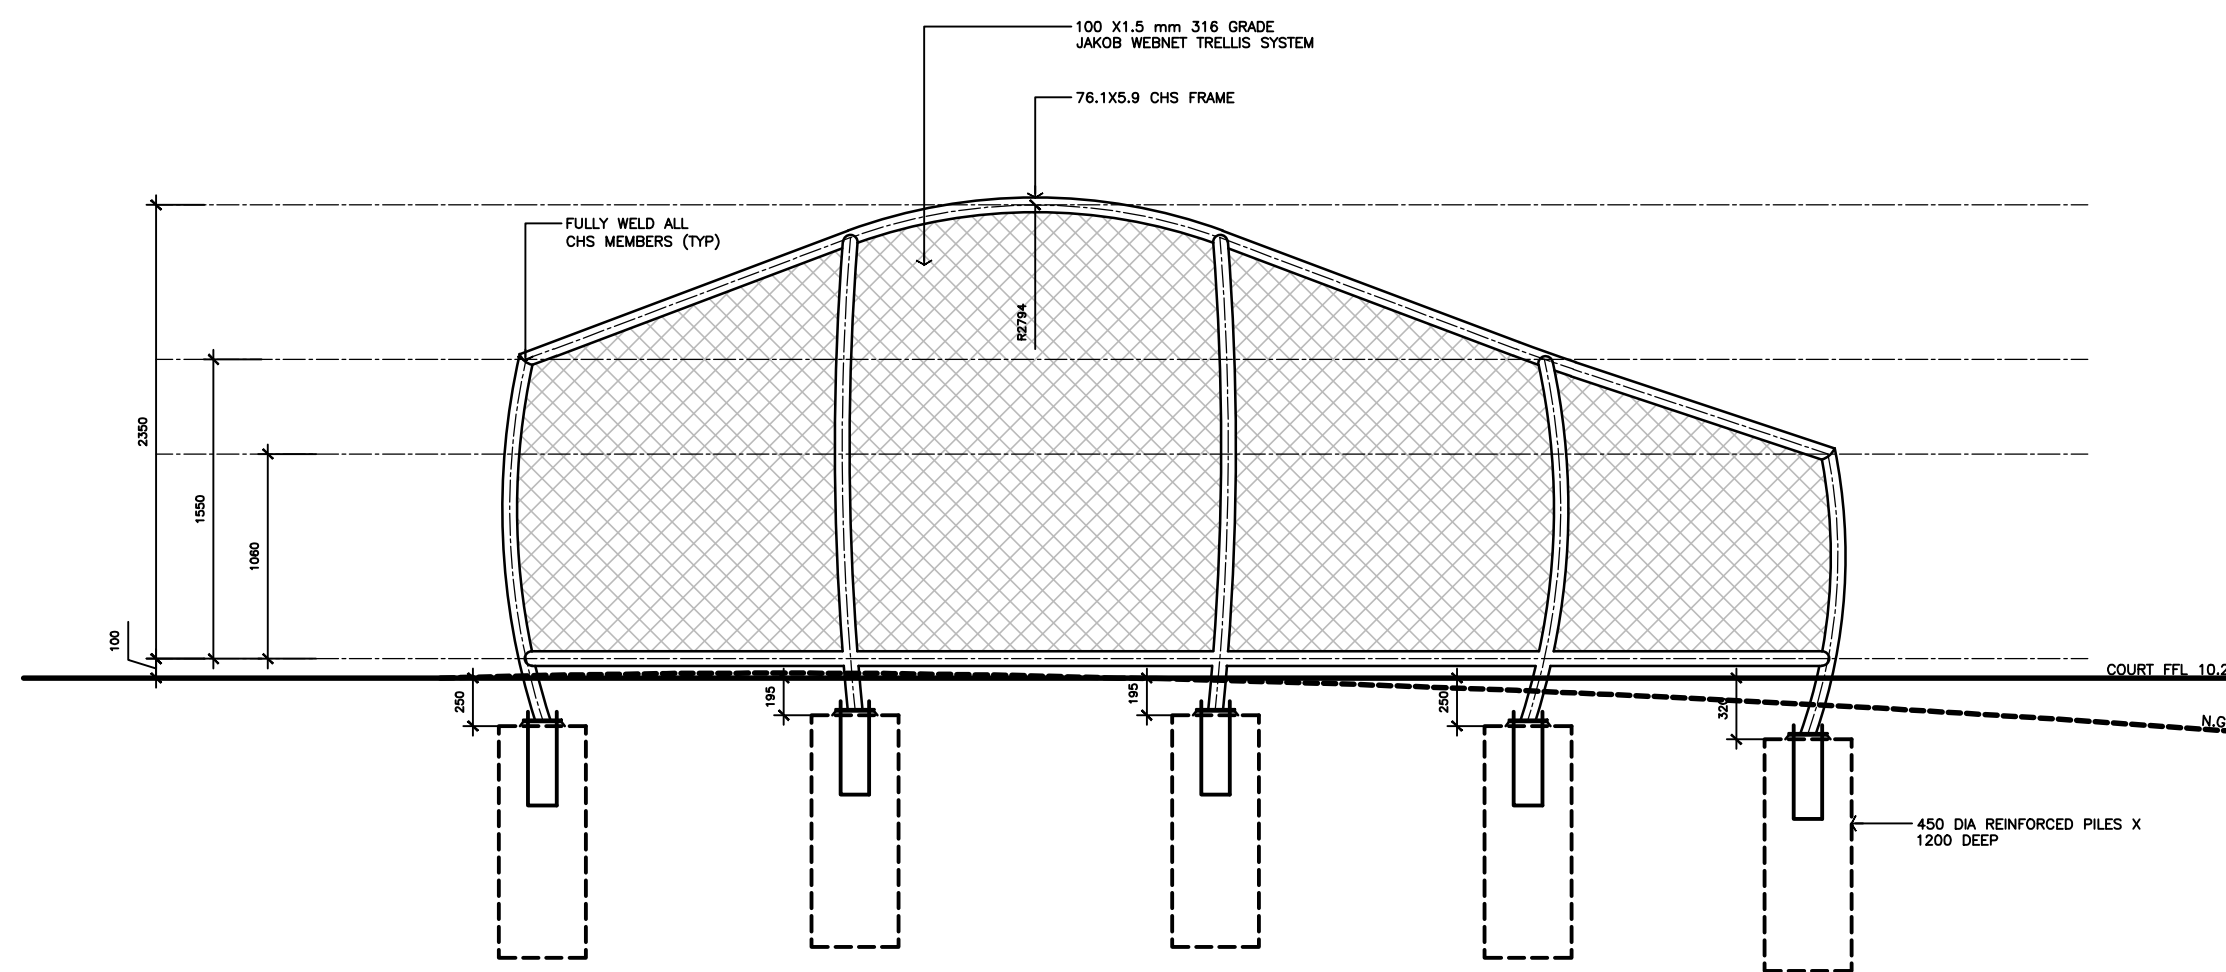

02 DT0050 ELEVATION - TRELLIS SCREEN A

ELEVATION


1:20

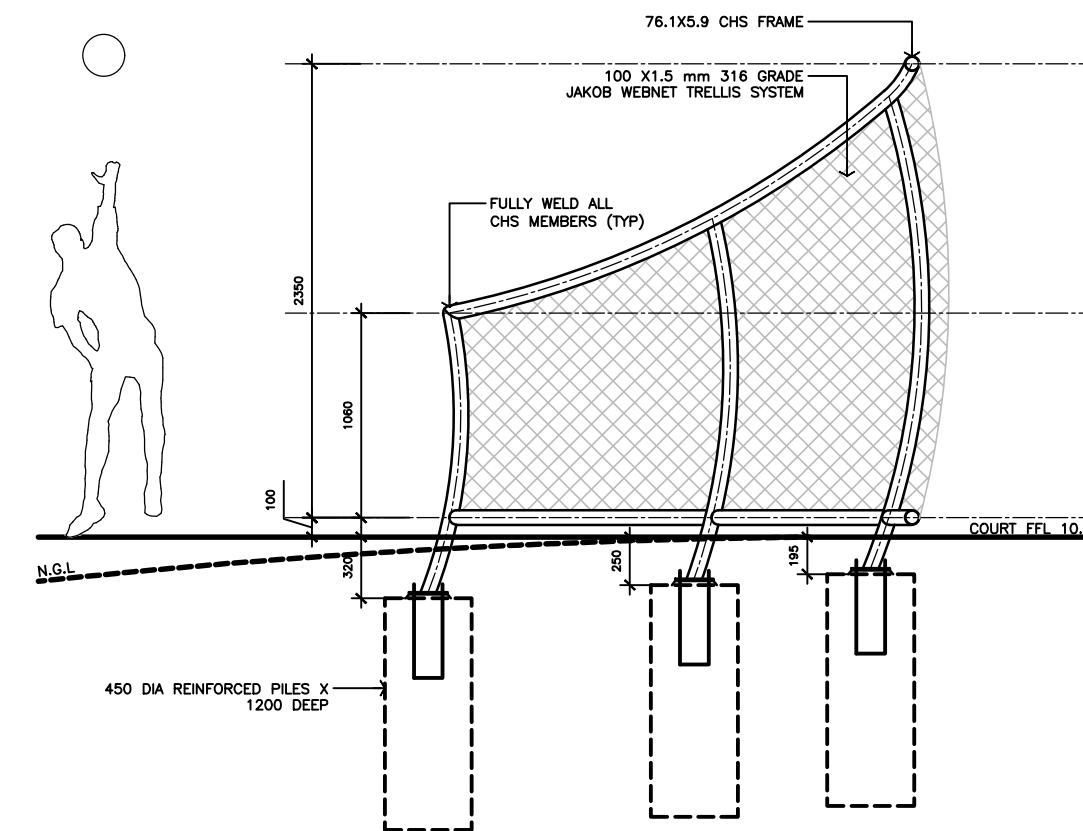

03 DT0050 SECTION - TRELLIS SCREEN A

SECTION


1:20

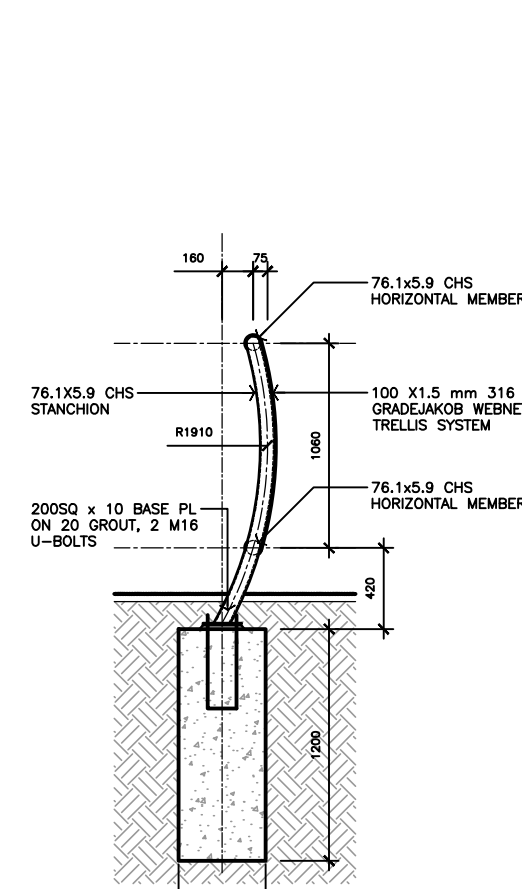

04 DT0050 STANCHION DETAIL

DETAIL


1:10

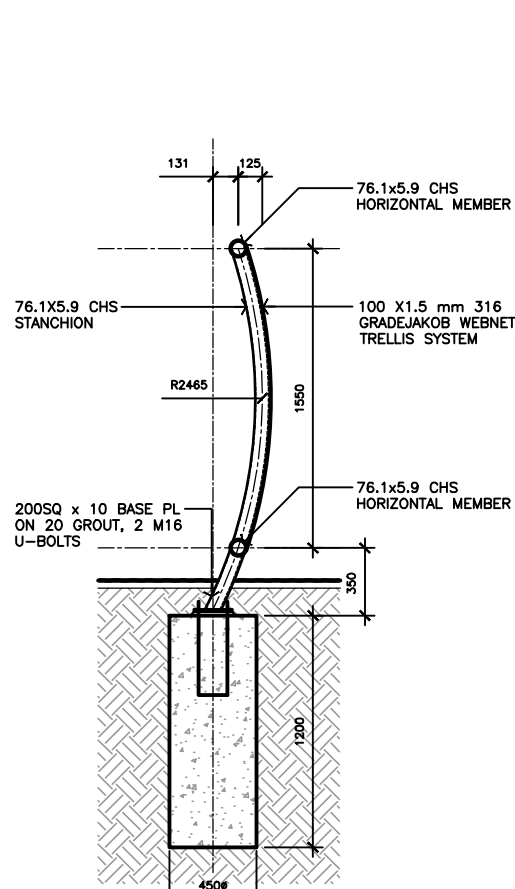

05 DT0050 STANCHION DETAIL

DETAIL


1:10

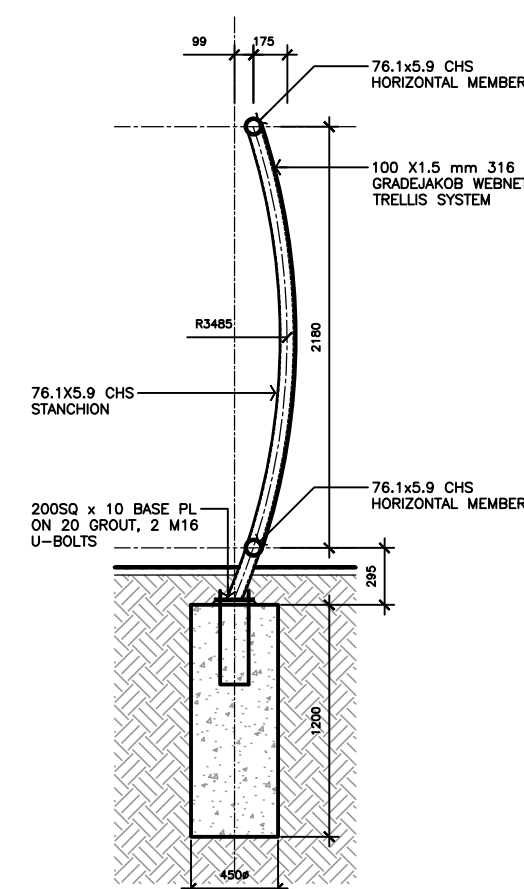


06 DT0050 STANCHION DETAIL

DETAIL


1:10

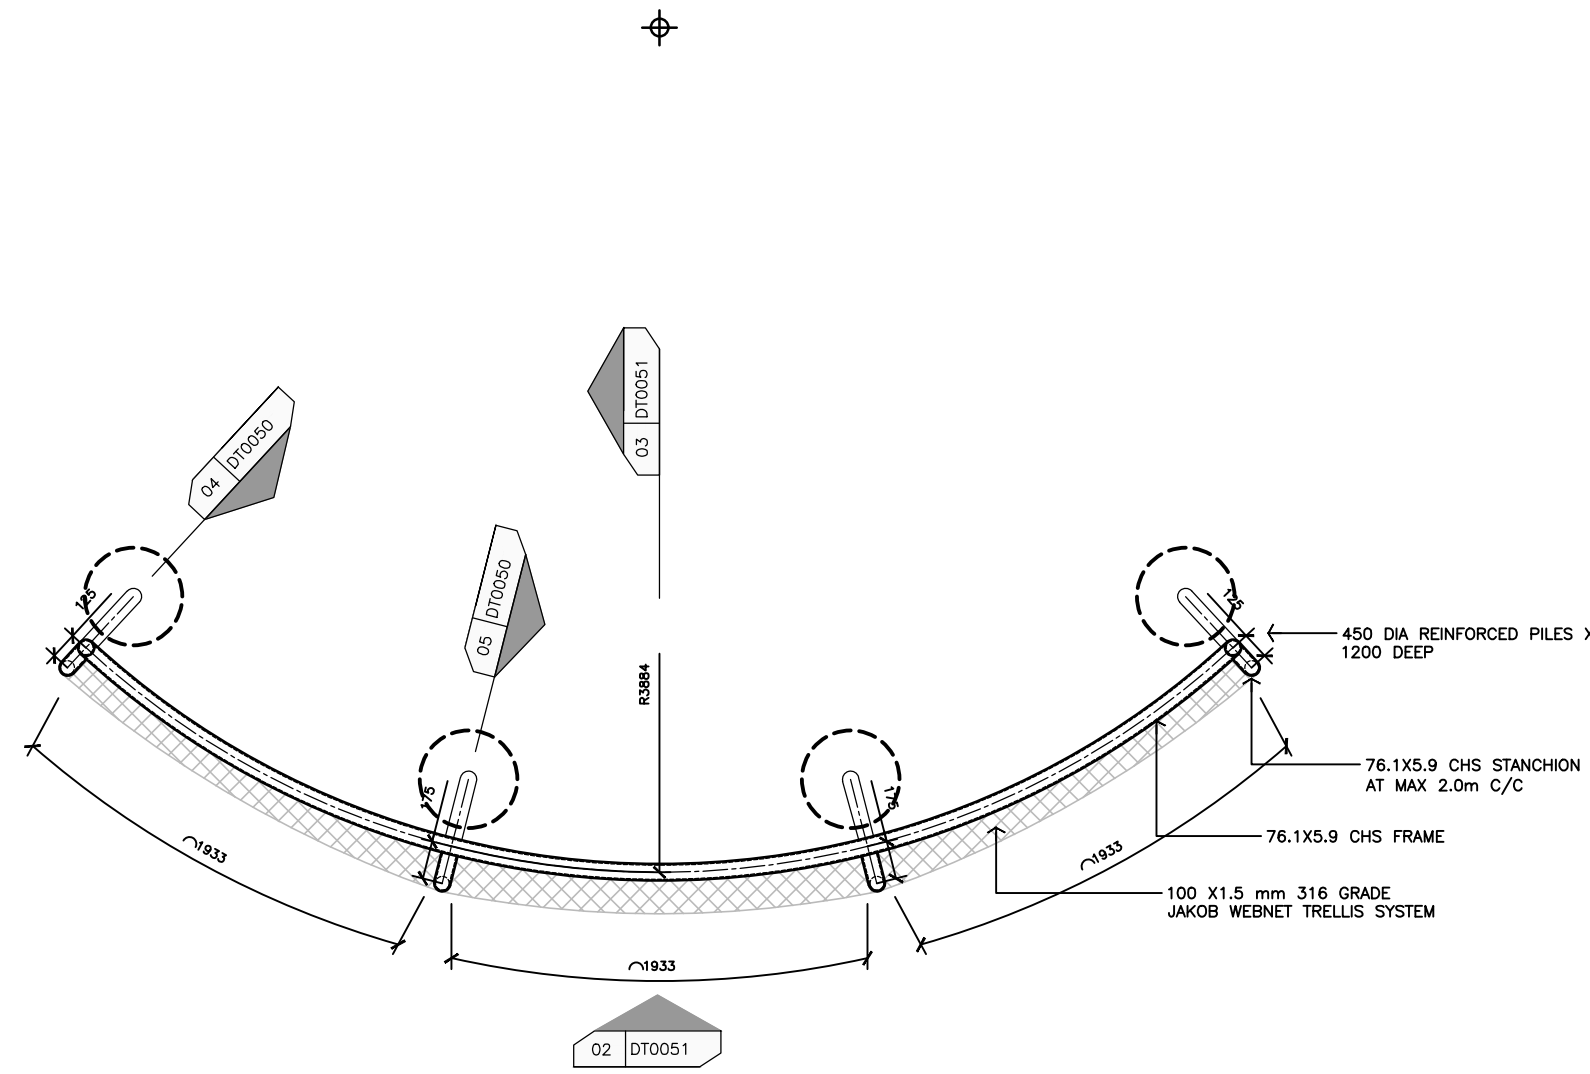


01 GA0001 F-14 TRELLIS SCREEN - B
PLAN 1:20

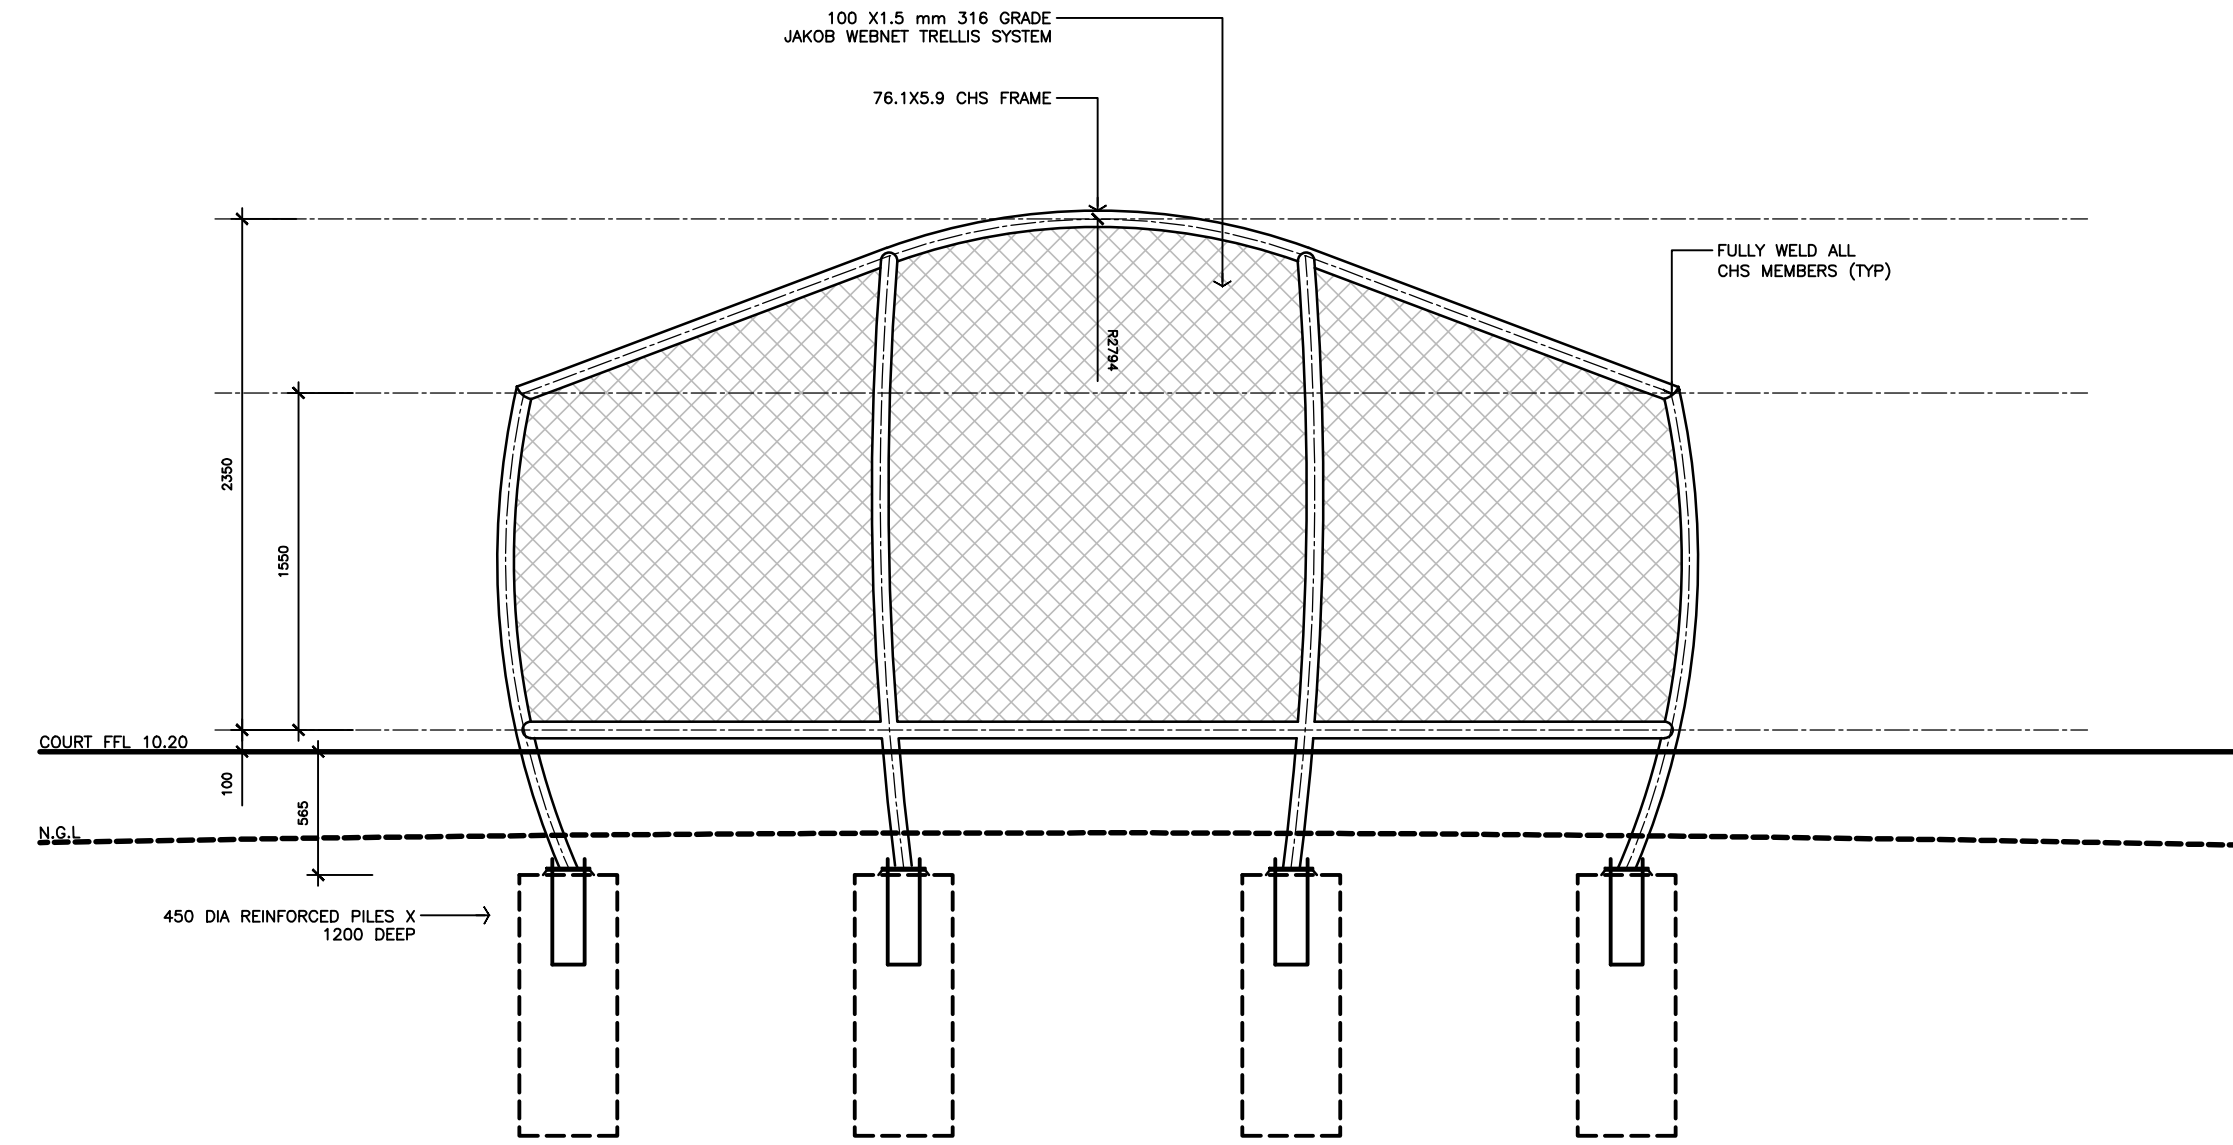


02 DT0051 ELEVATION - TRELLIS SCREEN B
ELEVATION 1:20

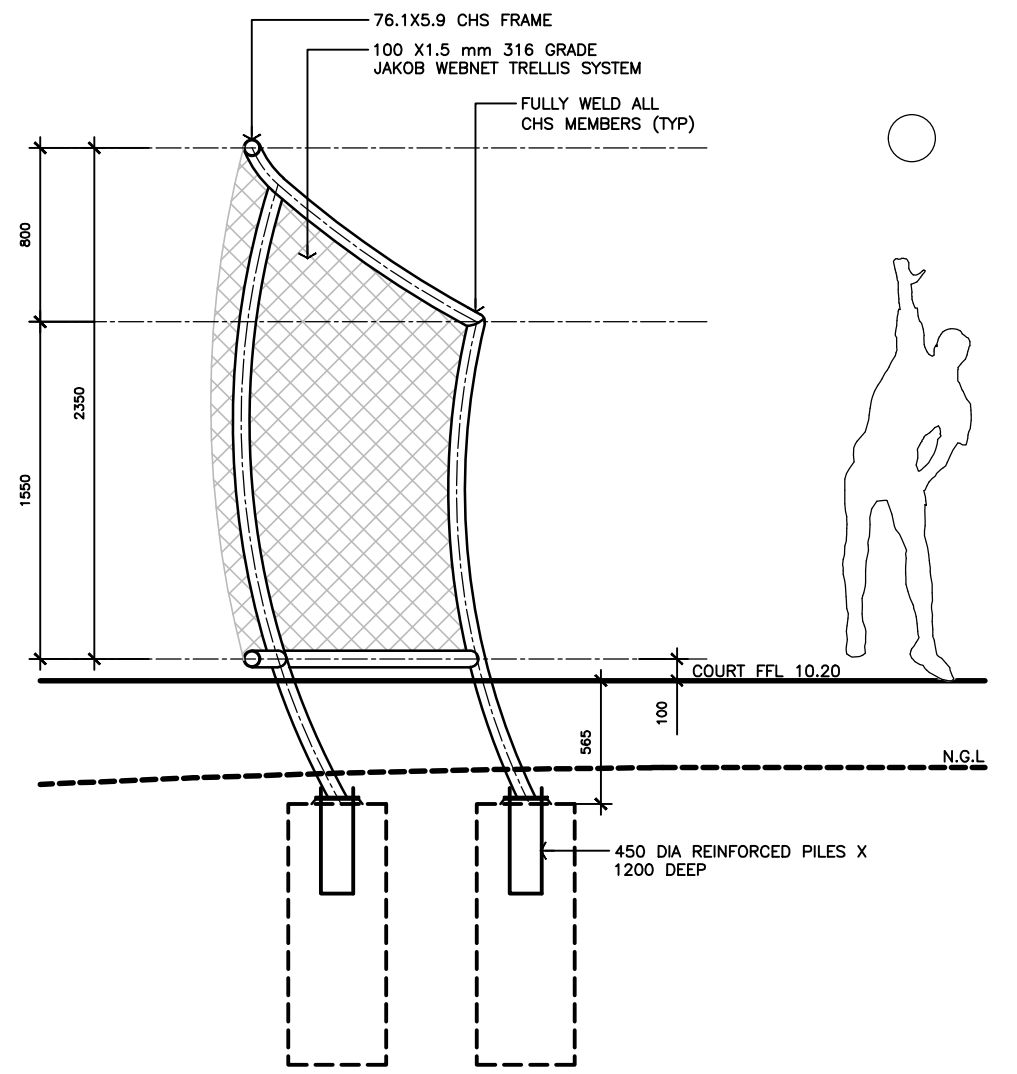

03 DT0051 SECTION - TRELLIS SCREEN B
SECTION 1:20

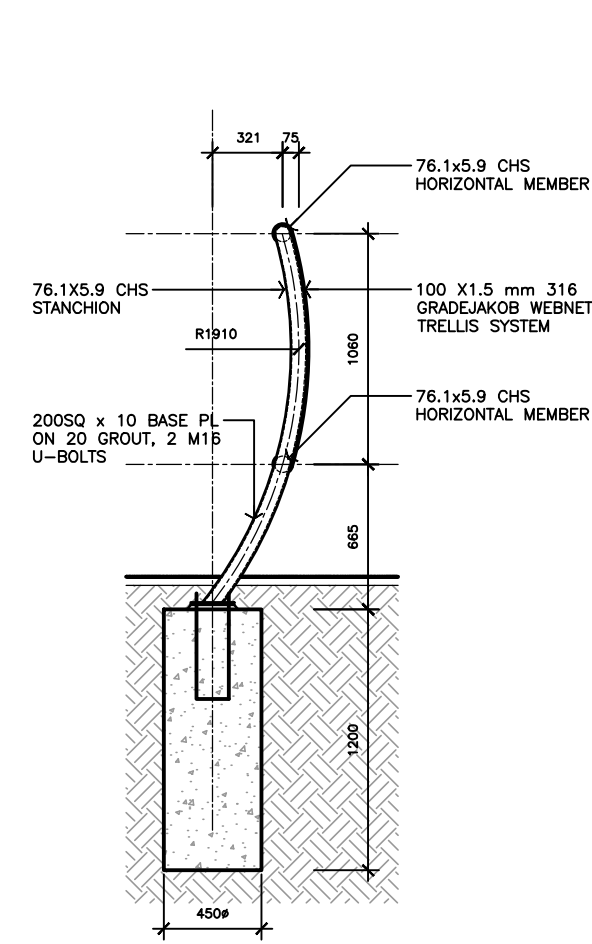

04 DT0051 STANCHION DETAIL
DETAIL 1:10

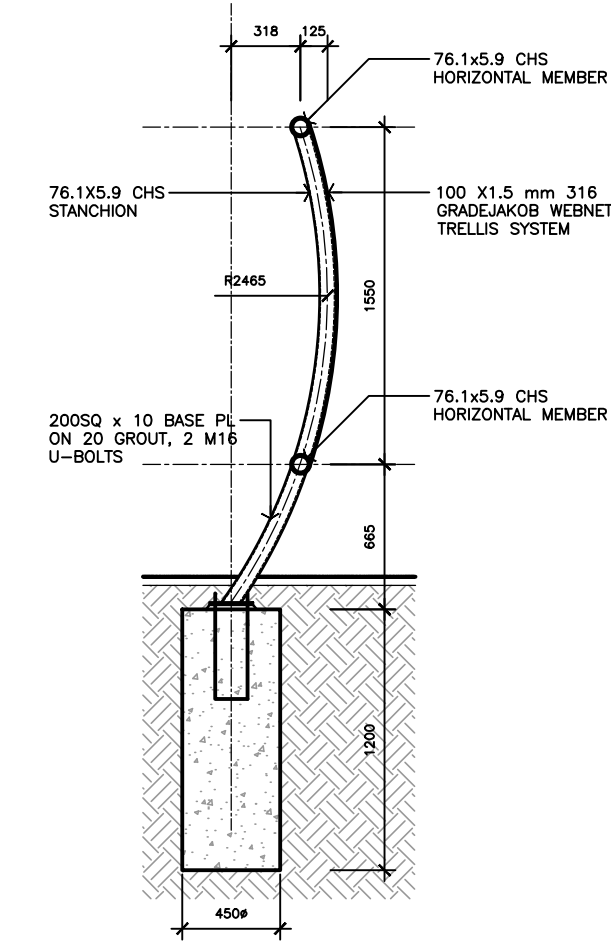

05 DT0051 STANCHION DETAIL
DETAIL 1:10