


GARDEN CITY

ANDREA LANE - EARLY WORKS

DRAWING LIST	
DWG	TITLE
001-CS	COVER SHEET & DRAWING INDEX
002-CS	LEGEND & PLANTING SCHEDULE
201-FI	FINISHES PLAN
202-FI	FINISHES PLAN
501-PL	PLANTING PLAN
502-PL	PLANTING PLAN

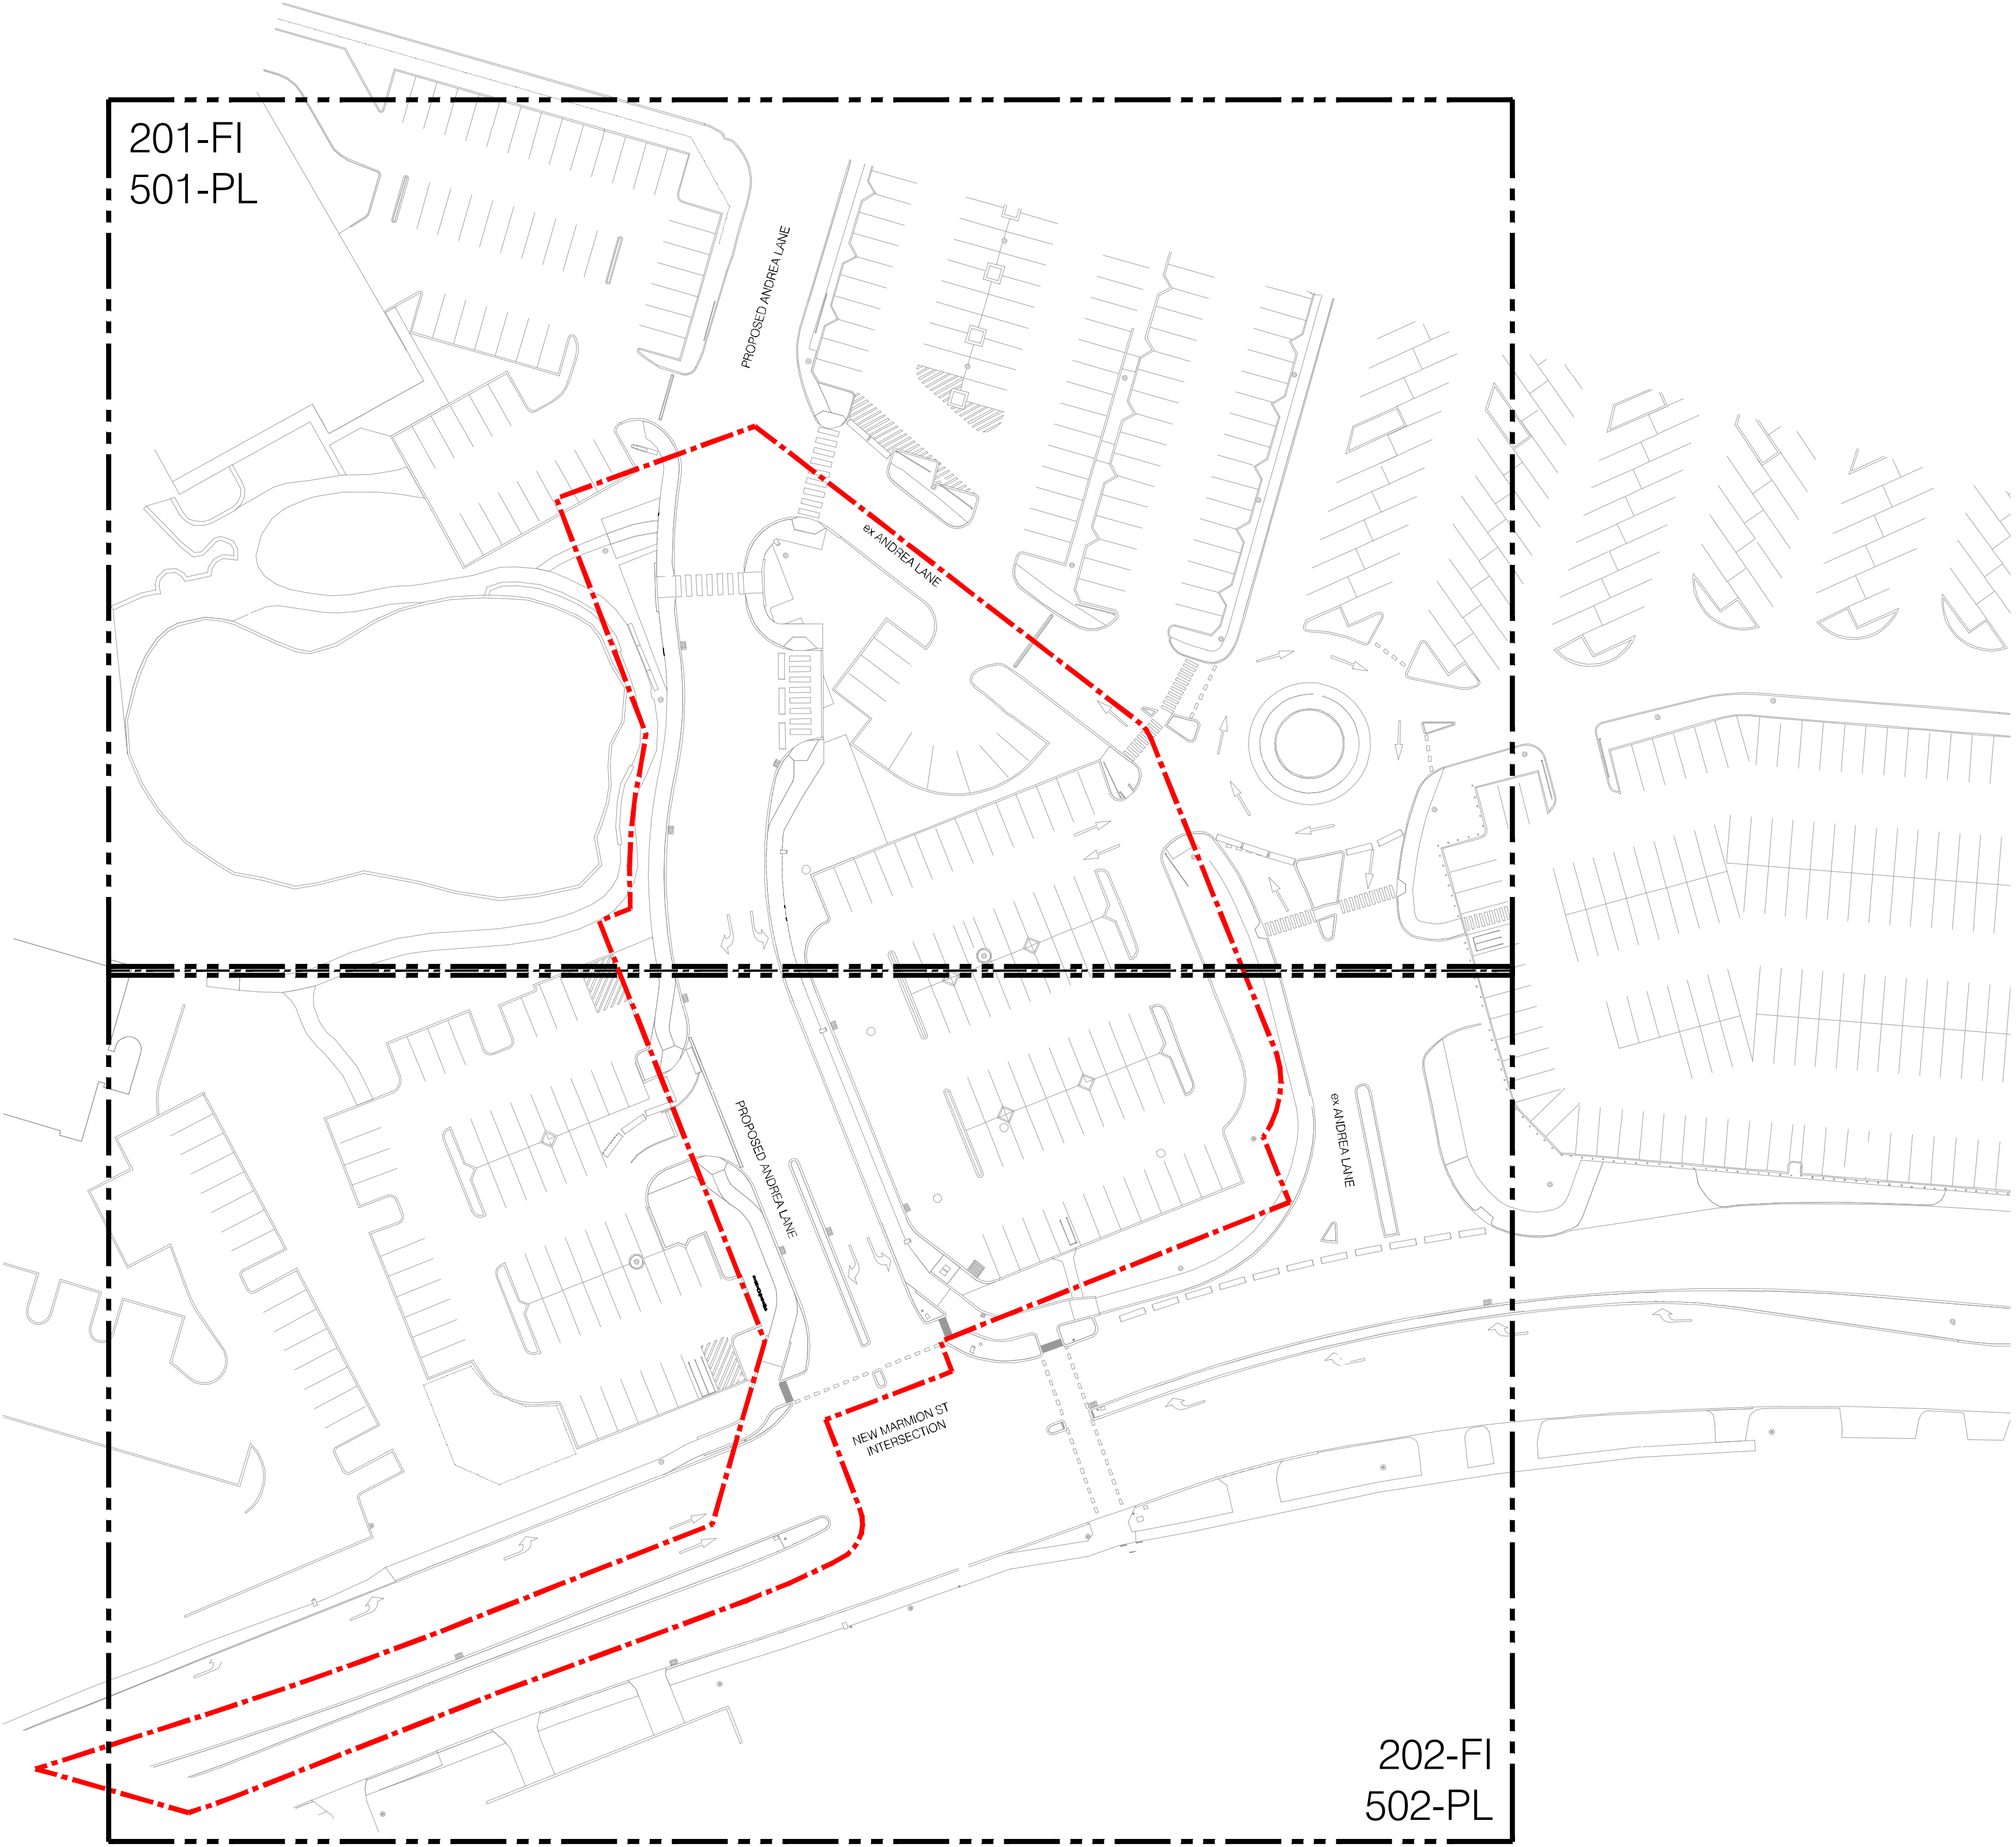

LOCATION PLAN

LEVEL 1, 55 ST GEORGES TCE
PERTH WA 6000 AUSTRALIA
TEL +618 9346 0500
FAX +618 9221 1779
www.urbis.com.au

URBIS Urbis Pty Ltd ABN 50 105 256 228

Copyright by Urbis Pty Ltd. This drawing, or parts thereof, may not be reproduced for any purpose without the consent of Urbis Pty Ltd. It is implied and has legal backing.

any discrepancies shall be referred to the Superintendent for a written decision prior to ordering/ supply/ installation/ construction.

KEY PLAN

LEGEND

EXTENT OF WORKS

— — — SHEET

NOT FOR CONSTRUCTION

A		ISSUED FOR INFORMATION ONLY	DC	PH	24.04.15
REV	NO	DESCRIPTION	DWN	CHK	DATE

PROJECT DIRECTOR: M.FREDRIKSSON

CLIENT

SCENTREGROUP

PROJECT

GARDEN CITY


ANDREA LANE - EARLY WORKS

DRAWING TITLE



LOCATION PLAN

ISSUE		PROJECT NO.	
INFORMATION		ND1152	
SCALE			
1:500 @ A1		1:1000 @ A3	
		50[m]	
DRAWING NO.		REVISION	
001-CS		A	

EXTENT OF WORKS

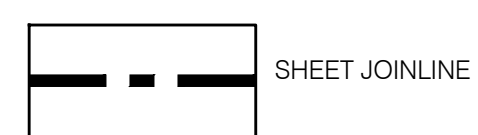

REFER TO SCHEDULE OF LANDSCAPE WORKS FOR DETAILS & FINISHES

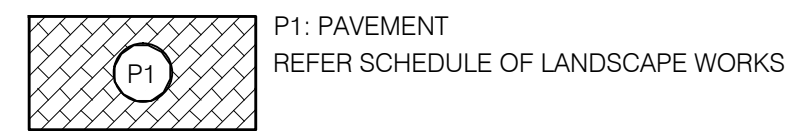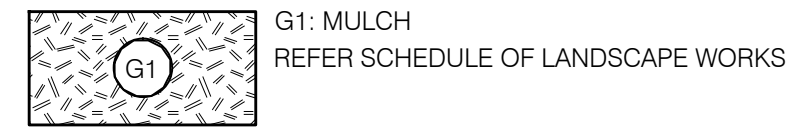

PROPOSED TREE
REFER PLANTING PLANS AND PLANT SCHEDULE

EXISTING TREE (SURVEYED)
TO BE RETAINED AND PROTECTED

EXISTING TREE (SURVEYED)
TO BE REMOVED

EXISTING TREE (NOT SURVEYED)

PLANT CODE	BOTANICAL NAME	COMMON NAME	CONTAINER SIZE	QTY
Eug	Eucalyptus gomphocephala	Tuart	200Ltr	9
Euv	Eucalyptus vitrix	Snow Queen	200Ltr	12
Eue	Eucalyptus erythrococus	Red Cap Gum	100Ltr	3
Mele	Melaleuca leucandendra	Weeping Paperbark	100Ltr	4
Xap	Xanthorrhoea preissii	Grass Tree	100Ltr	6
SUBTOTAL:				34
Erg	Eremophila glabra	Emu Bush	130mm	43
Errn	Eremophila nivea	Silky Eremophila	130mm	43
Cha	Chrysocephalum apiculatum	Yellow buttons	130mm	69
Leb	Leucophyta brownii	Cushion bush	130mm	53
Coc	Conostylus candicans	Yellow buttons	130mm	43
SUBTOTAL:				251
AcI	Acacia lasiocarpa prostrate	Glow Wattle	130mm	170
Bea	Beaufortia aestiva 'Summer Flame'	Summer Flame	130mm	170
Caq	Calothamnus quadrifidus	One-sided Bottlebrush	130mm	170
Leg	Lepidosperma gladiatum	Coast Sword-sedge	130mm	130
Loc	Lomandra confertifolia 'Seascape'	Mat Rush	130mm	224
Meh	Melaleuca huegelii 'Rambler'	Chenille Honey-myrtle	130mm	170
Pif	Pimelea ferruginea	Rice Flower	130mm	170
Wef	Westringia fruticosa 'Grey Box'	Grey Box	130mm	170
SUBTOTAL:				1320
Anf	Anigozanthos flavidus	Evergreen Kangaroo paw	130mm	60
Cha	Chrysocephalum apiculatum	Yellow buttons	130mm	103
Leb	Leucophyta brownii	Cushion bush	130mm	50
Leg	Lepidosperma gladiatum	Coast Sword-sedge	130mm	100
SUBTOTAL:				313

[illegible]

JOINS 202-PL

ex ANDREA LANE

PROPOSED ANDREA LANE

PROPOSED

— RAISE
WATER
MAIN

NEW MARMION ST
INTERSECTION

KEY PLAN

LEGEND

 EXTENT OF WORKS
 SHEET JOIN LINE

NOT FOR CONSTRUCTION

CLIENT
SCENTREGROUP

PROJECT DIRECTOR: M.FREDRIKSSON

PROJECT

GARDEN CITY

ANDREA LANE - EARLY WORKS

DRAWING TITLE
FINISHES PLAN

ISSUE
INFORMATION ONLY

SCALE 1:200 @ A1 1:400 @ A3



0 2 4 6 8 10

DRAWING NO.

201-FI

PROJECT NO.
ND1152

REVISION

A

LEVEL 1, 55 ST GEORGES TCE
PERTH WA 6000 AUSTRALIA
TEL +618 9346 0500
FAX +618 9221 1779
www.urbis.com.au


Urbis Pty Ltd ABN 50 105 256 228
Australia . Asia . Middle East

Copyright by Urbis Pty Ltd. This drawing, or parts thereof, may not be reproduced for any purpose without the consent of Urbis Pty Ltd. It is implied and has legal backing.

The drawings are to be read in conjunction with the specification and any other written instructions issued.
Any discrepancies shall be referred to the Superintendent for a written decision prior to ordering/ supply/ installation/ construction.

LAST SAVED: 4/24/2015 10:48 AM BY: DCLANCY

T:\003 PROJECTS\CURRENT\ND 1152 - GARDEN CITY LANDSCAPE DESIGN\ANDREA LANE - EARLY WORKS\DRAWINGS\LAYOUTS\201-FI.DWG

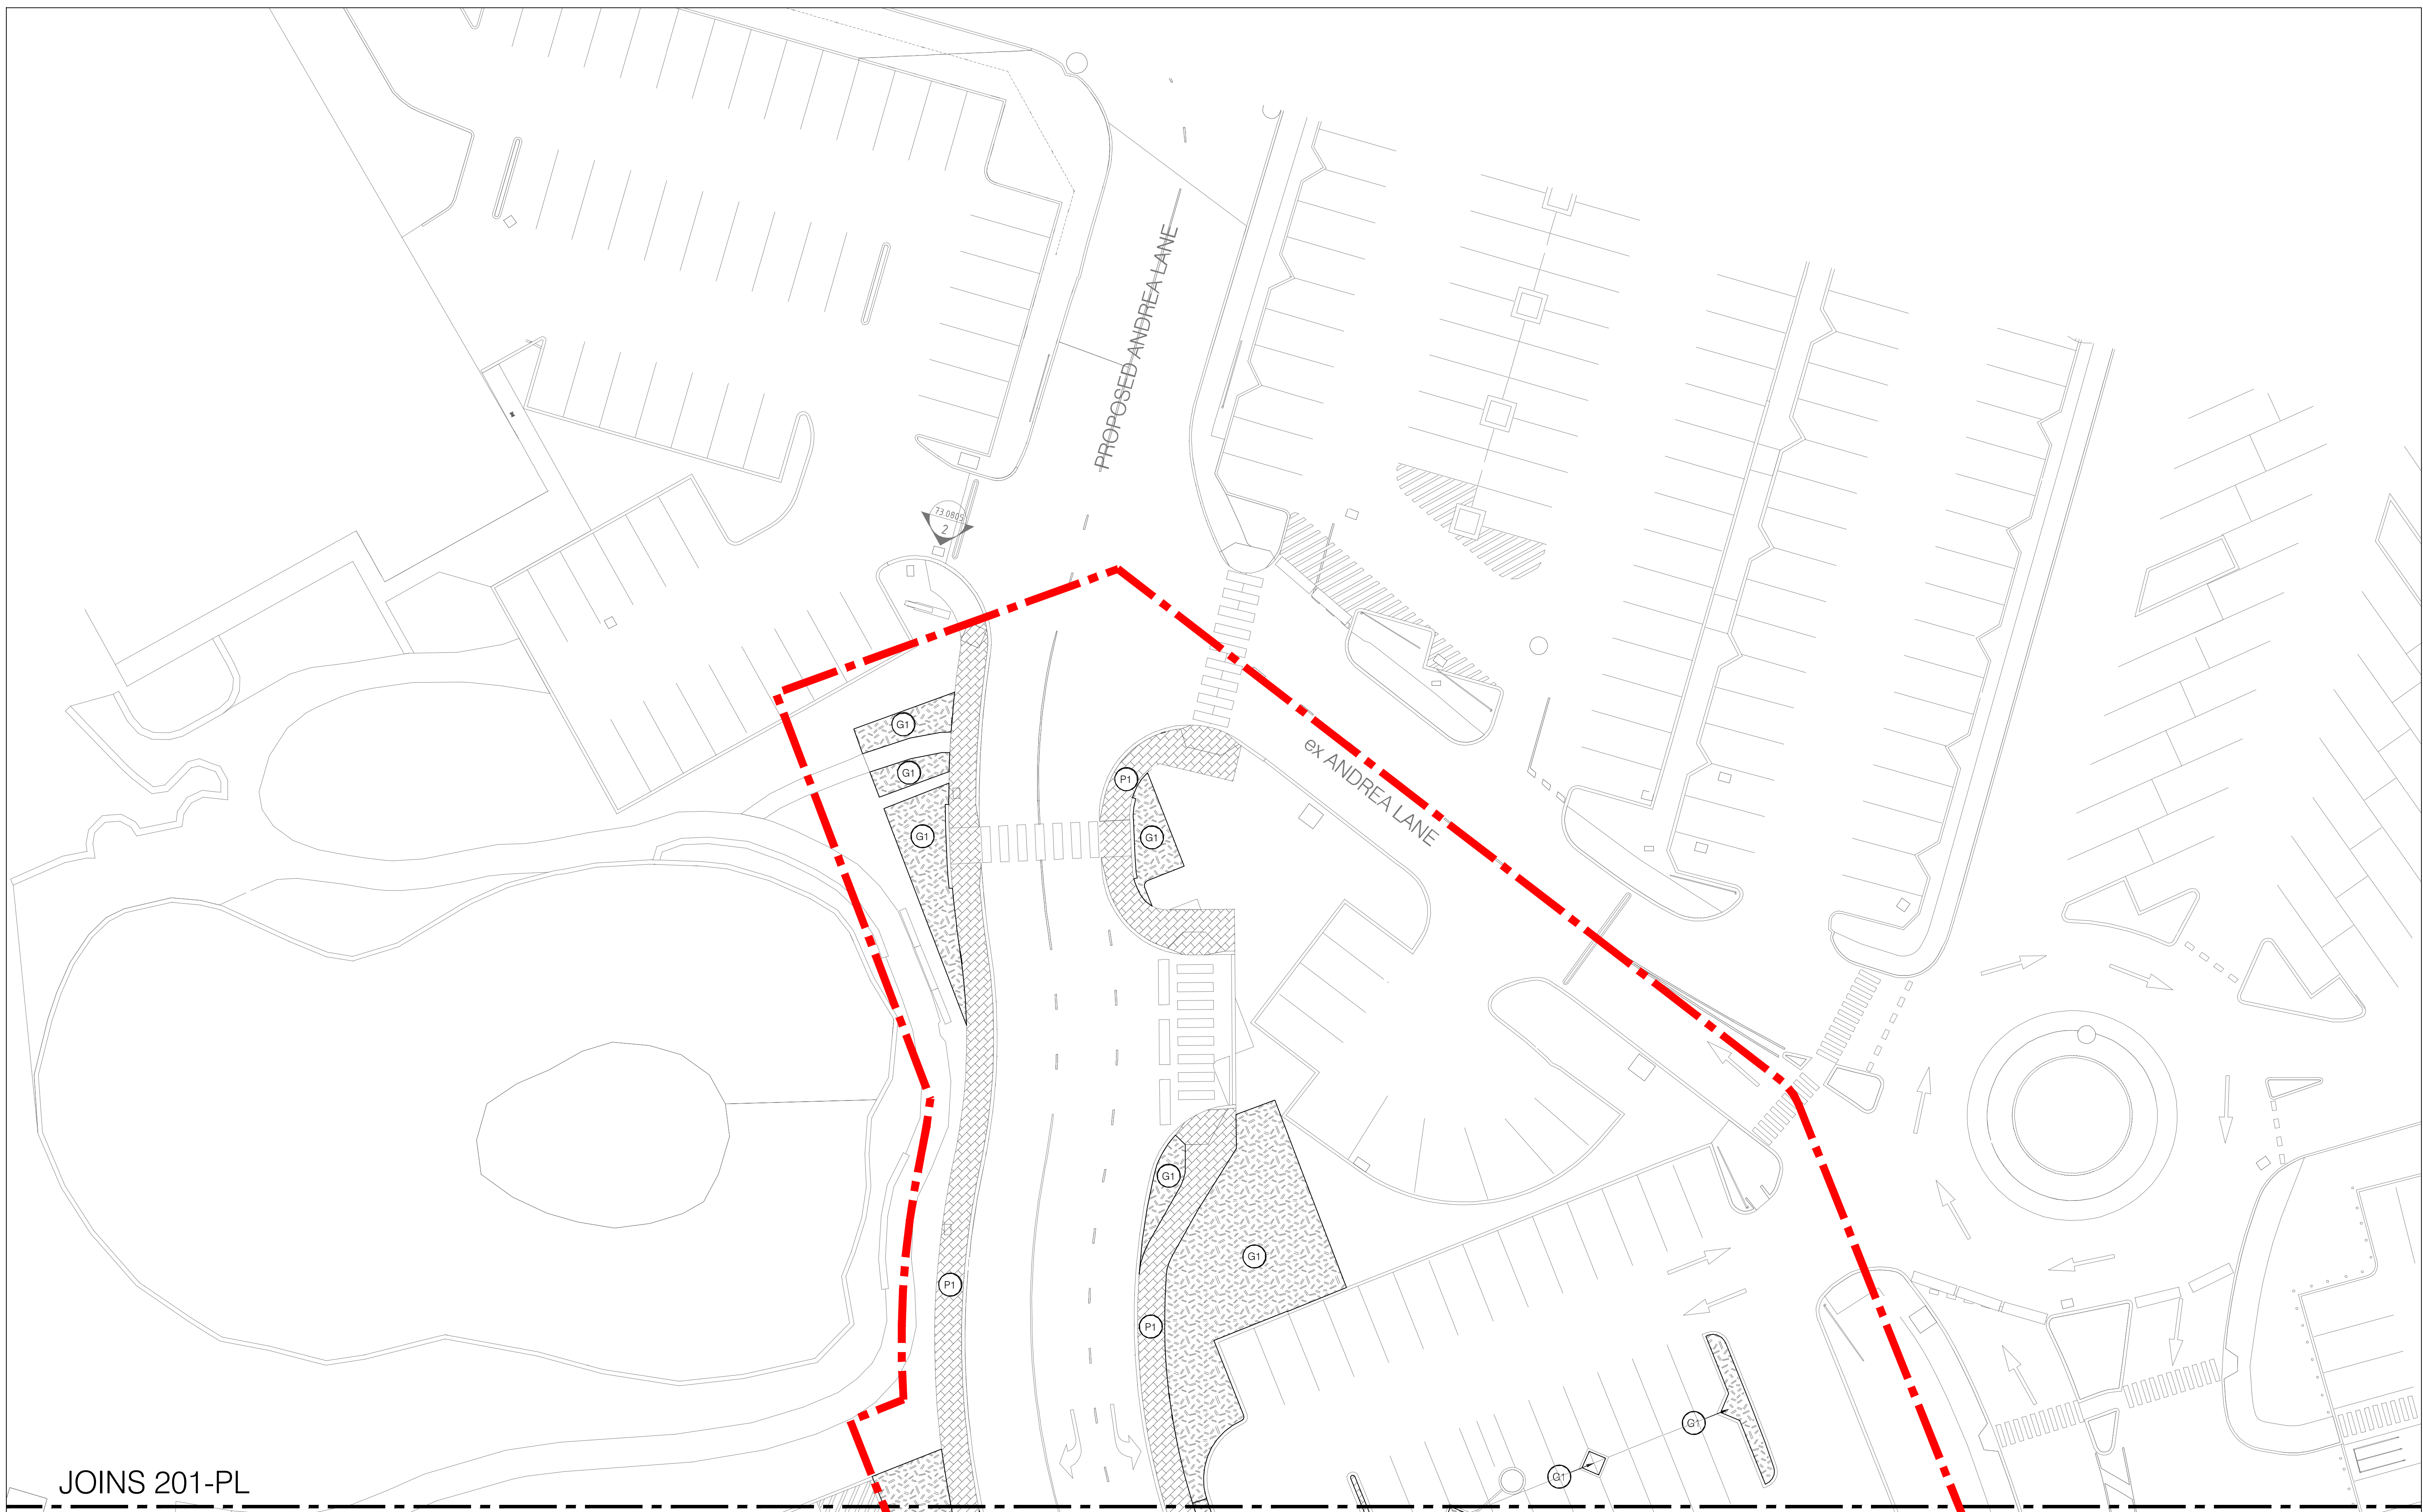

JOINS 201-PL



LEVEL 1, 55 ST GEORGES TCE
PERTH WA 6000 AUSTRALIA
TEL +618 9346 0500
FAX +618 9221 1779
www.urbis.com.au

Urbis Pty Ltd ABN 50 105 256 228
Australia Asia Middle East

Copyright by Urbis Pty Ltd. This drawing, or parts thereof, may not be reproduced for any purpose without the consent of Urbis Pty Ltd. It is implied and has legal backing.

The drawings are to be read in conjunction with the specification and any other written instructions issued.
Any discrepancies shall be referred to the Superintendent for a written decision prior to ordering/ supply/ installation/ construction.

KEY PLAN

LEGEND



EXTENT OF WORKS



SHEET JOIN LINE

NOT FOR CONSTRUCTION

CLIENT

SCENTREGROUP

PROJECT DIRECTOR: M.FREDRIKSSON

A	ISSUED FOR INFORMATION ONLY	DC	PH	24.04.15
REV	DESCRIPTION	DWN	CHK	DATE

PROJECT

GARDEN CITY

ANDREA LANE - EARLY WORKS

DRAWING TITLE

FINISHES PLAN

ISSUE

INFORMATION ONLY

SCALE 1:200 @ A1 1:400 @ A3




DRAWING NO.

202-FI

PROJECT NO.

ND1152

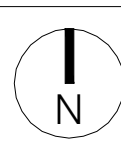

REVISION

A

LAST SAVED: 4/24/2015 10:48 AM BY: DCLANCY

BY: DCLANCY



JOINS 501-PL



LEVEL 1, 55 ST GEORGES TCE
PERTH WA 6000 AUSTRALIA
TEL +618 9346 0500
FAX +618 9221 1779
www.urbis.com.au


Urbis Pty Ltd ABN 50 105 256 228
Australia, Asia, Middle East

Copyright by Urbis Pty Ltd. This drawing, or parts thereof, may not be reproduced for any purpose without the consent of Urbis Pty Ltd. It is implied and has legal backing.

The drawings are to be read in conjunction with the specification and any other written instructions issued.

KEY PLAN

LEGEND

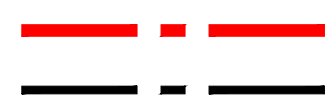

EXTENT OF WORKS

SHEET JOIN LINE

NOT FOR CONSTRUCTION

CLIENT

SCENTREGROUP

PROJECT DIRECTOR: M.FREDRIKSSON

A	ISSUED FOR INFORMATION ONLY	DC	PH	24.04.15
REV	DESCRIPTION	DWN	CHK	DATE

PROJECT

GARDEN CITY

ANDREA LANE - EARLY WORKS

DRAWING TITLE

PLANTING PLAN

ISSUE
INFORMATION ONLY

SCALE 1:200 @ A1 1:400 @ A3



DRAWING NO.

502-PL

PROJECT NO.
ND1152

REVISION

A

T:\003 PROJECTS\CURRENT\ND 1152 - GARDEN CITY LANDSCAPE DESIGN\ANDREA LANE - EARLY WORKS\DRAWINGS\LAYOUTS\502-PL.DWG

LAST SAVED: 4/24/2015 10:48 AM BY: DCLANCY