



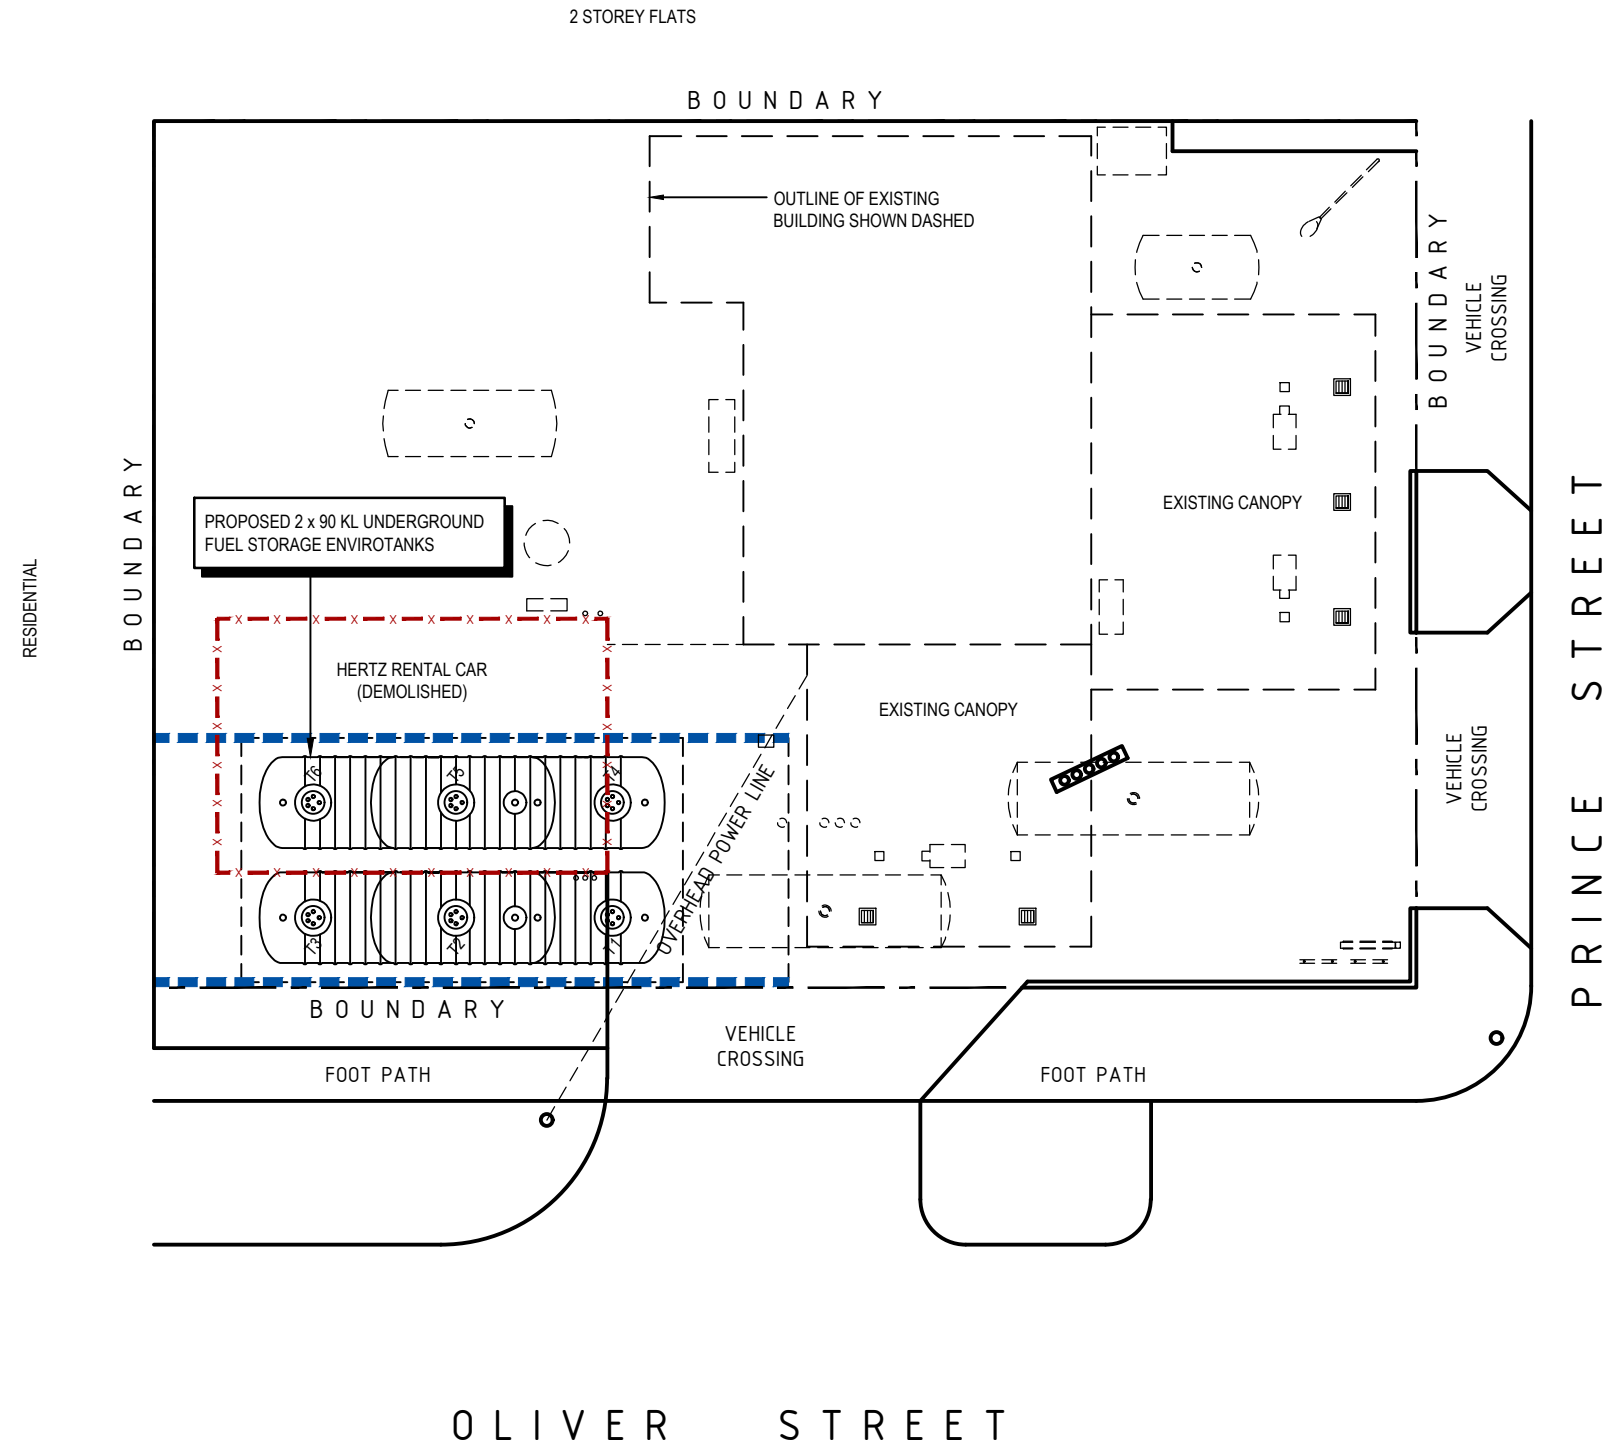

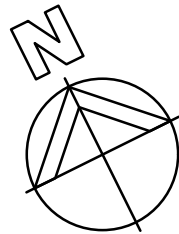

**LEGEND:**

- TEMPORARY SHORING ----
- DEMOLISHED BUILDING -x-x-x-x-

**Richmond+Ross**  
CONSULTING ENGINEERS AND PROJECT LEADERS  
38 Willoughby Road Crows Nest NSW 2065 ABN 34 001 485 436  
Tel: (02) 9490 9600 Fax: (02) 9438 1224


**AMPOL** Ampol Australia Petroleum Pty Ltd  
COPYRIGHT  
THIS DRAWING & DESIGN MUST NOT BE COPIED IN WHOLE OR PART WITHOUT THE WRITTEN CONSENT OF AMPOL AUSTRALIA PETROLEUM PTY LTD.

| REV.     | BY | DATE     | DESCRIPTION OF CHANGE |
|----------|----|----------|-----------------------|
| B        | BA | 10.03.21 | UPSS ASSESSMENT       |
| C        | DC | 15.03.21 | UPSS ASSESSMENT       |
| D        | DC | 22.03.21 | UPSS ASSESSMENT       |
| REVISION |    |          |                       |


|                                             |
|---------------------------------------------|
| PROJECT                                     |
| GRAFTON NSW<br>179 PRINCE STREET<br>GRAFTON |

|                      |
|----------------------|
| TITLE                |
| PROPOSED FUEL SYSTEM |

|       |          |             |      |
|-------|----------|-------------|------|
| DRAWN | DATE     | APPROVED    | DATE |
| DC    | 09.03.21 |             |      |
| SCALE | SIZE     | DRAWING No. | REV. |
| 250   | A3       | 210077-A02  | D    |

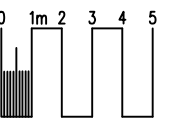


PRELIMINARY

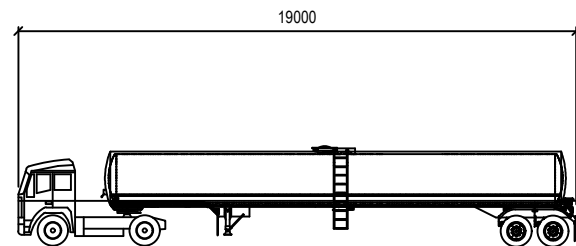

FH 13 4x2 Low WB 3600 - Walker Foodliner

|               |        |                    |        |
|---------------|--------|--------------------|--------|
|               | mm     |                    |        |
| Tractor Width | : 2550 | Lock to Lock Time  | : 6.0  |
| Trailer Width | : 2438 | Steering Angle     | : 17.6 |
| Tractor Track | : 2550 | Articulating Angle | : 70.0 |
| Trailer Track | : 2438 |                    |        |

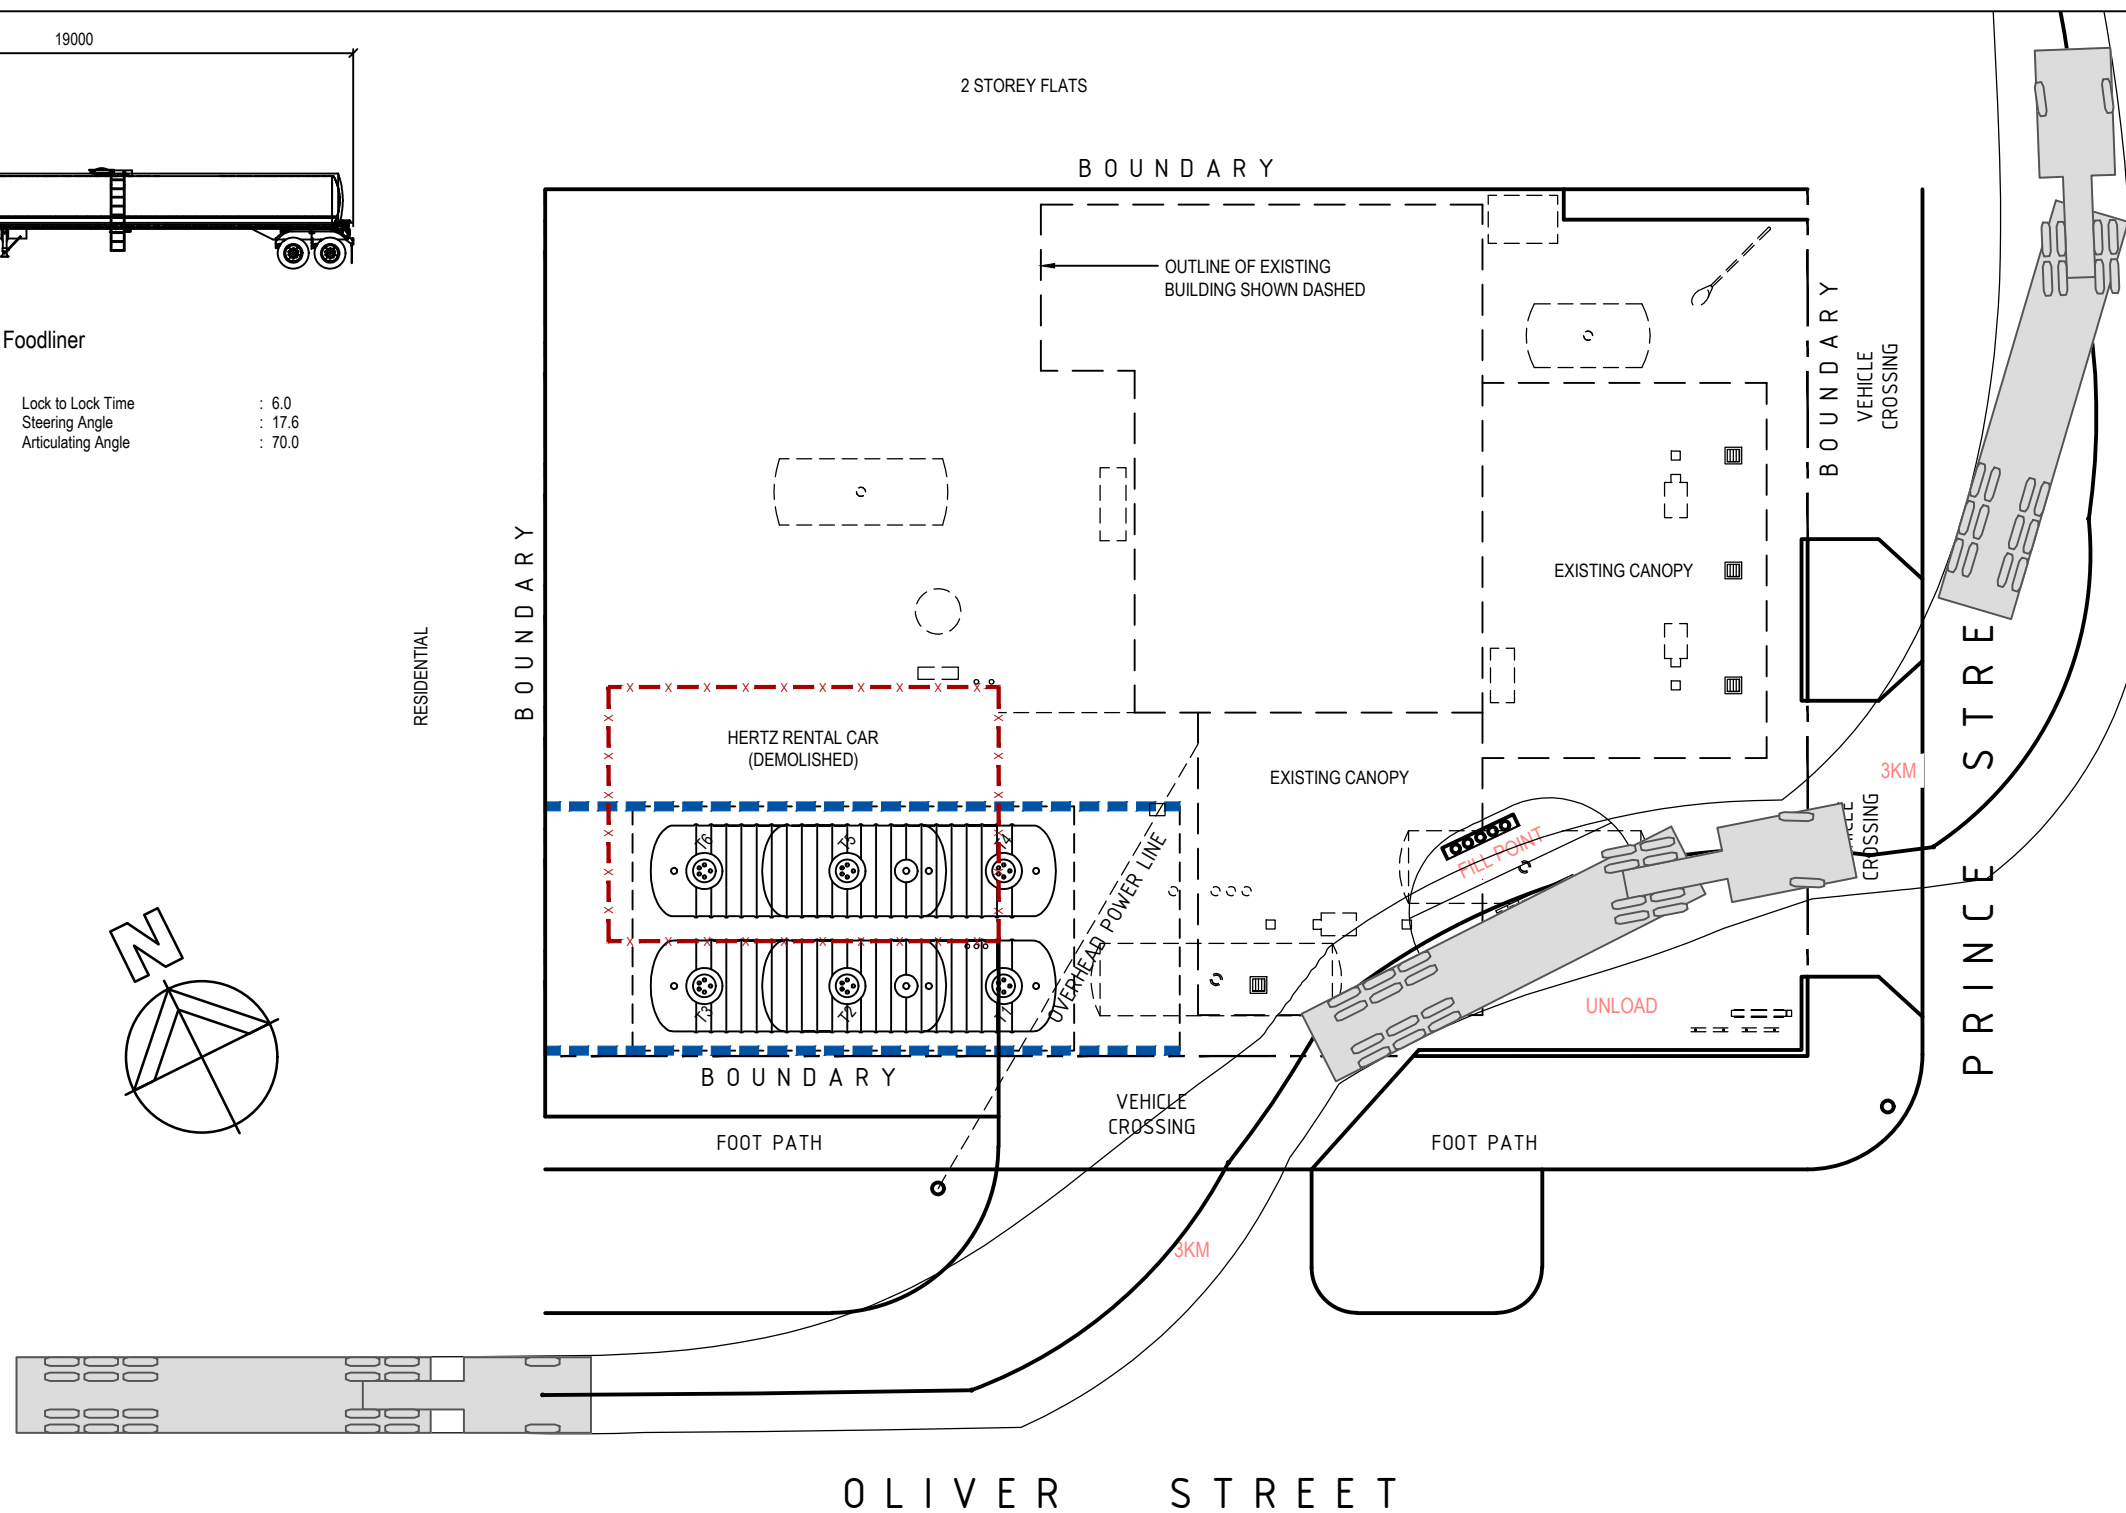


**Richmond+Ross**  
CONSULTING ENGINEERS AND PROJECT LEADERS  
38 Willoughby Road Crows Nest NSW 2065 ABN 34 001 485 436  
Tel: (02) 9490 9600 Fax: (02) 9438 1224

**LEGEND:**  
TEMPORARY SHORING   
DEMOLISHED BUILDING

PRELIMINARY


Ampol Australia Petroleum Pty Ltd  
COPYRIGHT  
THIS DRAWING & DESIGN MUST NOT BE COPIED IN WHOLE OR PART WITHOUT THE WRITTEN CONSENT OF AMPOL AUSTRALIA PETROLEUM PTY LTD.

| REV.     | BY | DATE     | DESCRIPTION OF CHANGE | PROJECT                                     | TITLE       | DRAWN | DATE     | APPROVED    | DATE |
|----------|----|----------|-----------------------|---------------------------------------------|-------------|-------|----------|-------------|------|
| B        | BA | 10.03.21 | UPSS ASSESSMENT       | GRAFTON NSW<br>179 PRINCE STREET<br>GRAFTON | TANKER PATH | DC    | 09.03.21 |             |      |
| C        | DC | 15.03.21 | UPSS ASSESSMENT       |                                             |             | SCALE | SIZE     | DRAWING No. | REV. |
| D        | DC | 22.03.21 | UPSS ASSESSMENT       |                                             |             | 250   | A3       | 210077-A03  | D    |
| REVISION |    |          |                       |                                             |             |       |          |             |      |

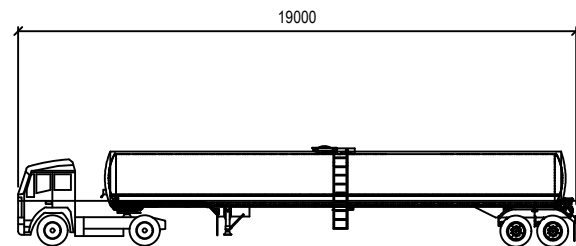


FH 13 4x2 Low WB 3600 - Walker Foodliner

|               |        |                    |        |
|---------------|--------|--------------------|--------|
|               | mm     |                    |        |
| Tractor Width | : 2550 | Lock to Lock Time  | : 6.0  |
| Trailer Width | : 2438 | Steering Angle     | : 17.6 |
| Tractor Track | : 2550 | Articulating Angle | : 70.0 |
| Trailer Track | : 2438 |                    |        |

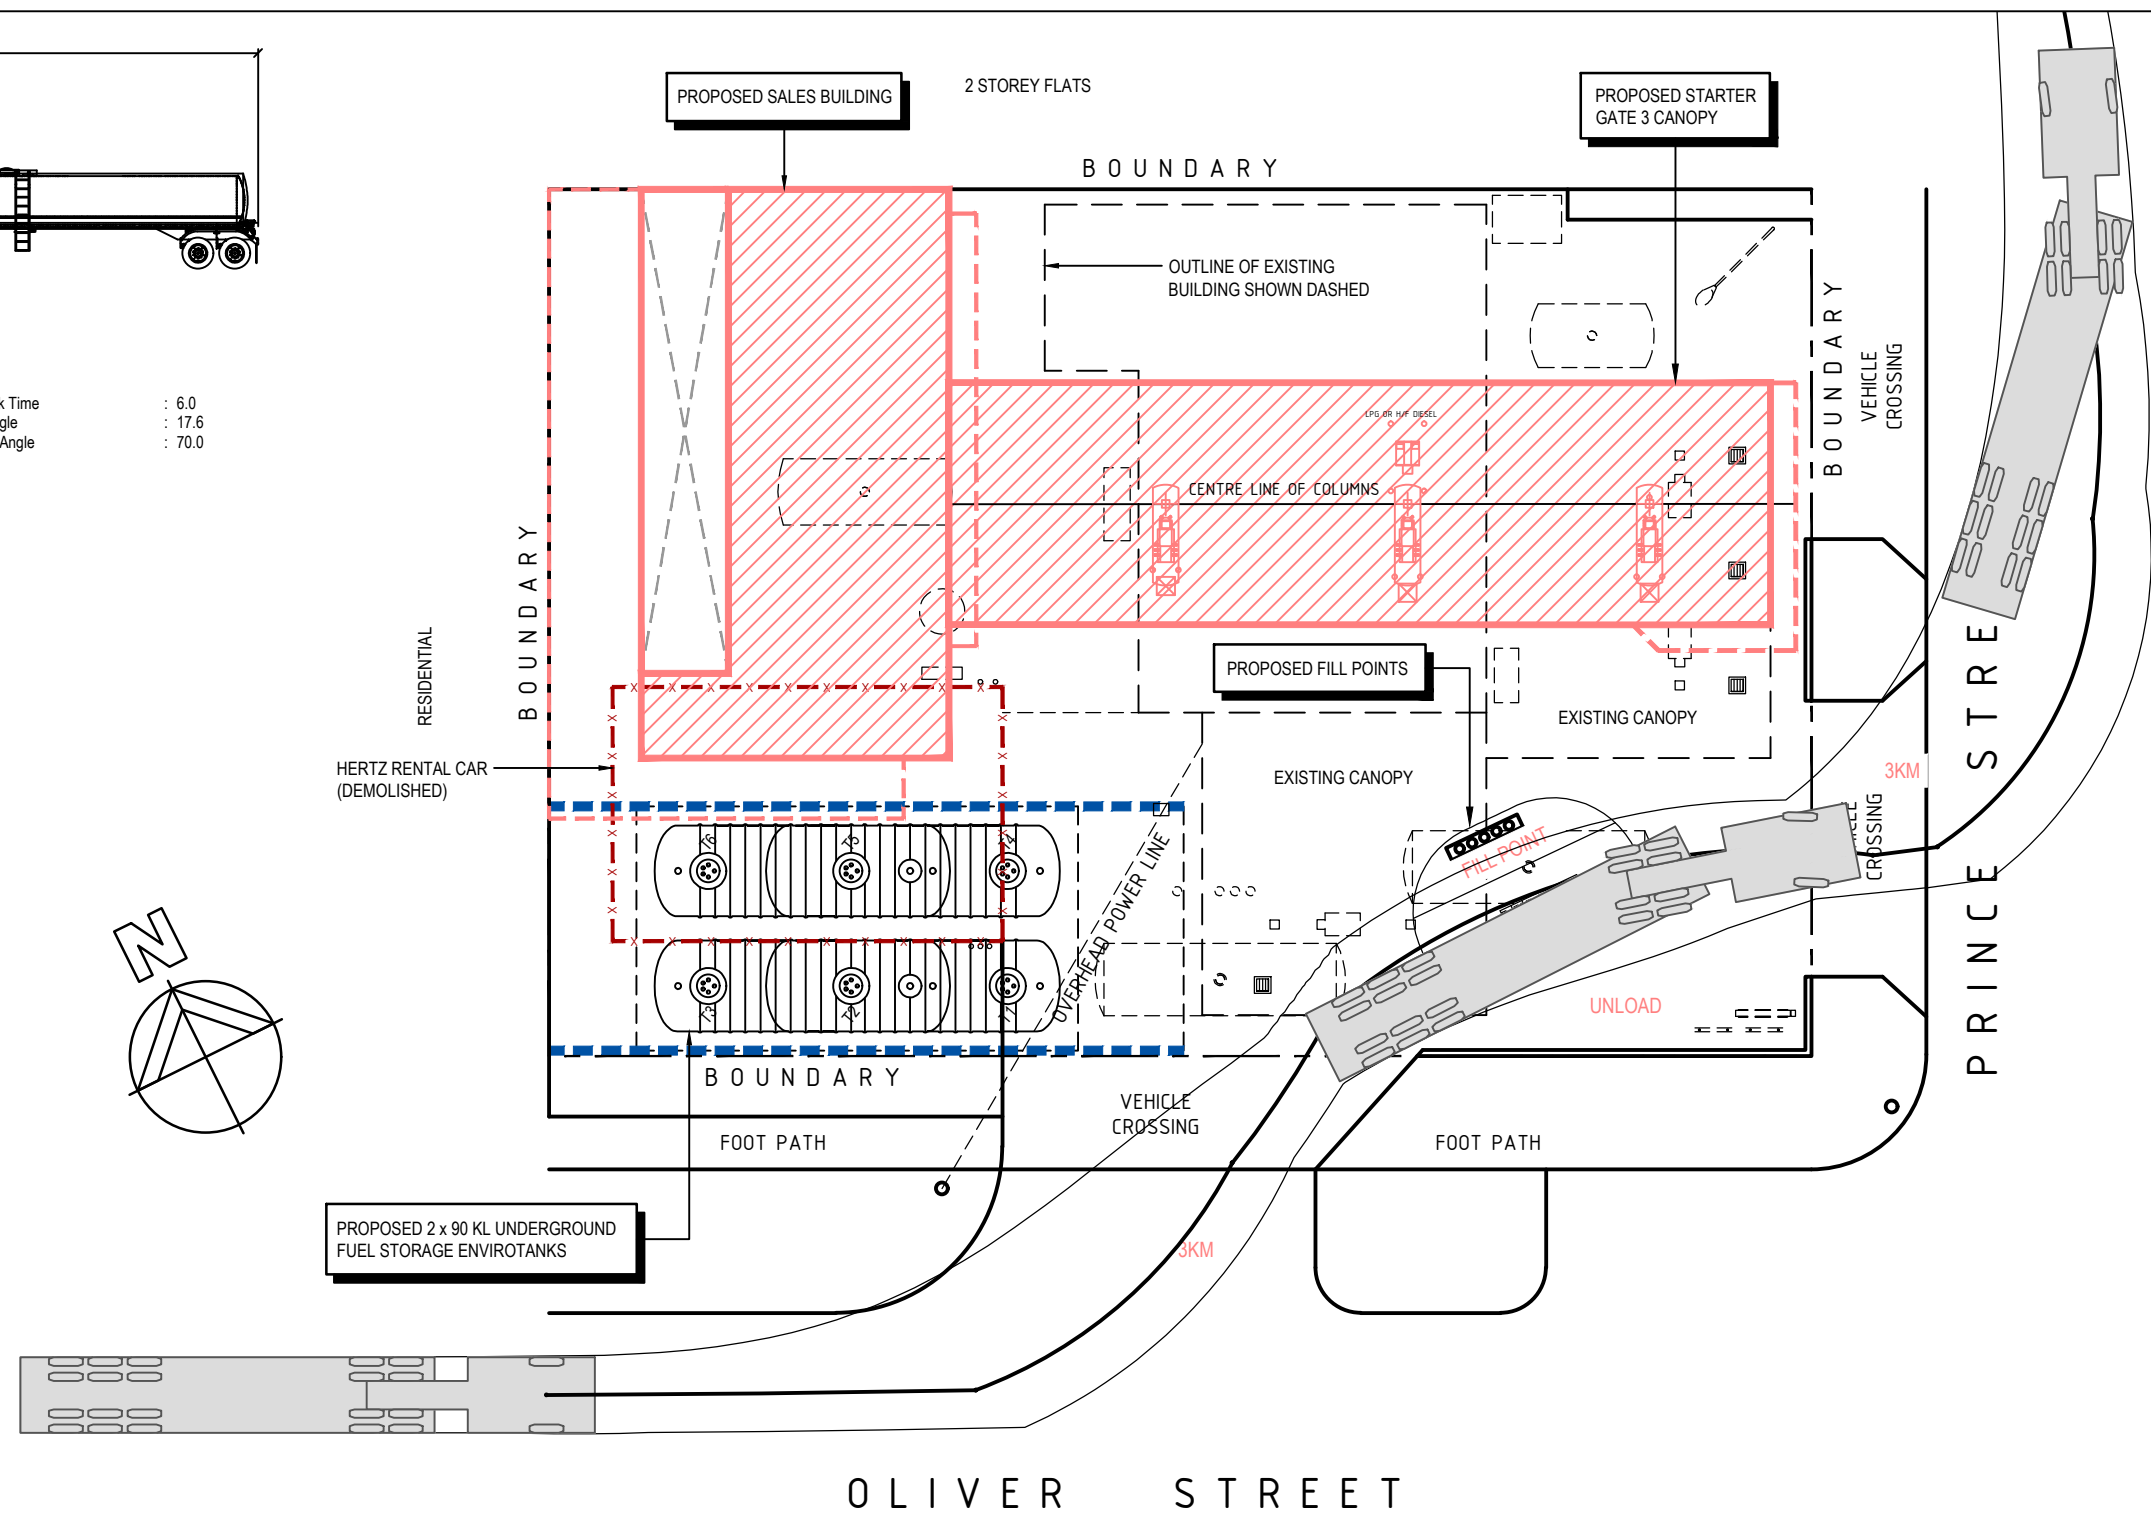

**Richmond+Ross**  
CONSULTING ENGINEERS AND PROJECT LEADERS  
38 Willoughby Road Crows Nest NSW 2065 ABN 34 001 485 436  
Tel: (02) 9490 9600 Fax: (02) 9438 1224

**LEGEND:**  
TEMPORARY SHORING   
DEMOLISHED BUILDING

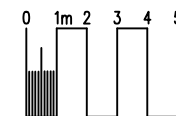

PRELIMINARY

**Ampol Australia Petroleum Pty Ltd**  
COPYRIGHT  
THIS DRAWING & DESIGN MUST NOT BE COPIED IN  
WHOLE OR PART WITHOUT THE WRITTEN CONSENT OF  
AMPOL AUSTRALIA PETROLEUM PTY LTD.

| REV.     | BY | DATE     | DESCRIPTION OF CHANGE | PROJECT                                     | TITLE                      | DRAWN | DATE     | APPROVED    | DATE |
|----------|----|----------|-----------------------|---------------------------------------------|----------------------------|-------|----------|-------------|------|
| B        | BA | 10.03.21 | UPSS ASSESSMENT       | GRAFTON NSW<br>179 PRINCE STREET<br>GRAFTON | PRELIMINARY KDR ASSESSMENT | DC    | 09.03.21 |             |      |
| C        | DC | 15.03.21 | UPSS ASSESSMENT       |                                             |                            | SCALE | SIZE     | DRAWING No. | REV. |
| D        | DC | 22.03.21 | UPSS ASSESSMENT       |                                             |                            | 250   | A3       | 210077-A04  | D    |
| REVISION |    |          |                       |                                             |                            |       |          |             |      |